


INTELLECTUAL NOTICE: THE CONTENT OF THIS DOCUMENT IS SOLELY THE PROPERTY OF MICRON CORPORATION AND IS NOT TO BE REPRODUCED, COPIED, OR TRANSMITTED IN ANY FORM OR BY ANY MEANS, ELECTRONIC OR MECHANICAL, INCLUDING PHOTOCOPYING, RECORDING, OR BY ANY INFORMATION STORAGE AND RETRIEVAL SYSTEM. ANY UNAUTHORIZED REPRODUCTION OR TRANSMISSION OF THIS DOCUMENT IS STRICTLY PROHIBITED AND WILL BE PUNISHED BY LAW. MICRON CORPORATION SHALL NOT BE LIABLE FOR ANY DAMAGES, INCLUDING CONSEQUENTIAL DAMAGES, ARISING FROM THE USE OF THIS DOCUMENT. THE CONTENT OF THIS DOCUMENT IS SOLELY THE PROPERTY OF MICRON CORPORATION AND IS NOT TO BE REPRODUCED, COPIED, OR TRANSMITTED IN ANY FORM OR BY ANY MEANS, ELECTRONIC OR MECHANICAL, INCLUDING PHOTOCOPYING, RECORDING, OR BY ANY INFORMATION STORAGE AND RETRIEVAL SYSTEM. ANY UNAUTHORIZED REPRODUCTION OR TRANSMISSION OF THIS DOCUMENT IS STRICTLY PROHIBITED AND WILL BE PUNISHED BY LAW. MICRON CORPORATION SHALL NOT BE LIABLE FOR ANY DAMAGES, INCLUDING CONSEQUENTIAL DAMAGES, ARISING FROM THE USE OF THIS DOCUMENT.

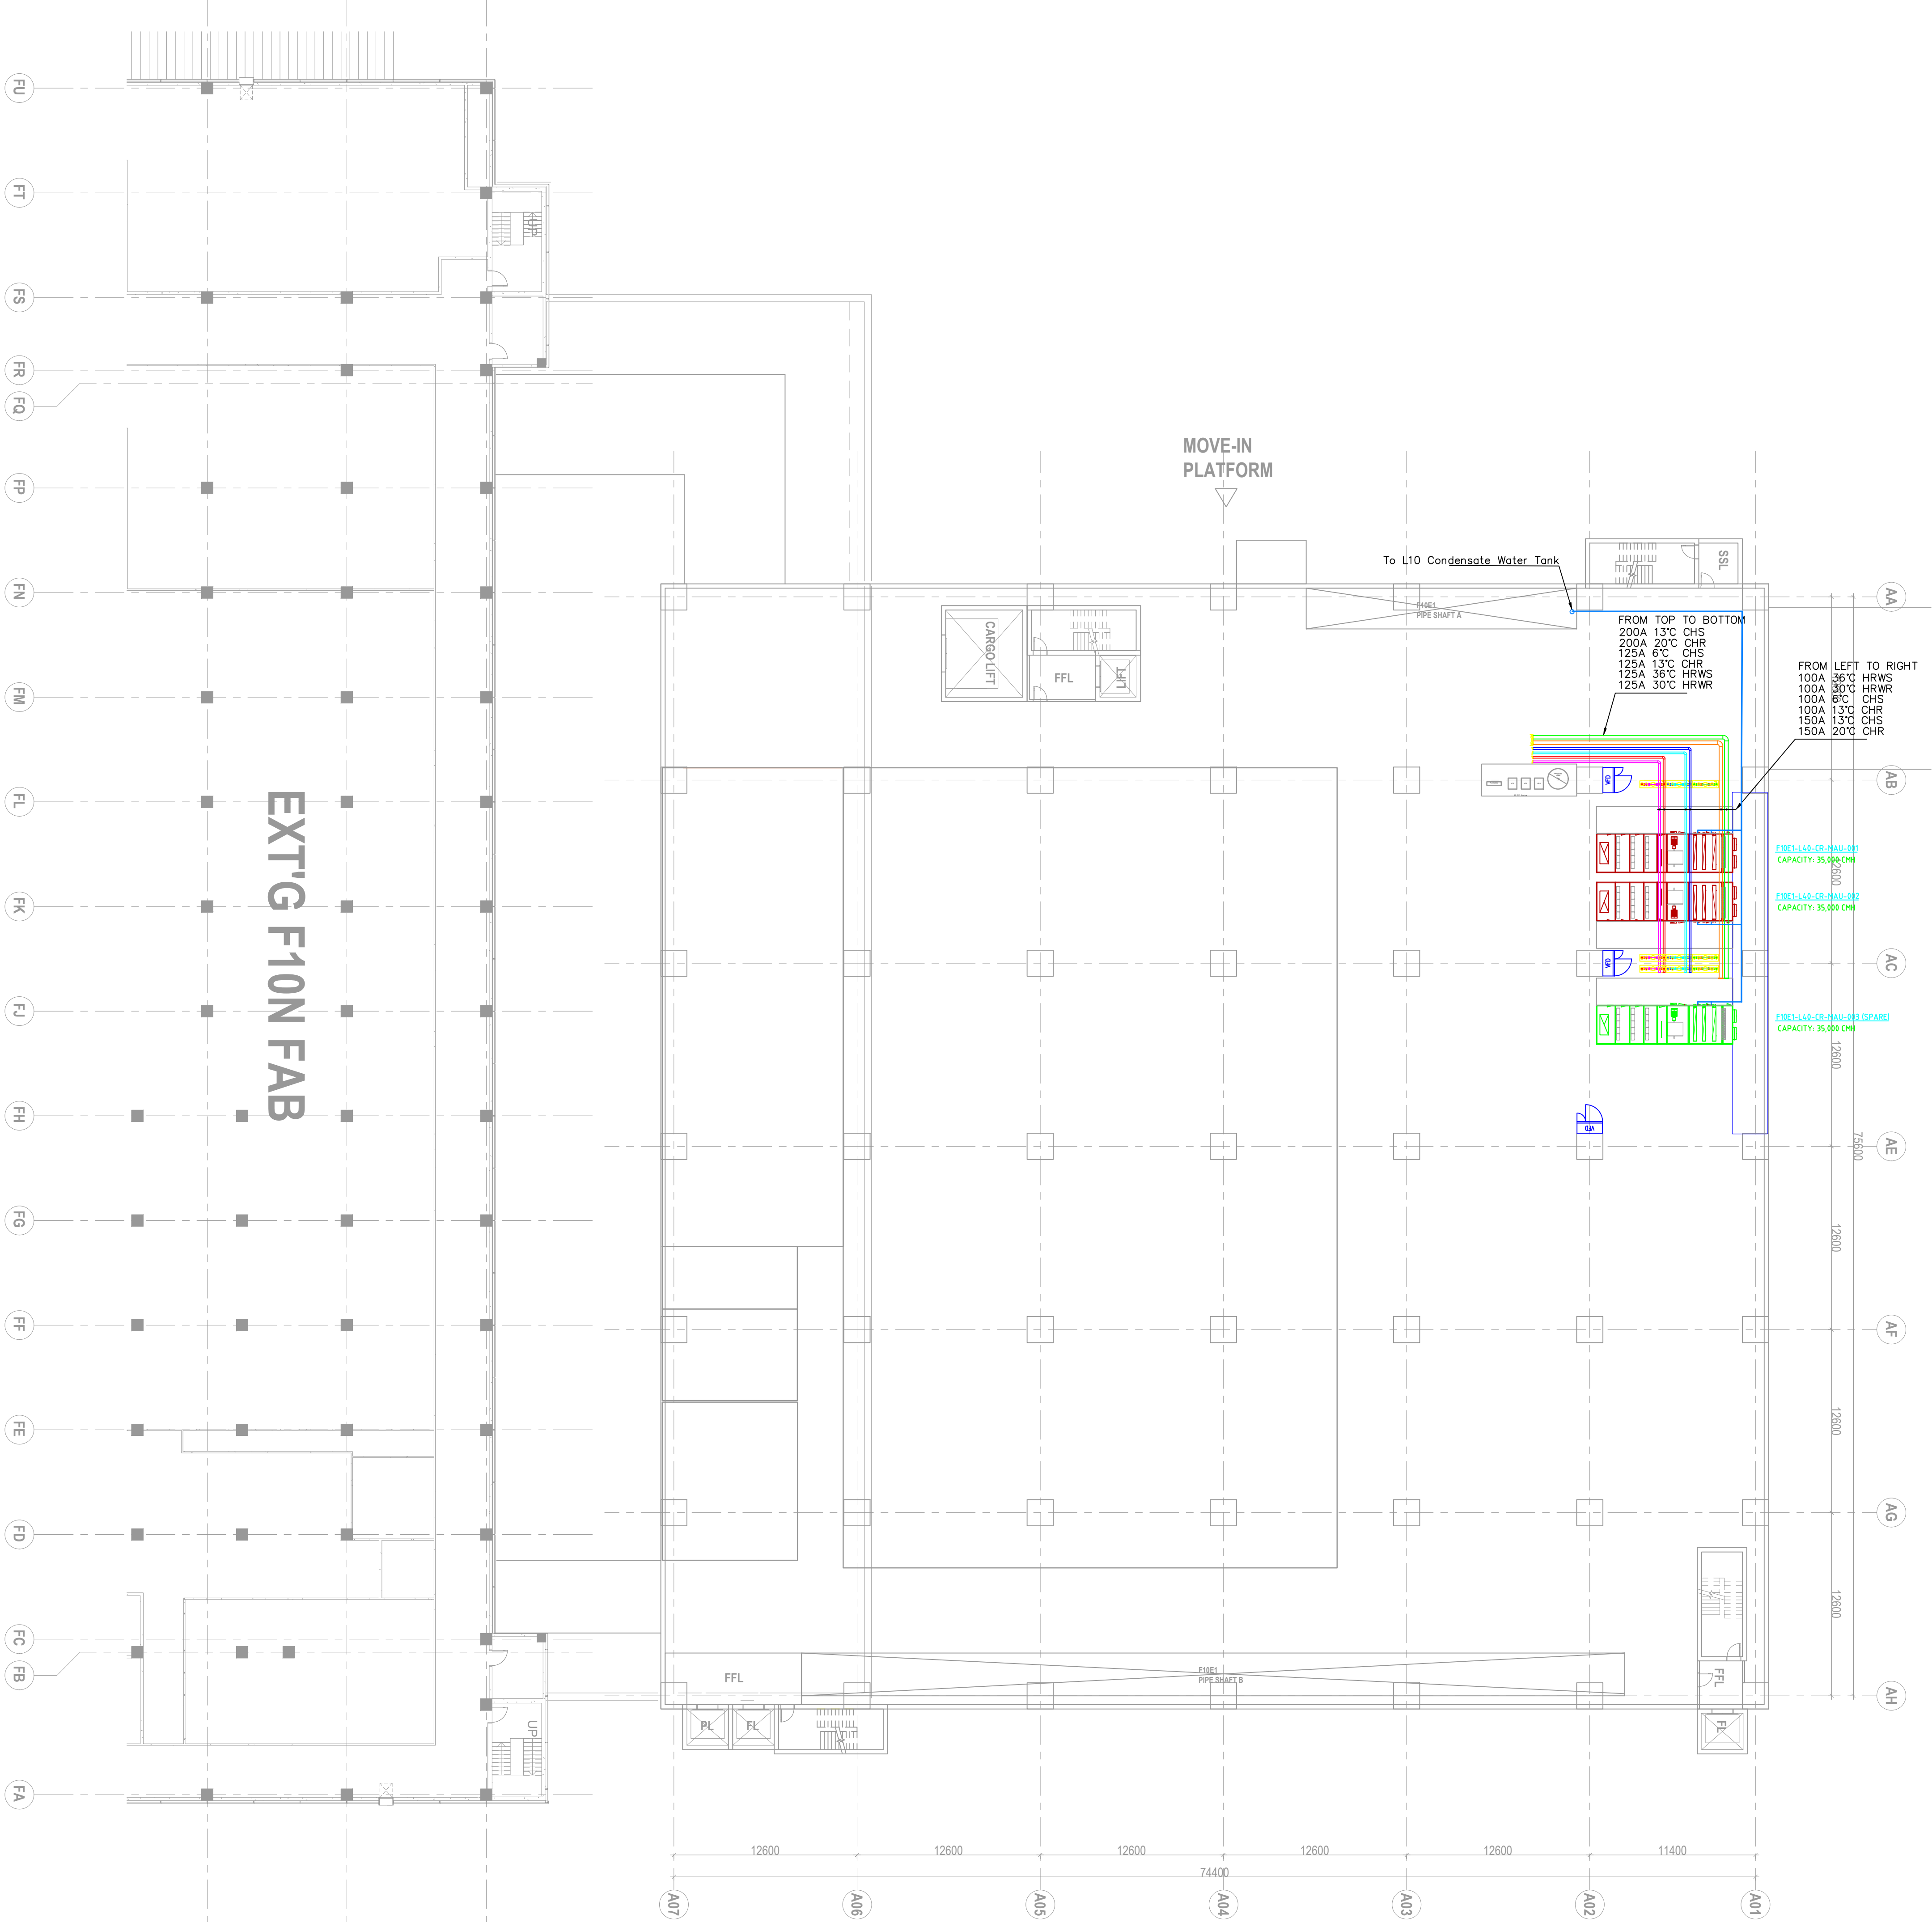

OWNER / DEVELOPER

ARCHITECTURAL CONSULTANT

CIVIL & STRUCTURAL CONSULTANT

MECHANICAL & ELECTRICAL CONSULTANT

DESIGN MANAGER

CTCI Singapore Pte. Ltd.

PROJECT ADDRESS
North Coast Drive, Singapore

KEY PLAN

Secret
R3
Level

FOR REVIEW

REV	DATE	DESCRIPTION Revisions	ISSUED BY

PROJECT TITLE

F10E1 L40 MAU Piping LAYOUT

PROJECT PHASE

A&E

DRAWING TITLE

Floor Plan
MAU Piping LAYOUT F10E1 L40

DESIGNED :	設計者	DRAWN :	作者	CHECKED :	審圖員
DATE :	02/12/26	JOB NO. :	SCALE :		
Micron DRAWING NO.	F01-F10E-LAY-F10E1-04-K-132				REV
CTCI DRAWING NO.					B
Reference Model					
CTCI	SHEET: 1 OF 1				SIZE: A1