


INTELLECTUAL NOTICE: THE CONTENT OF THIS DOCUMENT IS SENSITIVE INFORMATION AND OWNED BY MICRON CORPORATION AND PROTECTED BY COPYRIGHT LAWS AND RELEVANT LAWS/REGULATIONS. ONLY EMPLOYEES OF MICRON ARE ALLOWED TO ACCESS AND USE THIS SENSITIVE INFORMATION WITHIN THE WORK SCOPE. UNLESS THEY SPECIFICALLY AND EXPLICITLY OBTAIN PERMISSION FROM MICRON, ANY OTHER PARTY WITHOUT MICRON'S WRITTEN PERMISSION IS PROHIBITED FROM REPRODUCING, DISTRIBUTING, OR DISCLOSING THIS DOCUMENT IN ANY MANNER TO ANY OTHER PARTY WITHOUT MICRON'S WRITTEN PERMISSION.

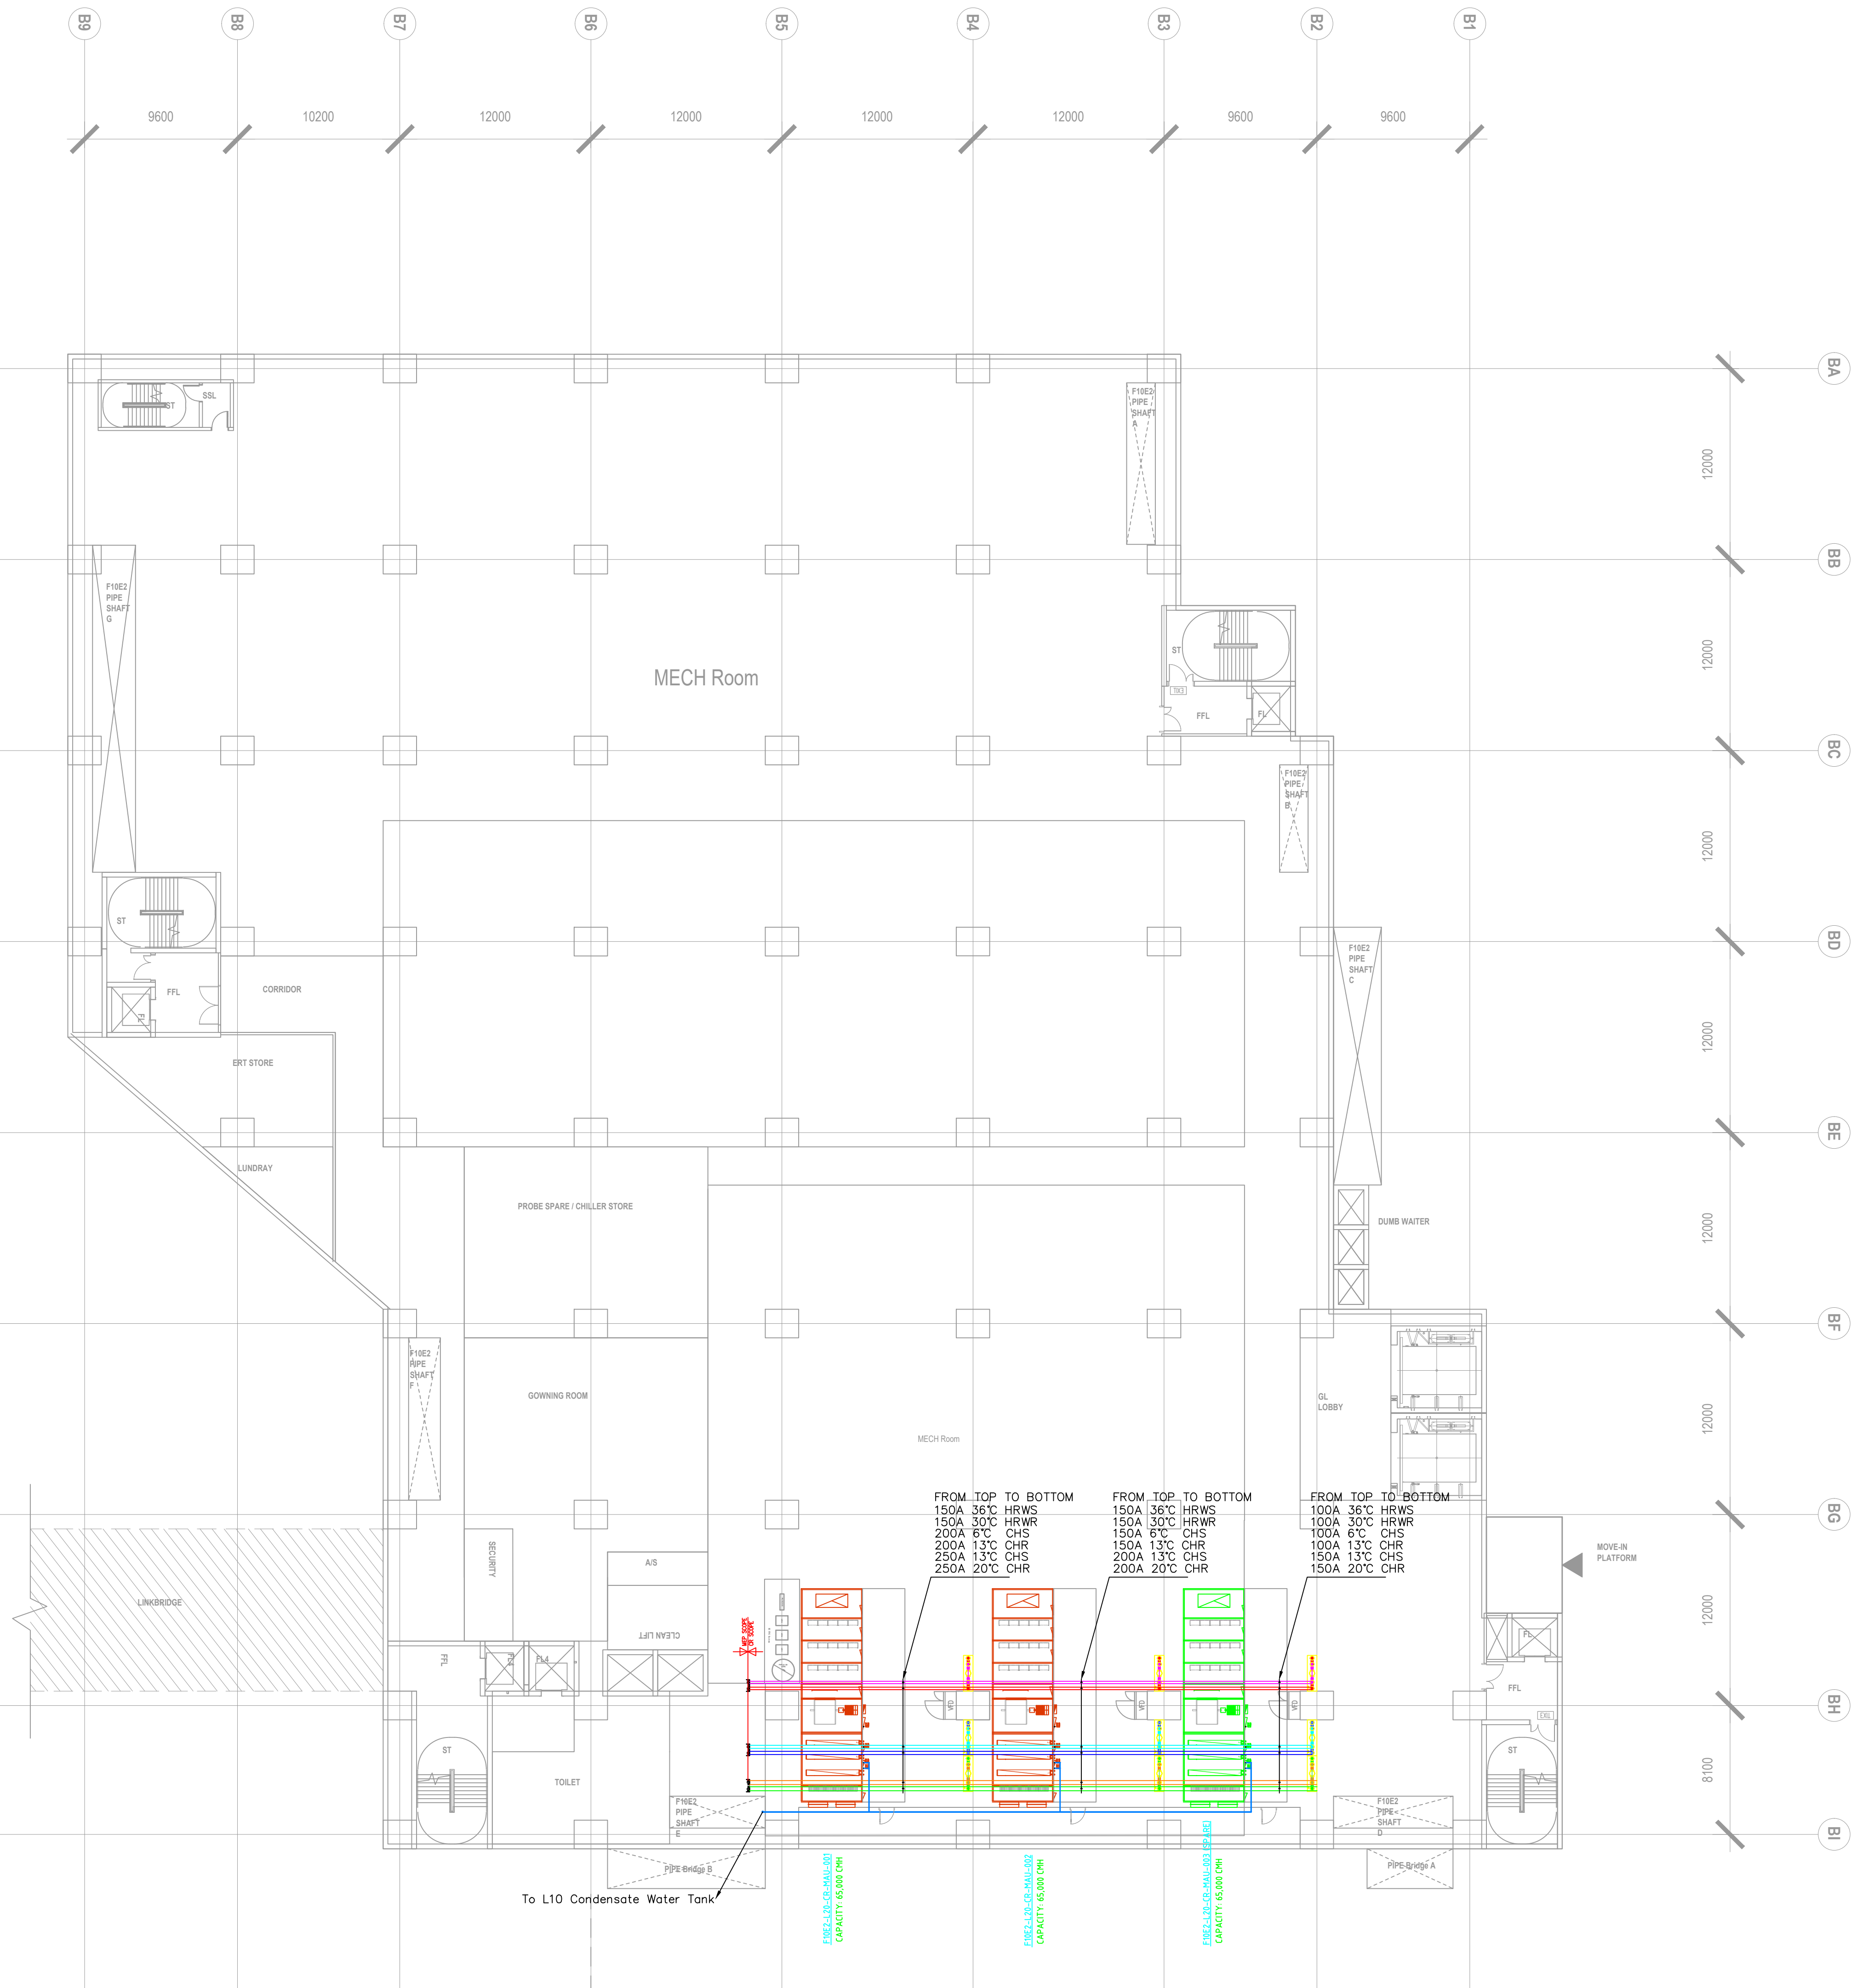

OWNER / DEVELOPER
micronTM


ARCHITECTURAL CONSULTANT

CIVIL & STRUCTURAL CONSULTANT

MECHANICAL & ELECTRICAL CONSULTANT

DESIGN MANAGER
CTCI CTCI Singapore Pte. Ltd.

PROJECT ADDRESS
North Coast Drive, Singapore

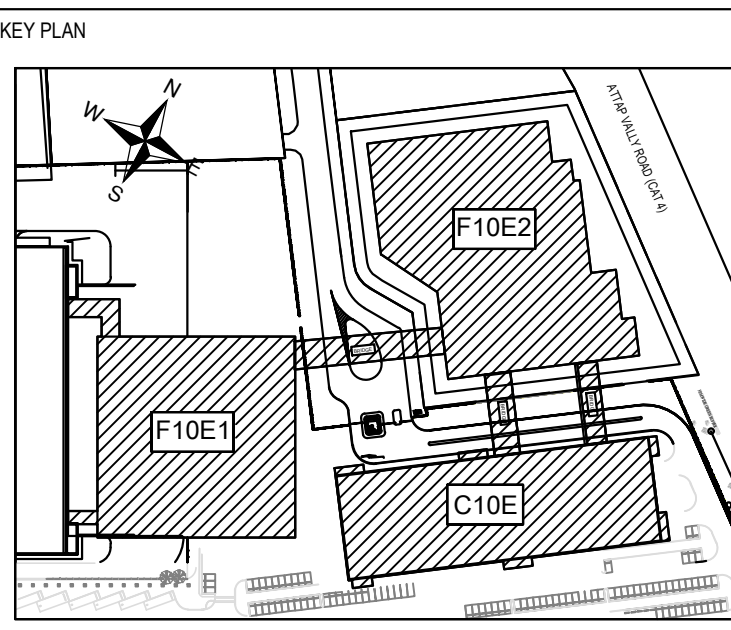

Secret
R3
Level

FOR REVIEW

REV	DATE	DESCRIPTION Revisions	ISSUED BY

PROJECT TITLE
Micron F10E Probe Project

PROJECT PHASE
A&E

DRAWING TITLE
**Floor Plan
MAU Piping Layout F10E2 L20**

DESIGNED : 設計者	DRAWN : 作者	CHECKED : 審圖員
DATE : 02/12/26	JOB NO. :	SCALE :
Micron DRAWING NO. : F01-F10E-LAY-F10E2-02-K-132	REV	
CTCI DRAWING NO. :	B	
Reference Model	SHEET: 1 OF 1	
CTCI	SIZE A1	