


INTELLECTUAL NOTICE: THE CONTENT OF THIS DOCUMENT IS SENSITIVE INFORMATION AND OWNED BY MICRON CORPORATION AND IS PROTECTED BY COPYRIGHT LAWS AND RELATED LAWS. NO PART OF THIS DOCUMENT IS TO BE REPRODUCED, COPIED, OR TRANSMITTED IN ANY FORM OR BY ANY MEANS, ELECTRONIC OR MECHANICAL, INCLUDING PHOTOCOPYING, RECORDING, OR BY ANY INFORMATION STORAGE AND RETRIEVAL SYSTEM, WITHOUT THE WRITTEN PERMISSION OF MICRON CORPORATION. ANY UNAUTHORIZED REPRODUCTION OR DISTRIBUTION OF THIS DOCUMENT IS STRICTLY PROHIBITED AND WILL BE PUNISHED BY LAW. THIS DOCUMENT IS THE PROPERTY OF MICRON CORPORATION AND IS TO BE KEPT IN CONFIDENTIALITY. IT IS TO BE DESTROYED WHEN NO LONGER REQUIRED FOR THE PROJECT. ANY REPRODUCTION OR DISTRIBUTION OF THIS DOCUMENT IS STRICTLY PROHIBITED AND WILL BE PUNISHED BY LAW.

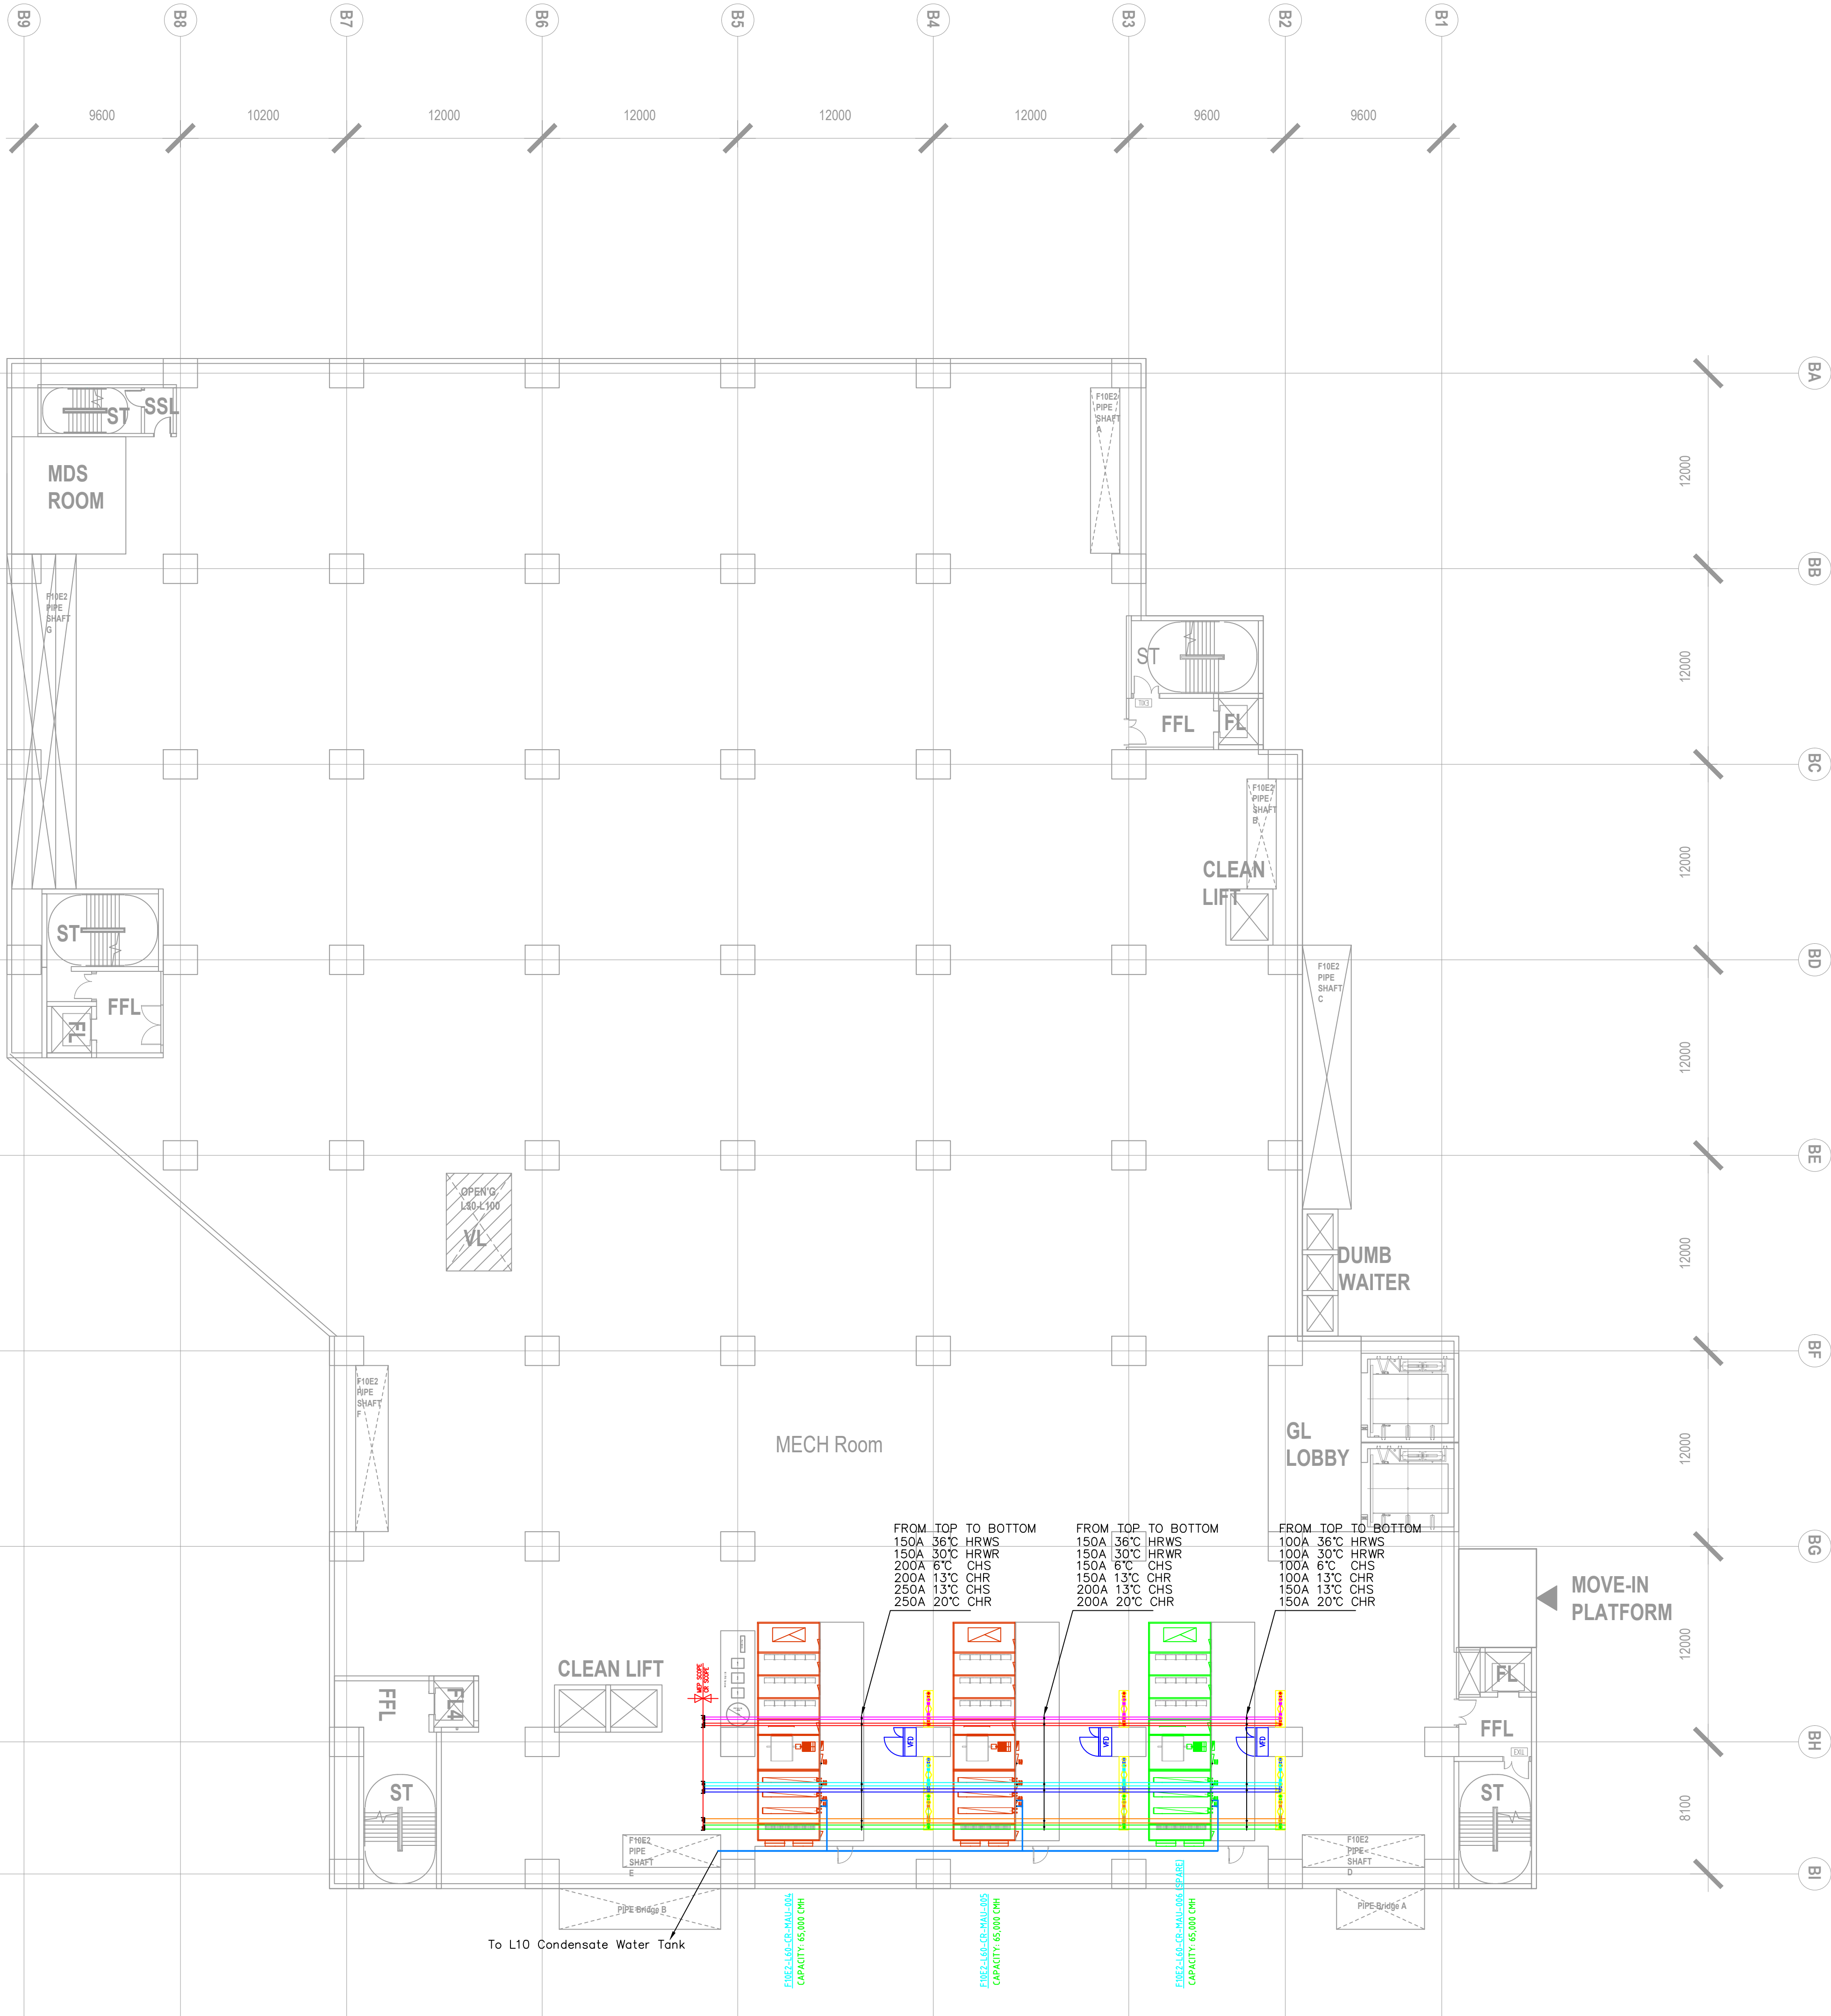

OWNER / DEVELOPER

ARCHITECTURAL CONSULTANT

CIVIL & STRUCTURAL CONSULTANT

MECHANICAL & ELECTRICAL CONSULTANT

DESIGN MANAGER

CTCI Singapore Pte. Ltd.

PROJECT ADDRESS
North Coast Drive, Singapore

KEY PLAN

Secret
R3
Level

FOR REVIEW

REV	DATE	DESCRIPTION Revisions	ISSUED BY

PROJECT TITLE
Micron F10E Probe Project

PROJECT PHASE
A&E

DRAWING TITLE
Floor Plan
MAU Piping Layout F10E2 L60

DESIGNED : 設計者	DRAWN : 作者	CHECKED : 審圖員
DATE : 02/12/26	JOB NO. :	SCALE :
Micron DRAWING NO. : F01-F10E-LAY-F10E2-06-K-132	REV	
CTCI REFERENCE NO. :	B	
Reference Model	SHEET: 1 OF 1	SIZE: A1