


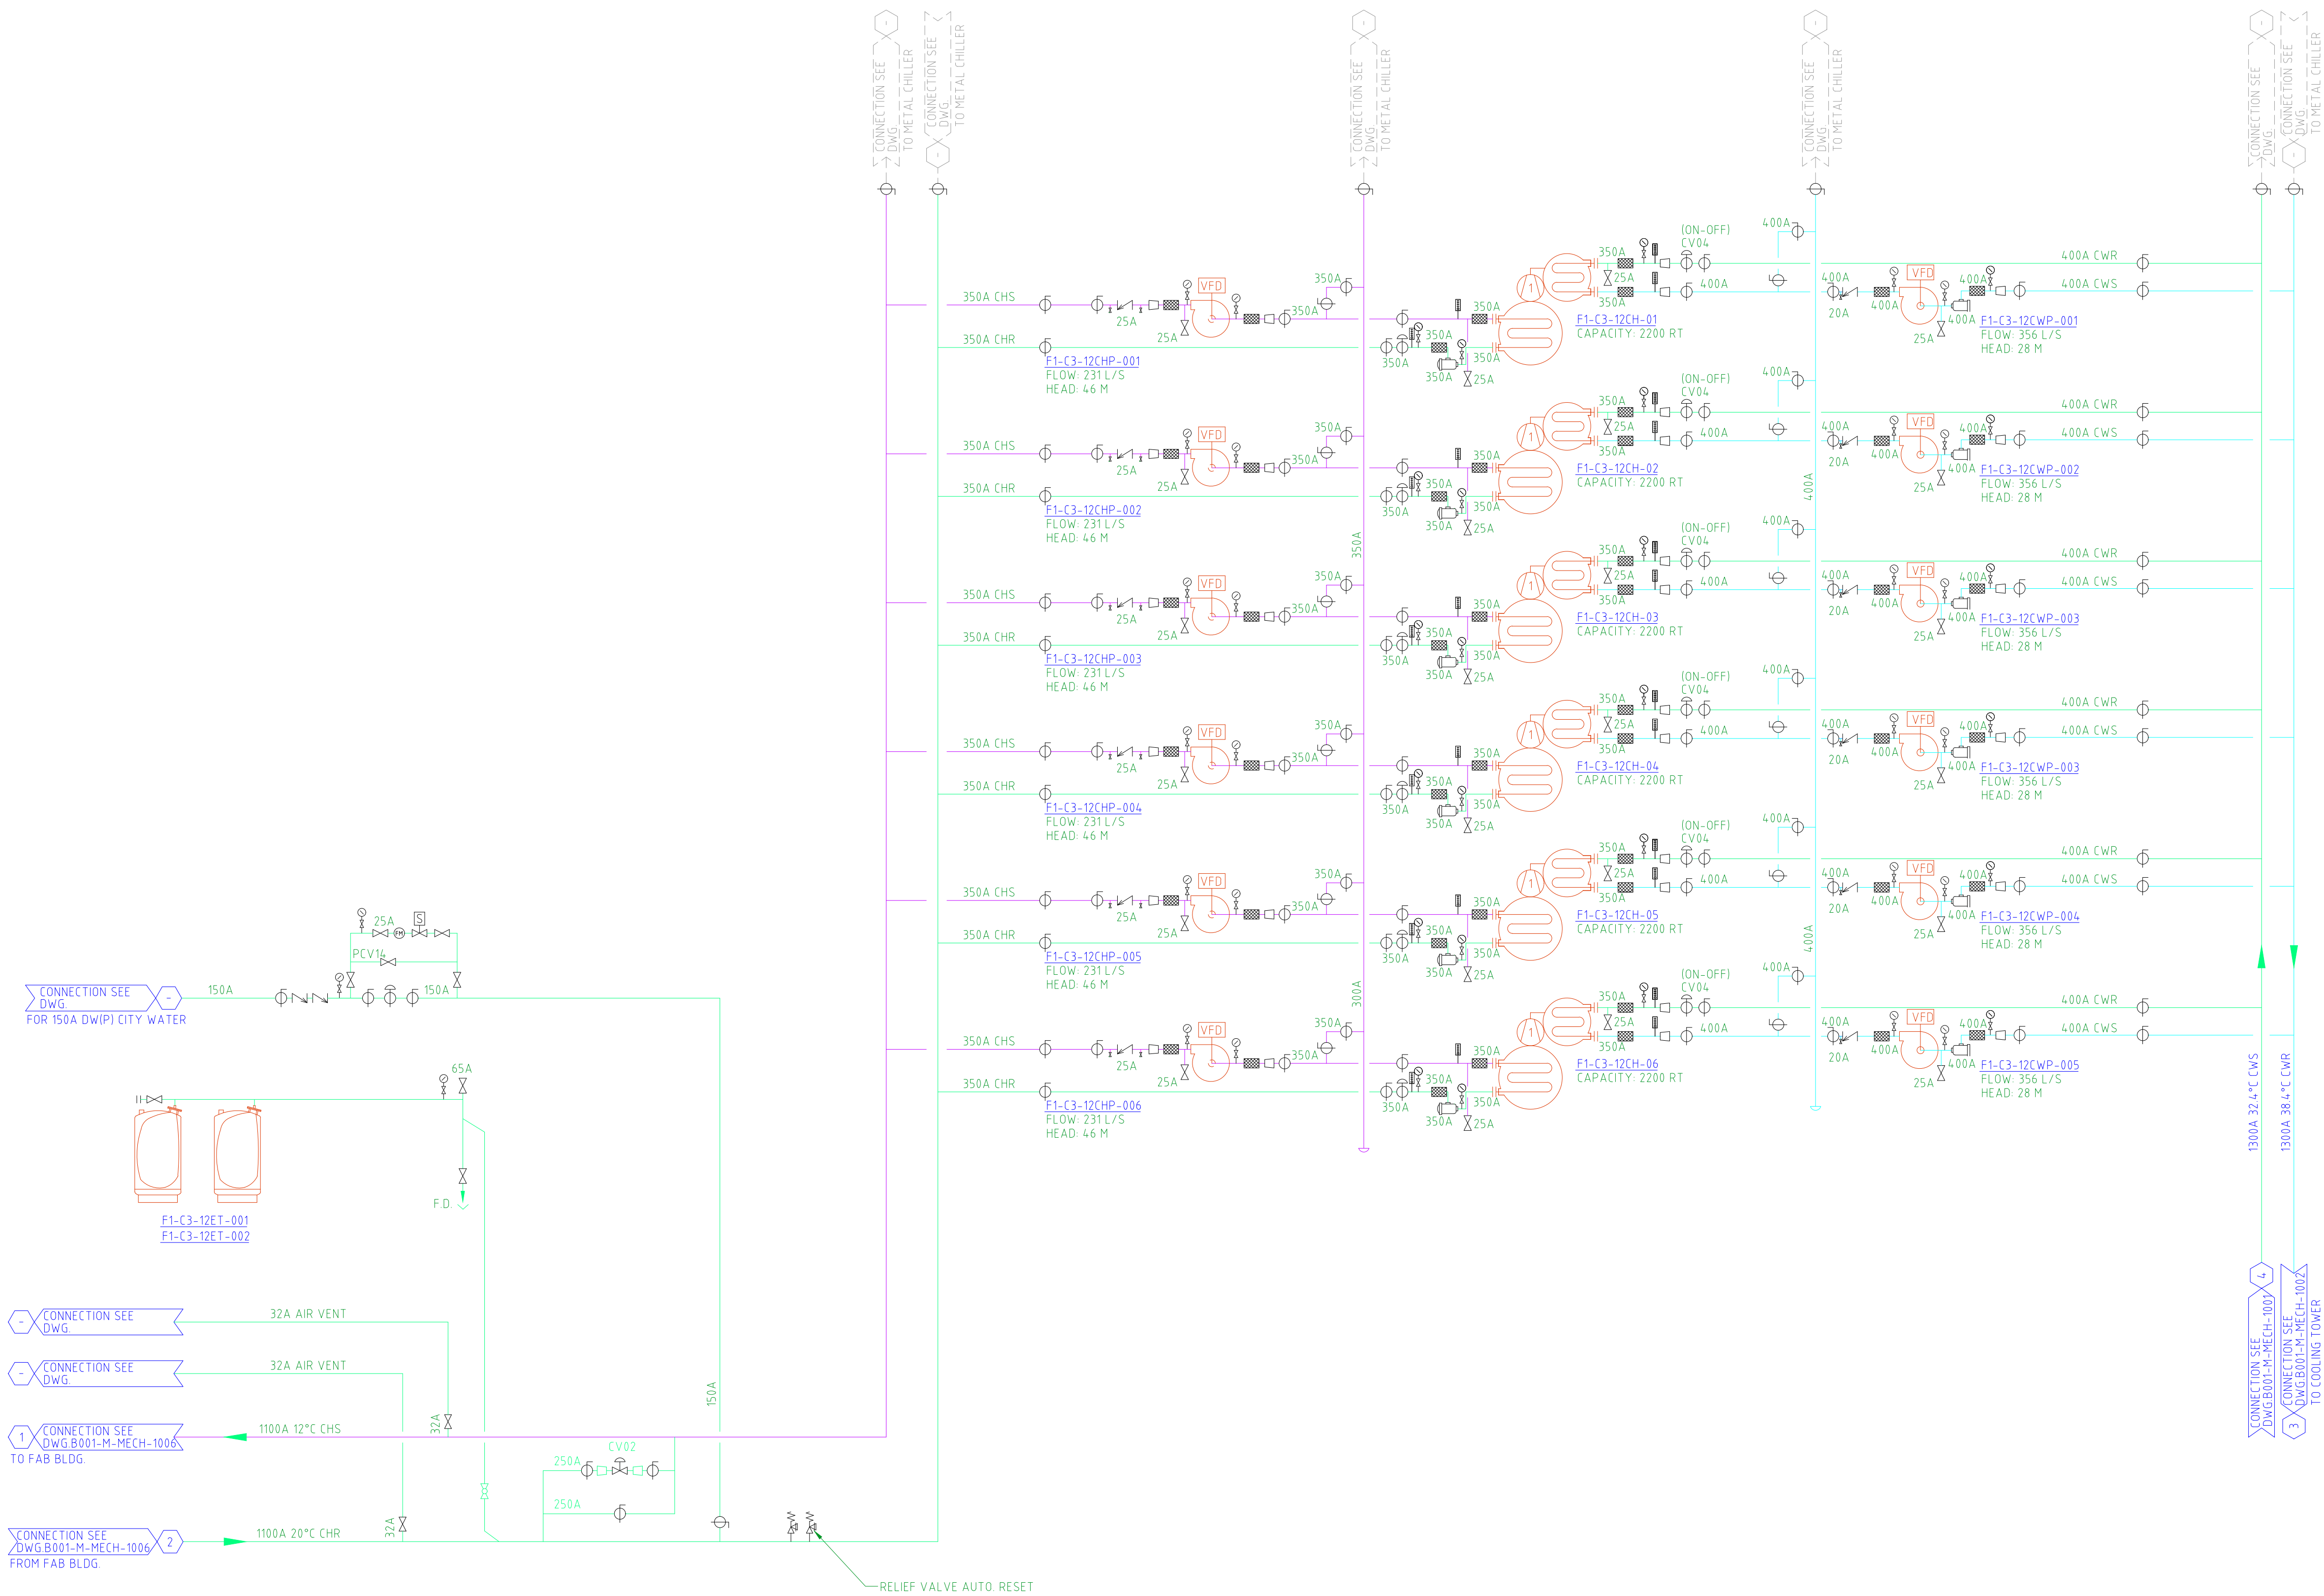

OWNER / DEVELOPER

ARCHITECTURAL CONSULTANT

潘冀聯合建築師

CIVIL & STRUCTURAL CONSULTANT

TEAM 群策工程股份有限公司

MECHANICAL & ELECTRICAL CONSULTANT & CONTRACTOR

漢唐集成股份有限公司

SUB-CONTRACTOR

PROJECT ADDRESS

KEY PLAN

PROJECT TITLE

Micron Falcon A Project (200K)

PROJECT PHASE

Concept Design

DRAWING TITLE

FLOW DIAGRAM-
12°C/20°C CHILLED & CONDENSER
WATER SYSTEM

DESIGNED : -

DRAWN : -

CHECKED : -

DATE : 2024/11/20

JOB NO. :

SCALE :

DRAWING NO.

DE_F1_ALL_B001_M_MECH_1001-00

REV

0

SHEET:

SIZE

A1