


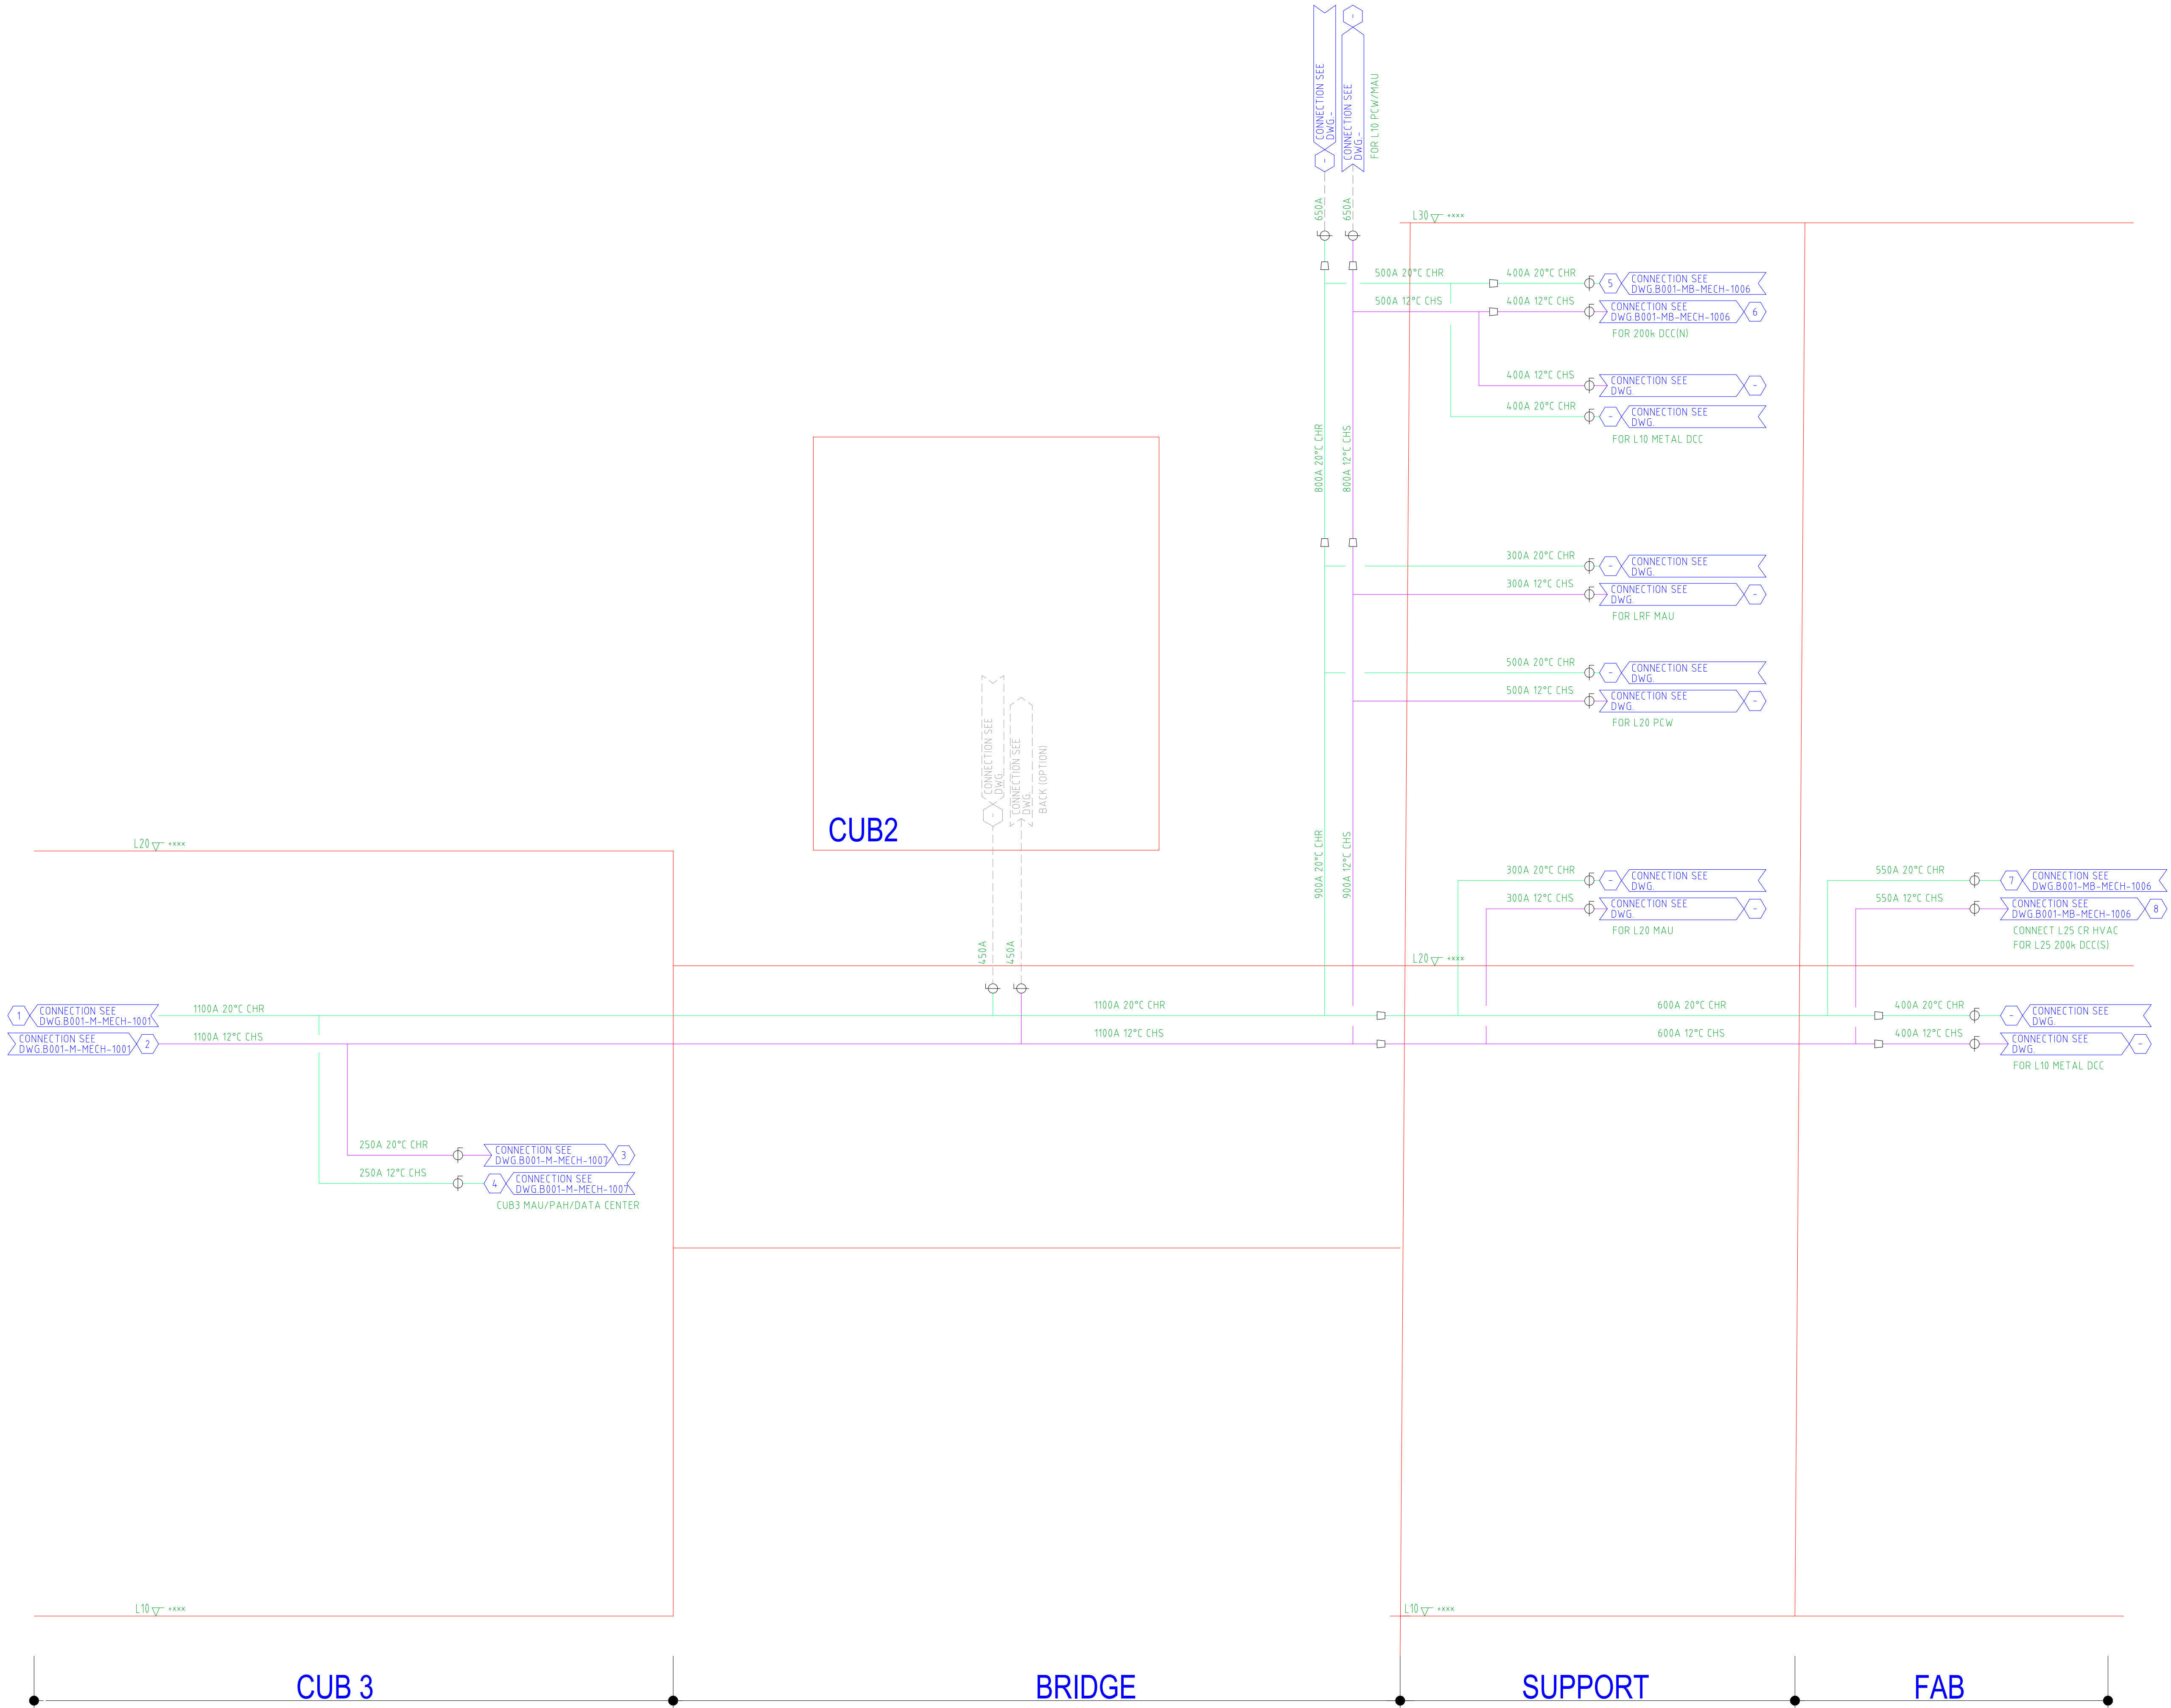

OWNER / DEVELOPER



ARCHITECTURAL CONSULTANT



CIVIL & STRUCTURAL CONSULTANT



MECHANICAL & ELECTRICAL CONSULTANT & CONTRACTOR



SUB-CONTRACTOR

PROJECT ADDRESS

KEY PLAN

1	2025/01/09	REVIEW Drawing	
0	2024/11/20	REVIEW Drawing	
REV	DATE	DESCRIPTION	ISSUED BY
		Revisions	

PROJECT TITLE
Micron Falcon A Project

PROJECT PHASE
Construction

DRAWING TITLE
FLOW DIADRAM-PIPING SYSTEM-1

DESIGNED : JACK CHANG | DRAWN : JACK CHANG | CHECKED : C.S.HU

DATE : 2025/01/09 | JOB NO. : | SCALE : N.T.S

DRAWING NO.
DE_F1_ALL_B001_M_MECH_1005-00

REV
1

SHEET:
A1

SIZE
A1