


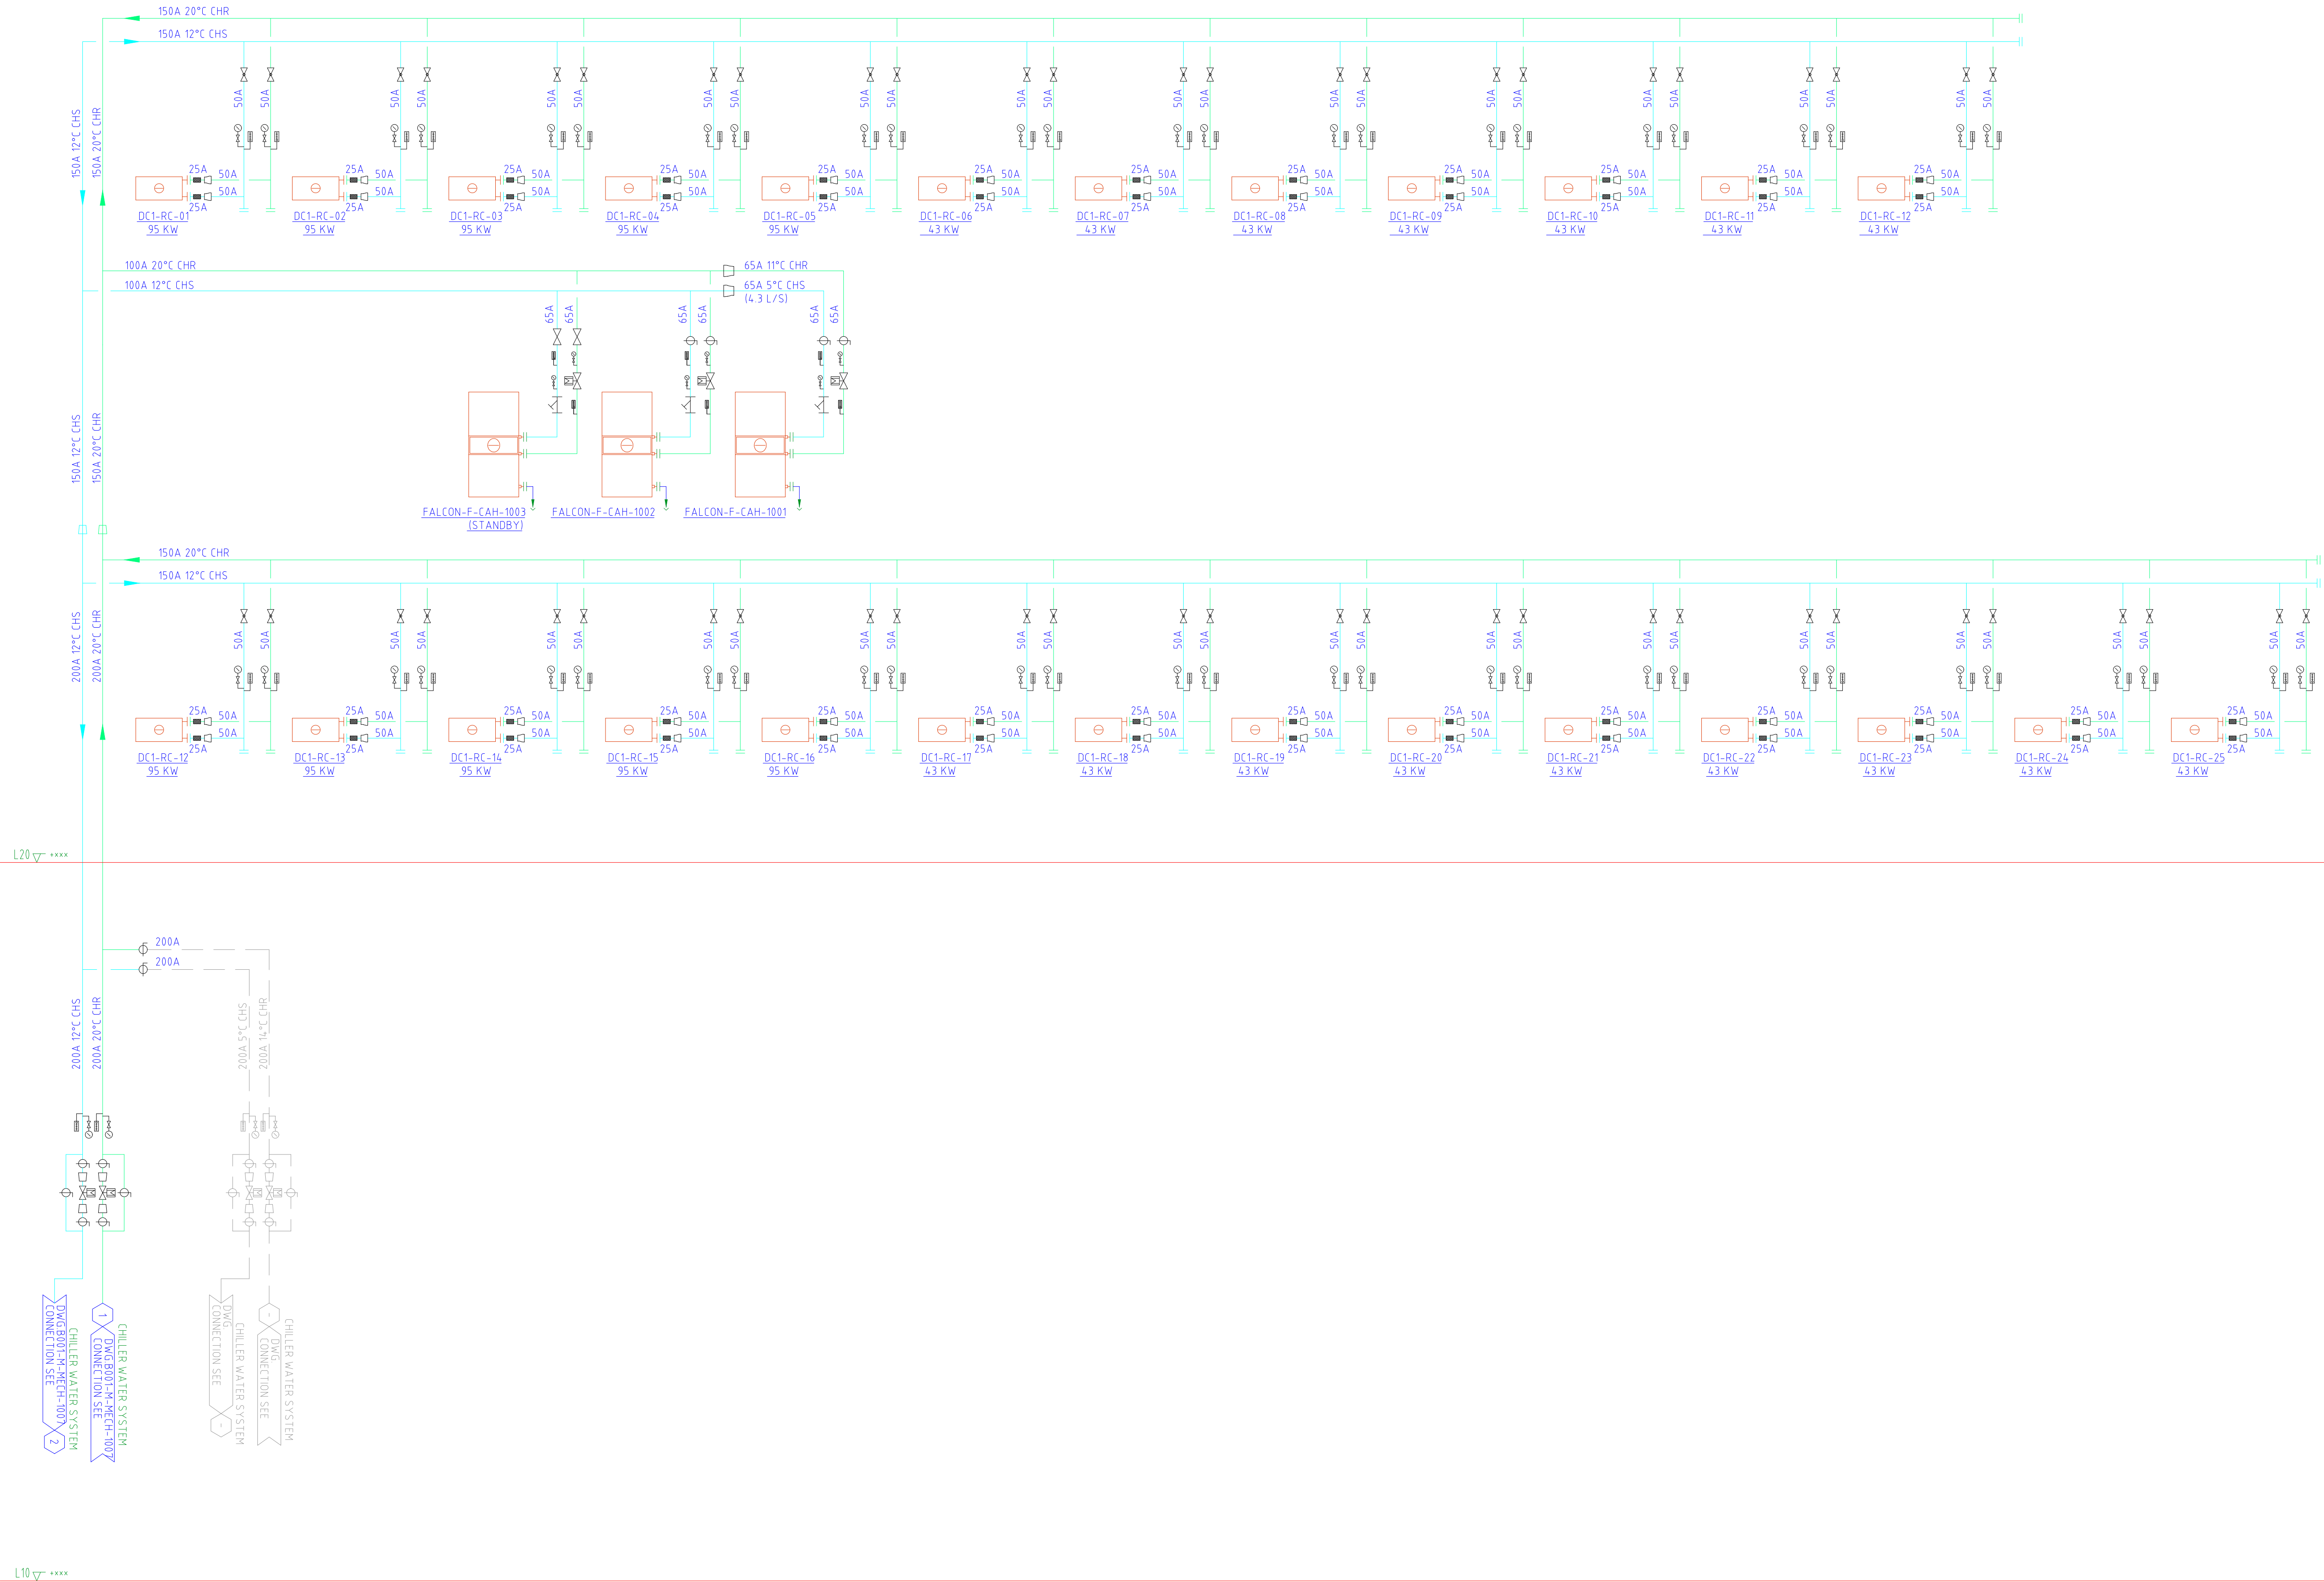

CUB3 DATA CENTER

OWNER / DEVELOPER

ARCHITECTURAL CONSULTANT

潘冀聯合建築師

CIVIL & STRUCTURAL CONSULTANT

群策工程股份有限公司

MECHANICAL & ELECTRICAL CONSULTANT & CONTRACTOR

漢唐集成股份有限公司

SUB-CONTRACTOR

PROJECT ADDRESS

KEY PLAN

PROJECT TITLE

Micron Falcon A Project (200K)

PROJECT PHASE

Concept Design

DRAWING TITLE

FLOW DIADRAM-PIPING SYSTEM-3

DESIGNED : JACK CHANG

DRAWN : JACK CHANG

CHECKED : C.S.HU

DATE : 2024/11/20

JOB NO. :

SCALE : N.T.S

DRAWING NO.

DE_F1_ALL_B001_M_MECH_1007-00

REV

0

SHEET:

SIZE

A1