


L20

L10

CUB3 DATA CENTER

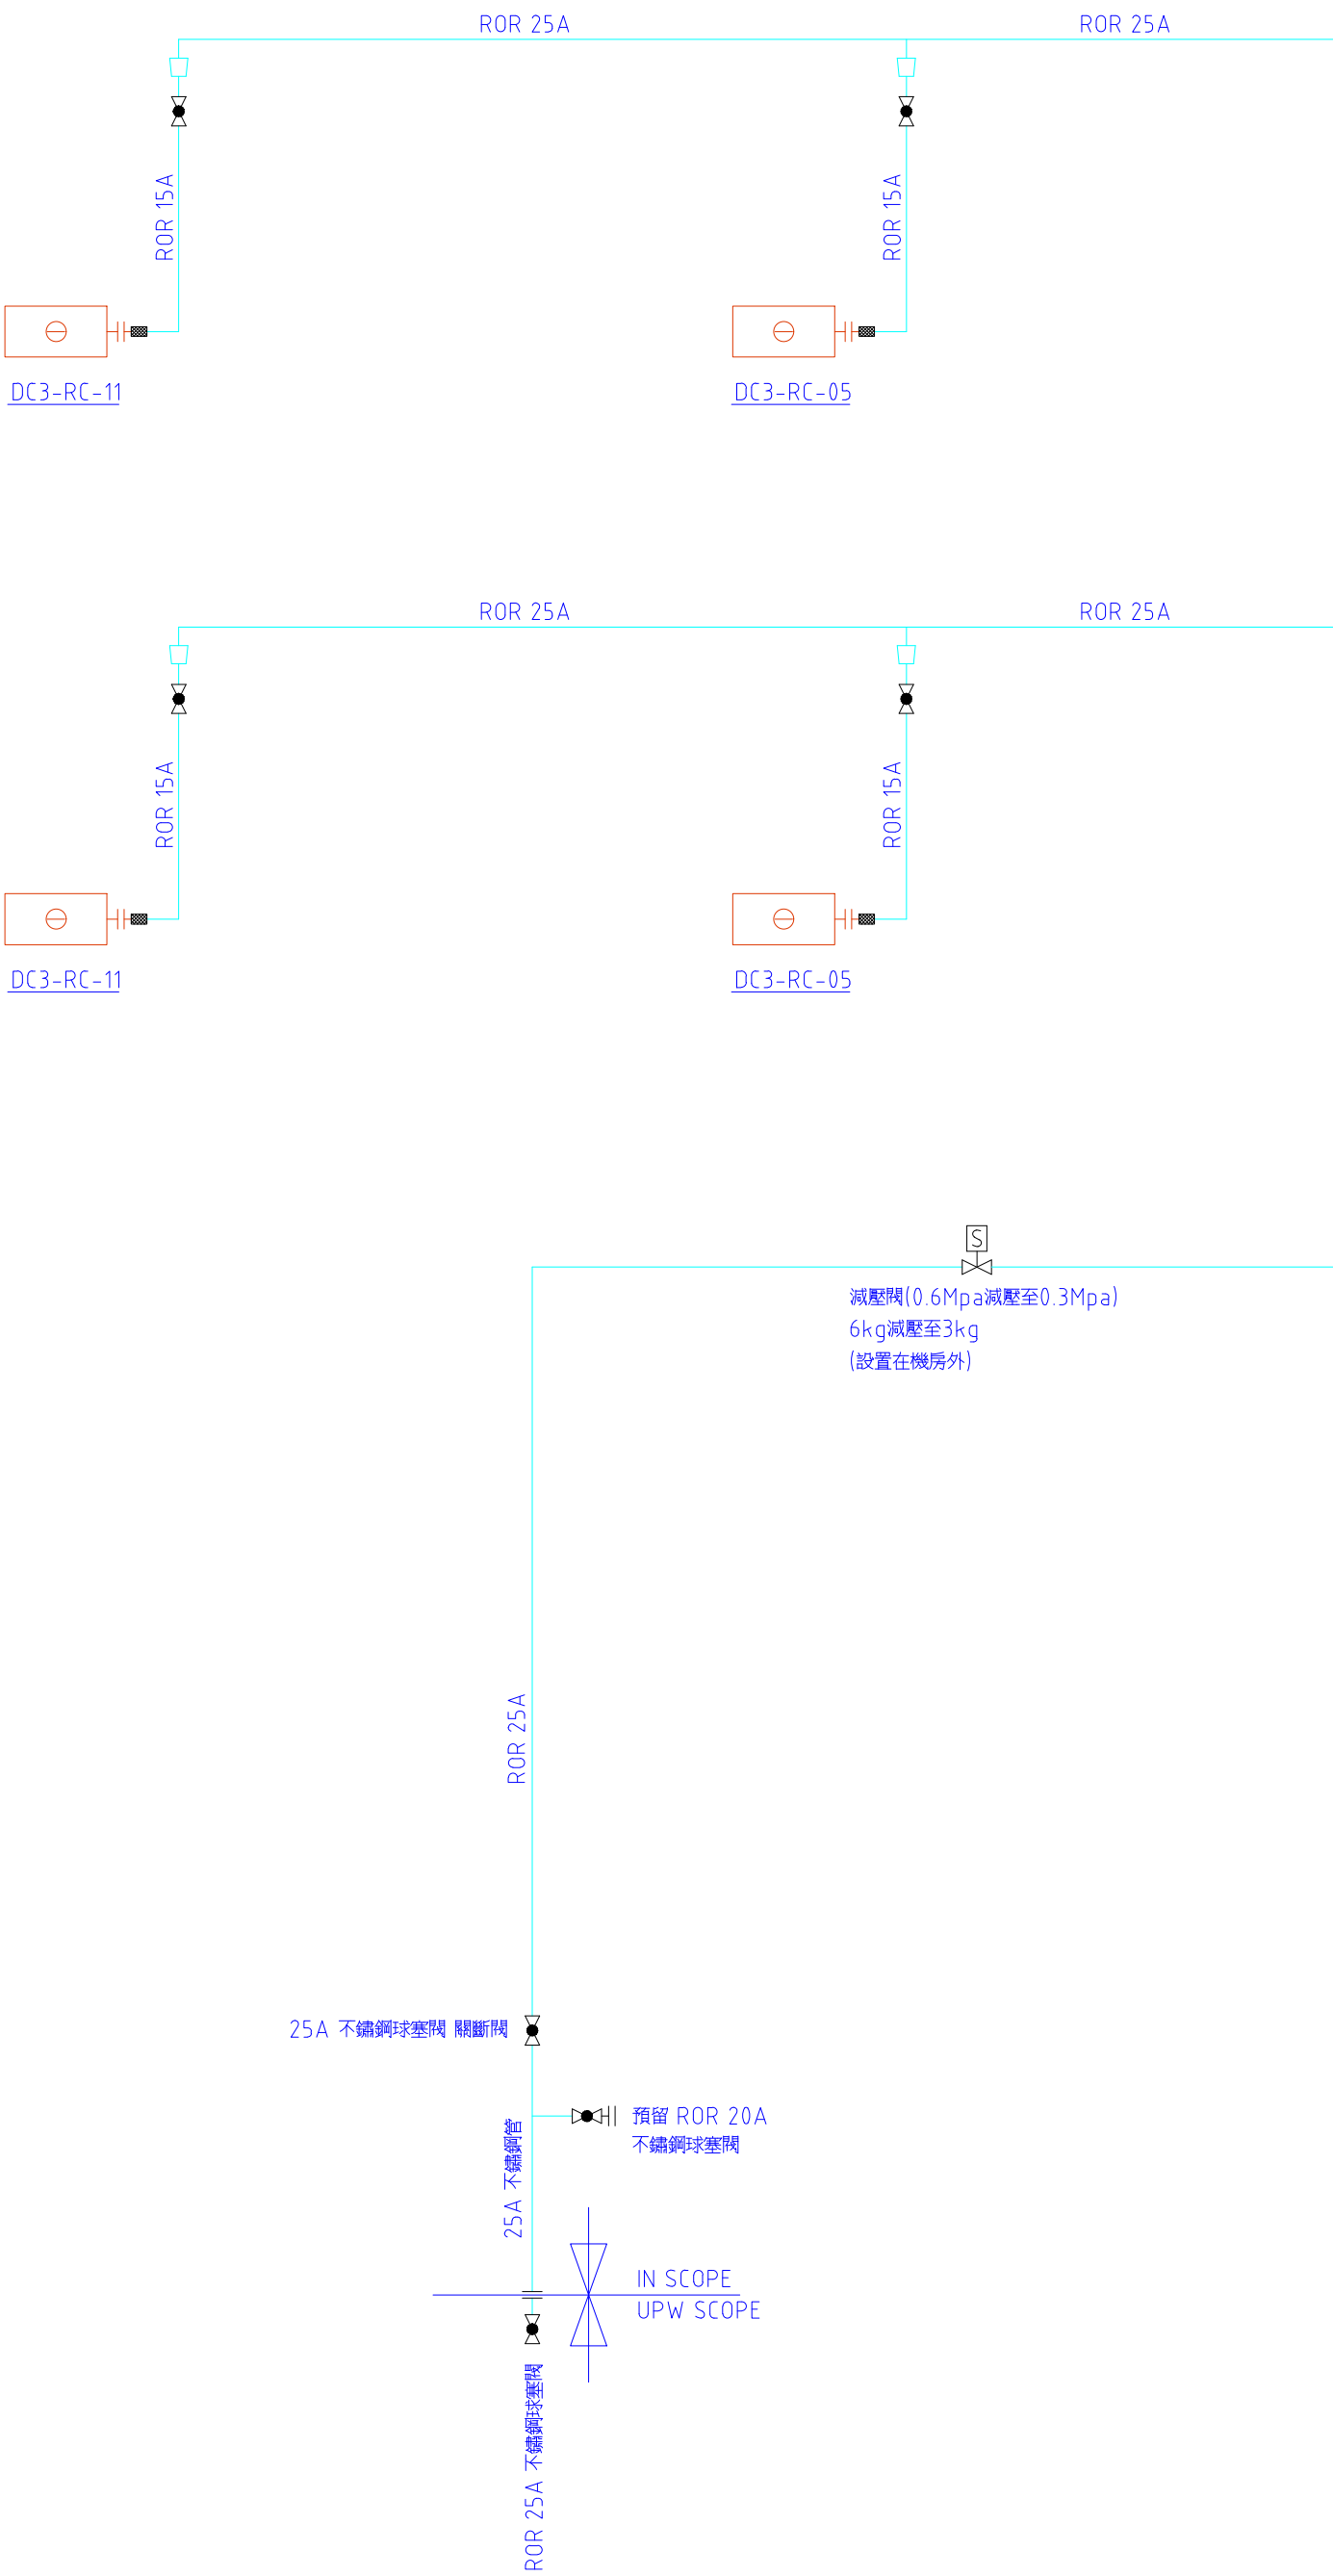

OWNER / DEVELOPER			
micron®			
ARCHITECTURAL CONSULTANT			
JJP ARCHITECTS & PLANNERS 潘冀聯合建築師			
CIVIL & STRUCTURAL CONSULTANT			
TEAM 群策工程股份有限公司			
MECHANICAL & ELECTRICAL CONSULTANT & CONTRACTOR			
uis 漢唐集成股份有限公司			
SUB-CONTRACTOR			
PROJECT ADDRESS			
KEY PLAN			
PROJECT TITLE			
Micron Falcon A Project (200K)			
PROJECT PHASE			
Concept Design			
DRAWING TITLE			
FLOW DIADRAM-PIPING SYSTEM-4			
DESIGNED : JACK CHANG DRAWN : JACK CHANG CHECKED : C.S.HU			
DATE : 2024/11/20 JOB NO. : SCALE : N.T.S			
DRAWING NO. DE_F1_ALL_B001_M_MECH_1008-00			
SHEET: 0			
SIZE A1			