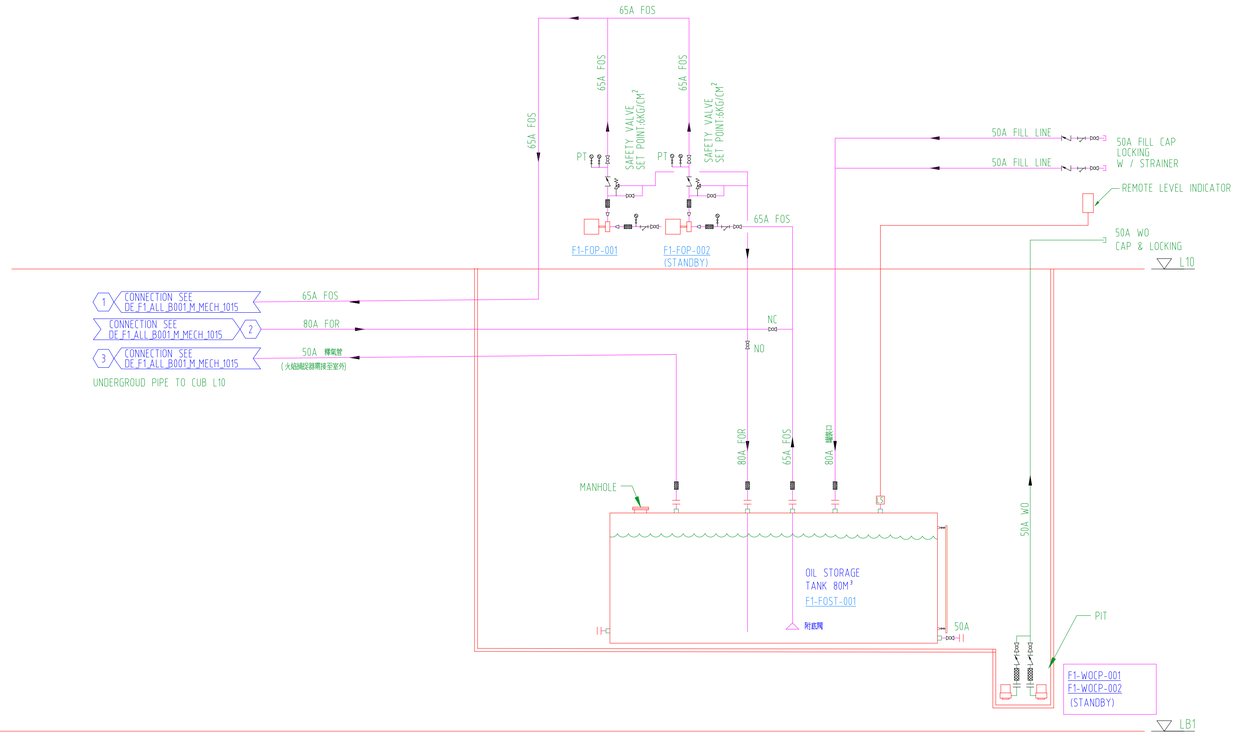


柴油儲存槽配管流程圖

OWNER / DEVELOPER

micron

ARCHITECTURAL CONSULTANT

JJP ARCHITECTS & PLANNERS 潘冀聯合建築師

CIVIL & STRUCTURAL CONSULTANT

TEAM 群策工程股份有限公司

MECHANICAL & ELECTRICAL CONSULTANT & CONTRACTOR

UIS United Integrated Services 漢唐集成股份有限公司

SUB-CONTRACTOR

PROJECT ADDRESS

KEY PLAN

REV	DATE	DESCRIPTION	ISSUED BY
A	2025/01/02	REVIEW Drawing	

Revisions

PROJECT TITLE

Micron Falcon A Project (200K)

PROJECT PHASE

Concept Design

DRAWING TITLE

FLOW DIAGRAM-
DIESEL FUEL SYSTEM(1)
-

DESIGNED : JACK	DRAWN : JACK	CHECKED : C.S.HU	
DATE : 2024/11/20	JOB NO. :	SCALE : N.T.S.	

DRAWING NO. DE_F1_ALL_B001_M_MECH_1010-00

REV 0

SHEET:

SIZE A1