


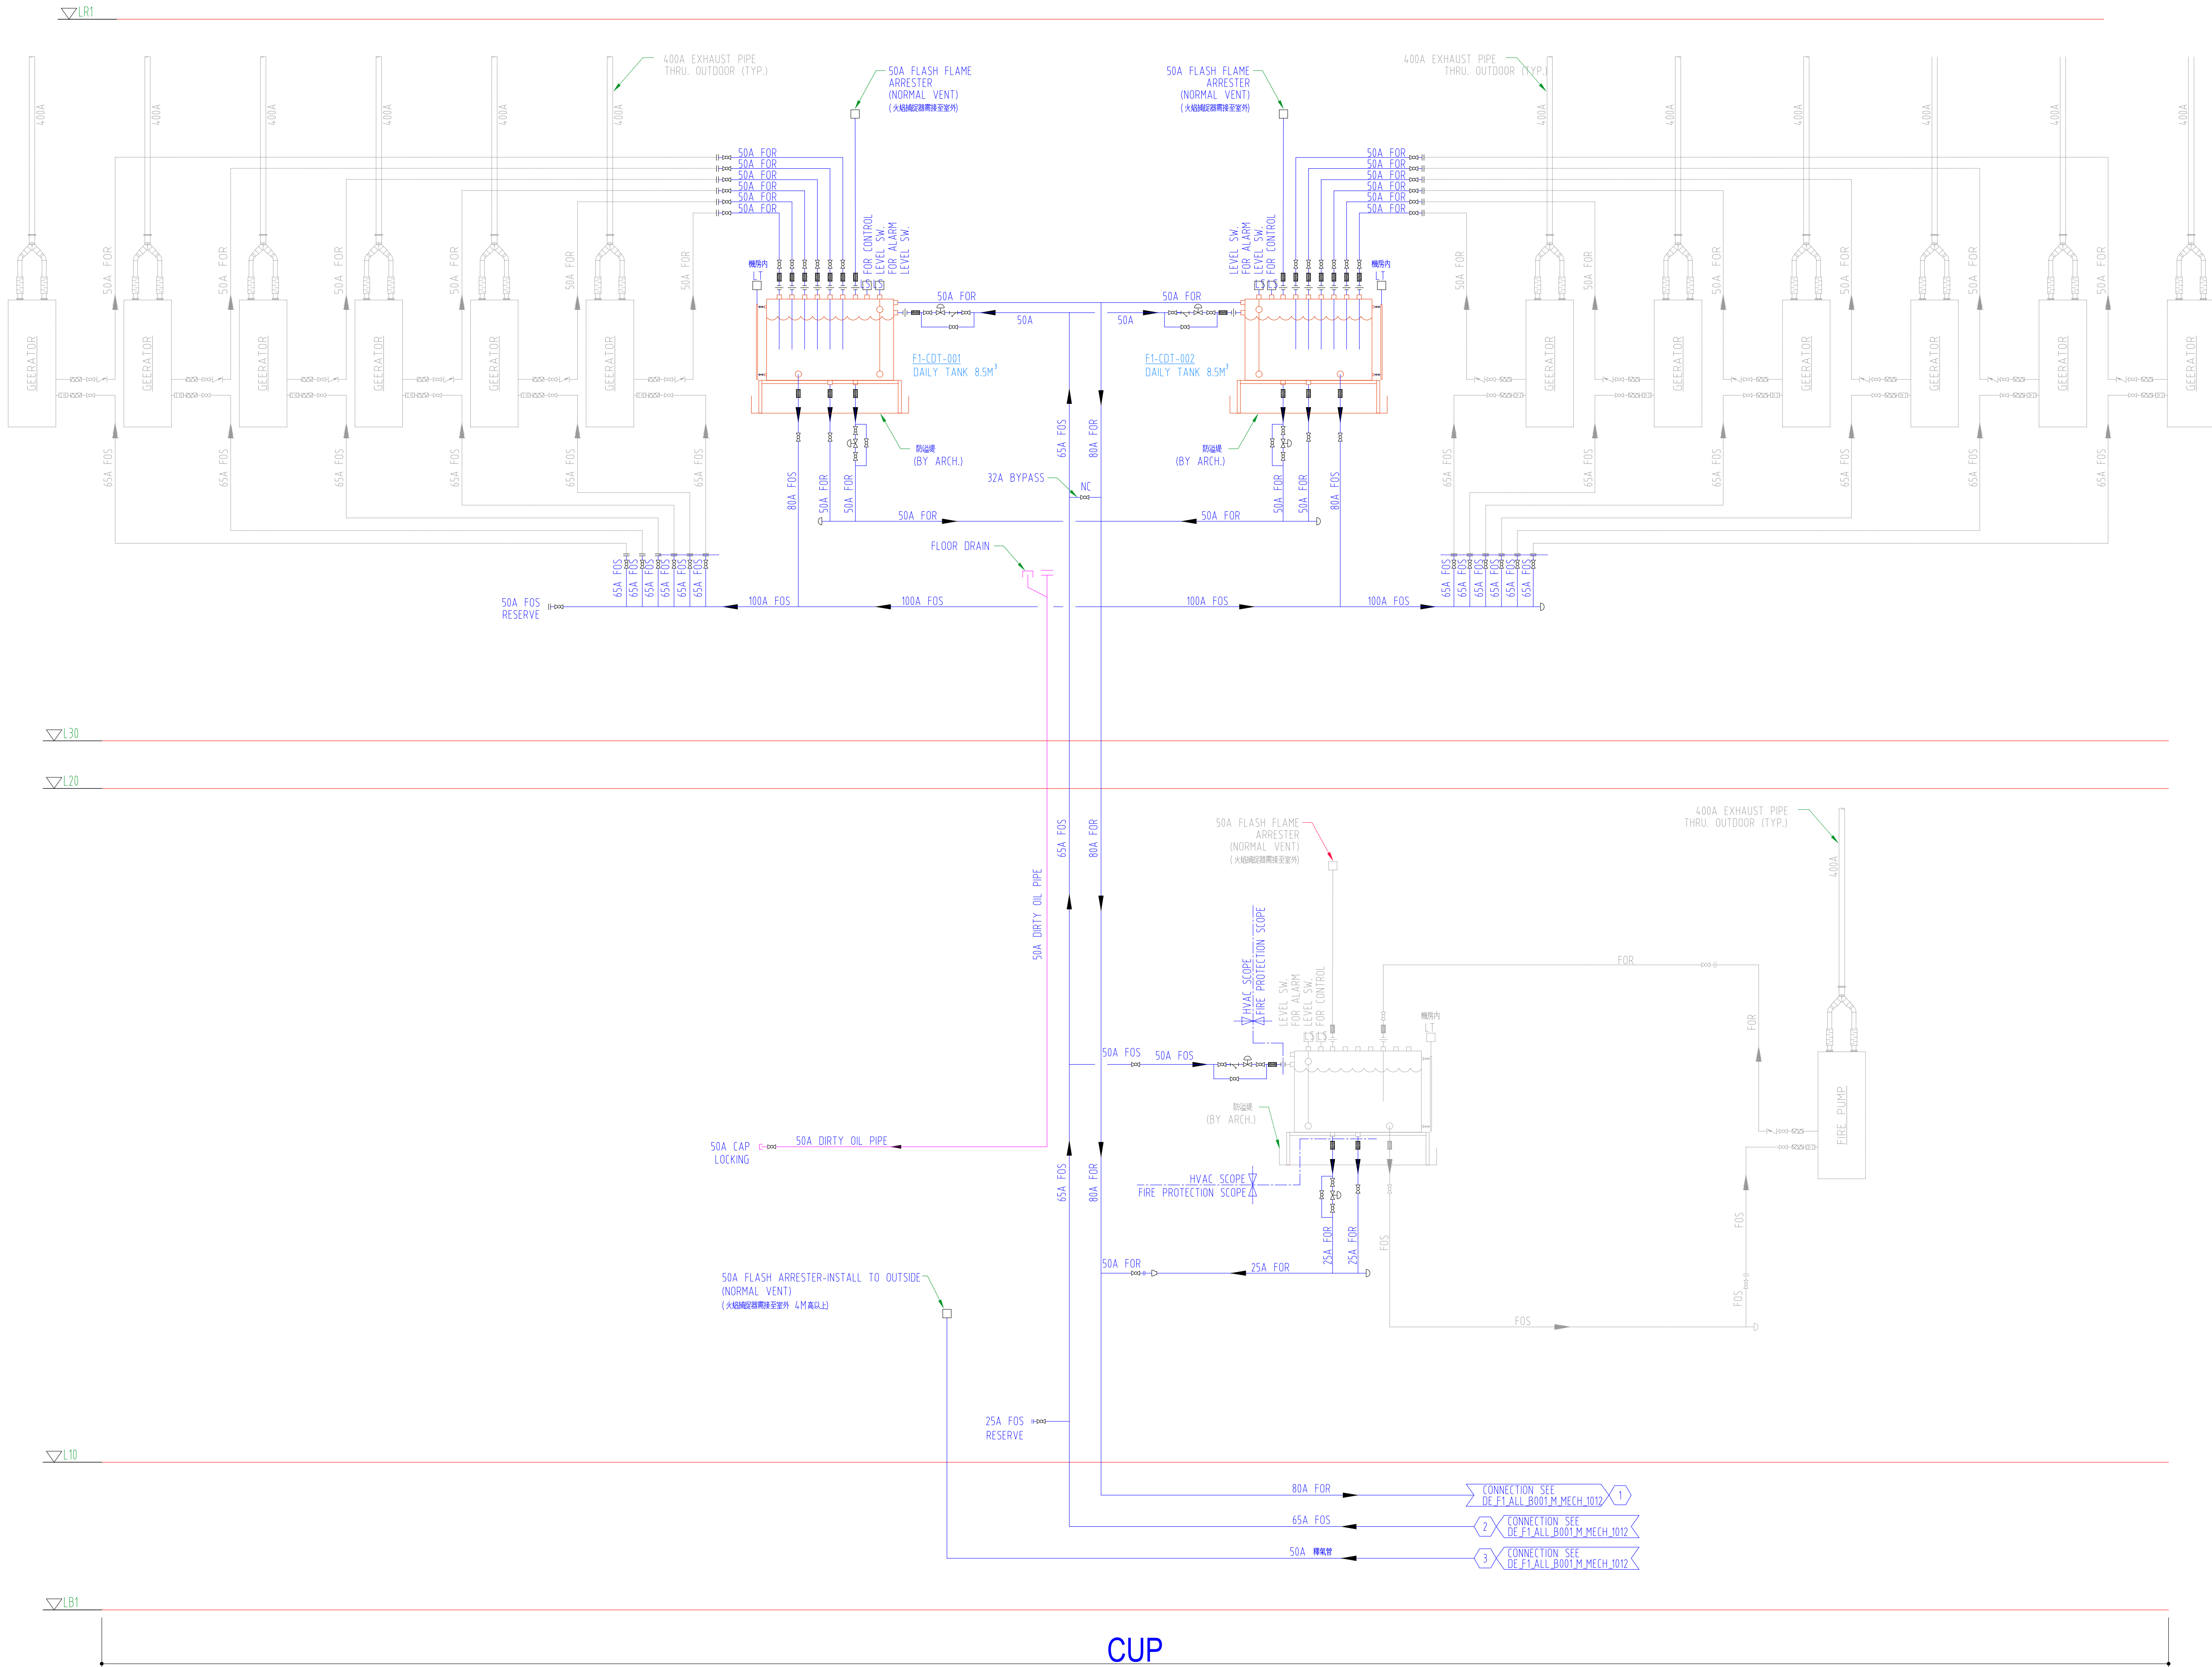

OWNER / DEVELOPER

micron

ARCHITECTURAL CONSULTANT

JJP

ARCHITECTS & PLANNERS

潘冀聯合建築師

CIVIL & STRUCTURAL CONSULTANT

TEAM

群策工程股份有限公司

MECHANICAL & ELECTRICAL CONSULTANT & CONTRACTOR

uis

United Integrated Services

漢唐集成股份有限公司

SUB-CONTRACTOR

PROJECT ADDRESS

KEY PLAN

PROJECT TITLE

Micron Falcon A Project (200K)

PROJECT PHASE

Concept Design

DRAWING TITLE

FLOW DIAGRAM- DIESEL FUEL SYSTEM(2)

DESIGNED :	JACK	DRAWN :	JACK	CHECKED :	C.S.HU
DATE :	2024/11/20	JOB NO. :		SCALE :	N.T.S.
DRAWING NO.	DE_F1_ALL_B001_M_MECH_1011-00				REV
					0
	SHEET:				SIZE A1