


L40

L30

L25

L20

L05

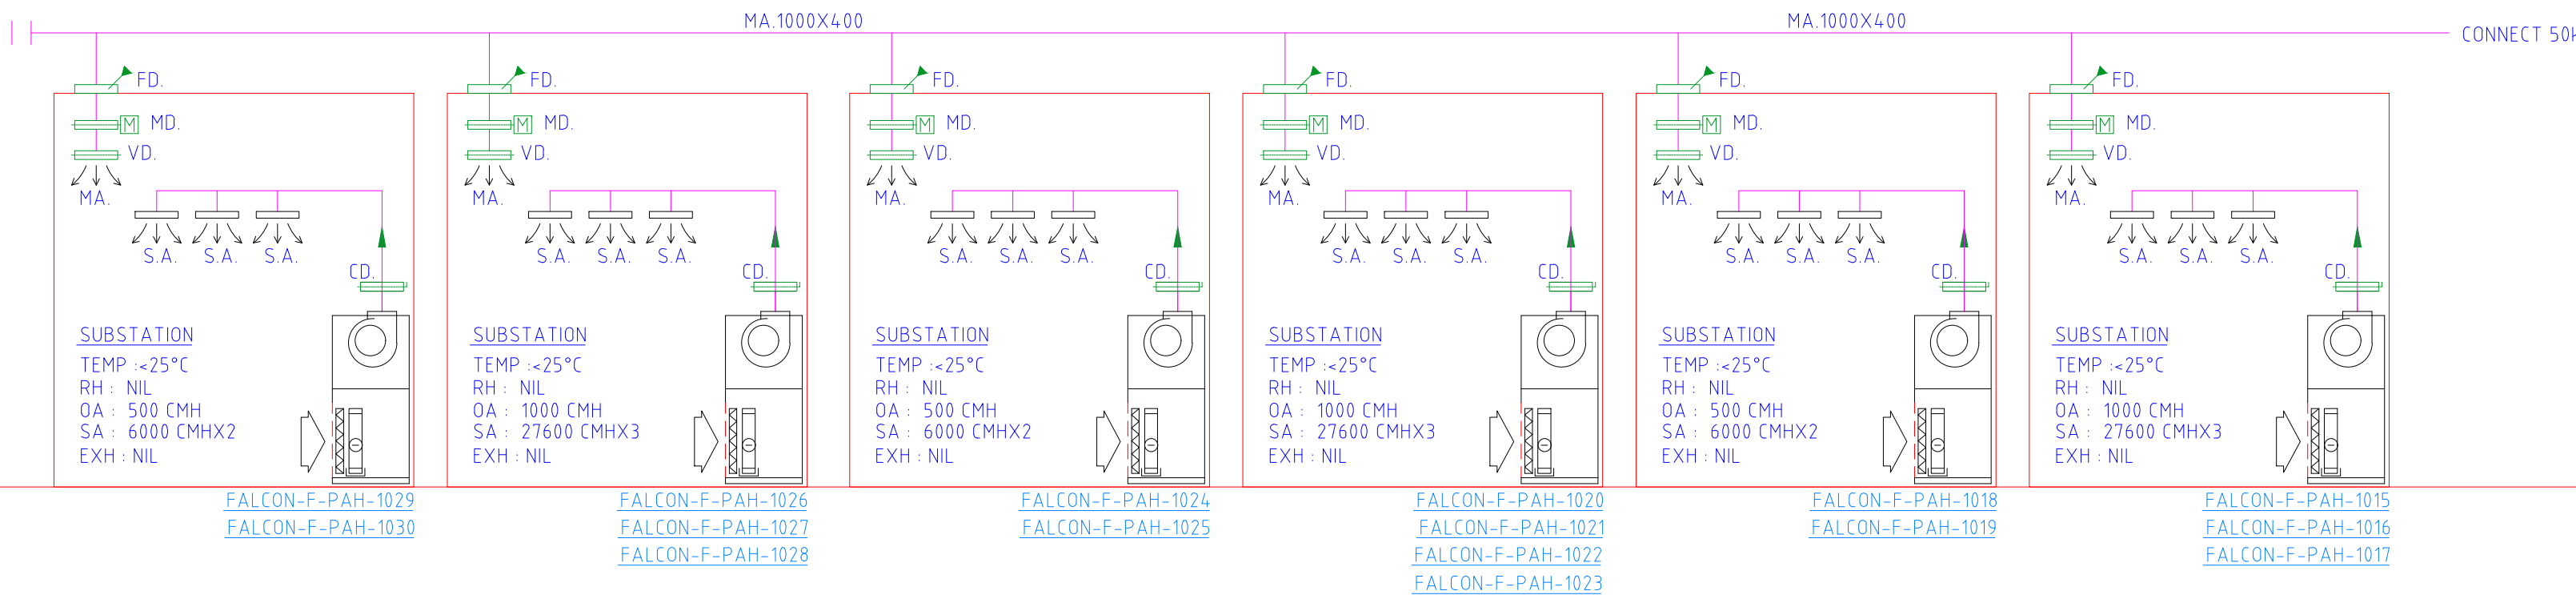

FAB

OWNER / DEVELOPER			
micron®			
ARCHITECTURAL CONSULTANT			
JJP ARCHITECTS & PLANNERS 潘冀聯合建築師			
CIVIL & STRUCTURAL CONSULTANT			
TEAM 群策工程股份有限公司			
MECHANICAL & ELECTRICAL CONSULTANT & CONTRACTOR			
uis 漢唐集成股份有限公司			
SUB-CONTRACTOR			
PROJECT ADDRESS			
KEY PLAN			
PROJECT TITLE			
Micron Falcon A Project			
PROJECT PHASE			
Construction			
DRAWING TITLE			
FLOW DIADRAM-FAB DUCTING SYSTEM			
(1)			
-			
-			
DESIGNED : JACK CHANG			
DRAWN : JACK CHANG			
CHECKED : C.S.HU			
DATE : 2025/01/09			
JOB NO. :			
SCALE : N.T.S			
DRAWING NO.			
DE_F1_ALL_B001_M_MECH_1015-00			
REV			
1			
SHEET:			
SIZE A1			