L20 ▽ ××××

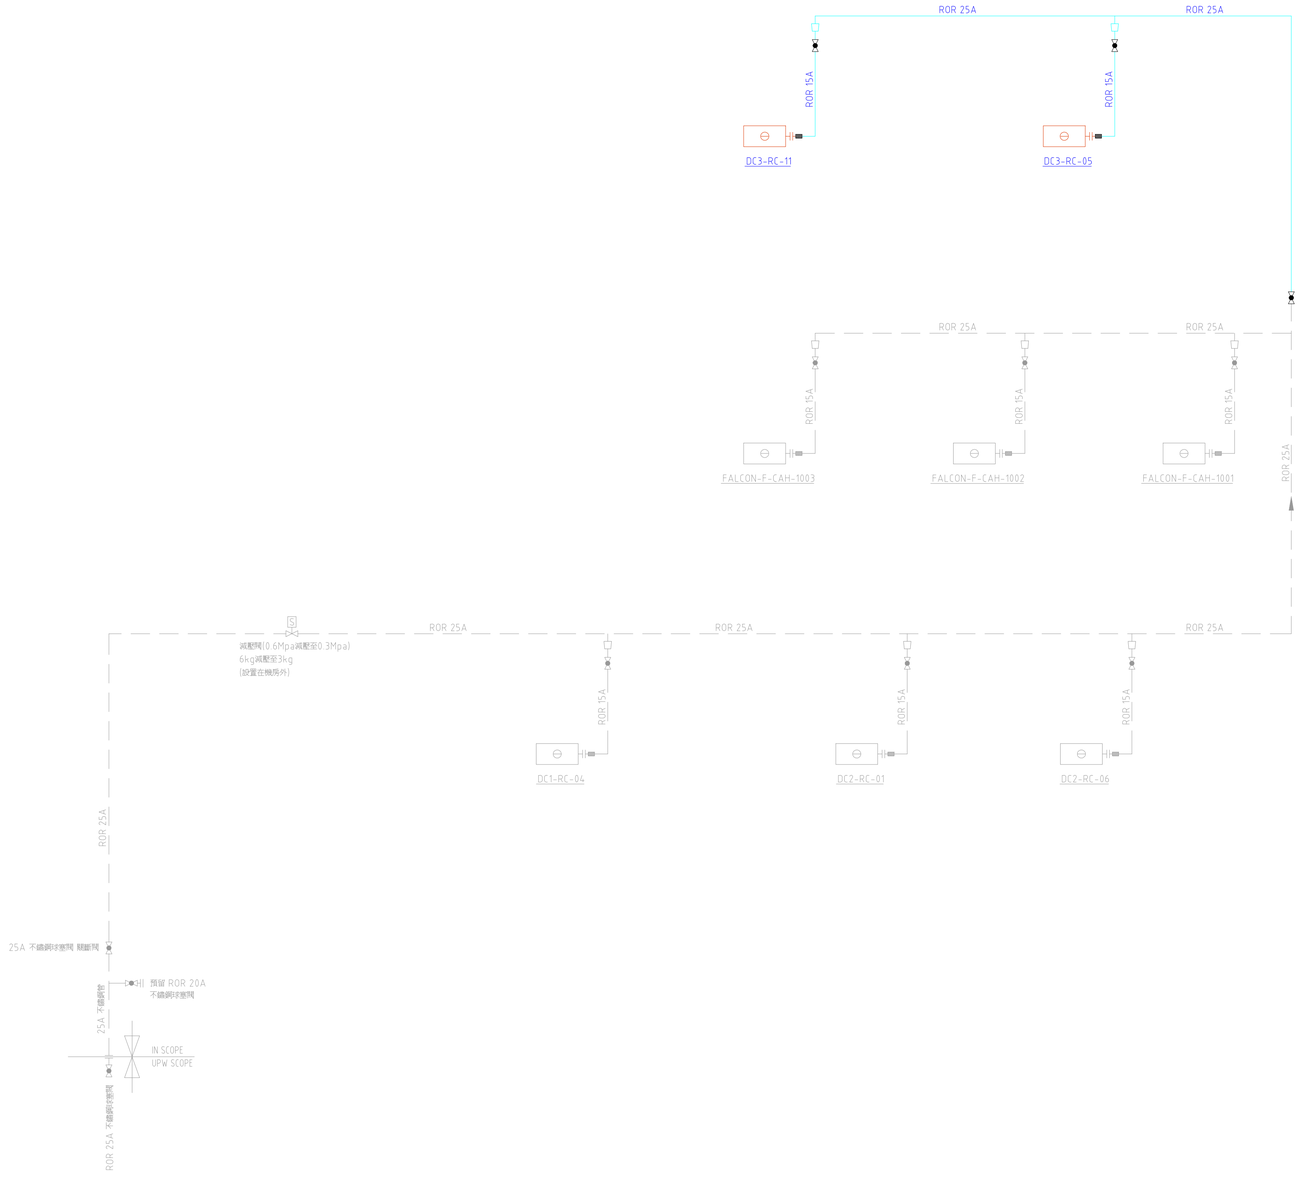

L10 ▽ ××××

DATA CENTER

OWNER / DEVELOPER

micron

ARCHITECTURAL CONSULTANT

JJP ARCHITECTS & PLANNERS 潘冀聯合建築師

CIVIL & STRUCTURAL CONSULTANT

TEAM 群策工程股份有限公司

MECHANICAL & ELECTRICAL CONSULTANT & CONTRACTOR

UIS Unified Integrated Services 漢唐集成股份有限公司

SUB-CONTRACTOR

PROJECT ADDRESS

KEY PLAN

REV	DATE	DESCRIPTION	ISSUED BY
A	2025/01/02	REVIEW Drawing	

Revisions

PROJECT TITLE

Micron Falcon A Project (200K)

PROJECT PHASE

Concept Design

DRAWING TITLE

FLOW DIADRAM-FAB(N) PIPING SYSTEM-2

-

-

-

DESIGNED : JACK CHANG	DRAWN : JACK CHANG	CHECKED : C.S.HU	
DATE : 2024/11/20	JOB NO. :	SCALE : N.T.S	

DRAWING NO.

DE_F1_DATA_B001_M_PIPE_1003-DC-00

REV 0

SHEET:

SIZE A1