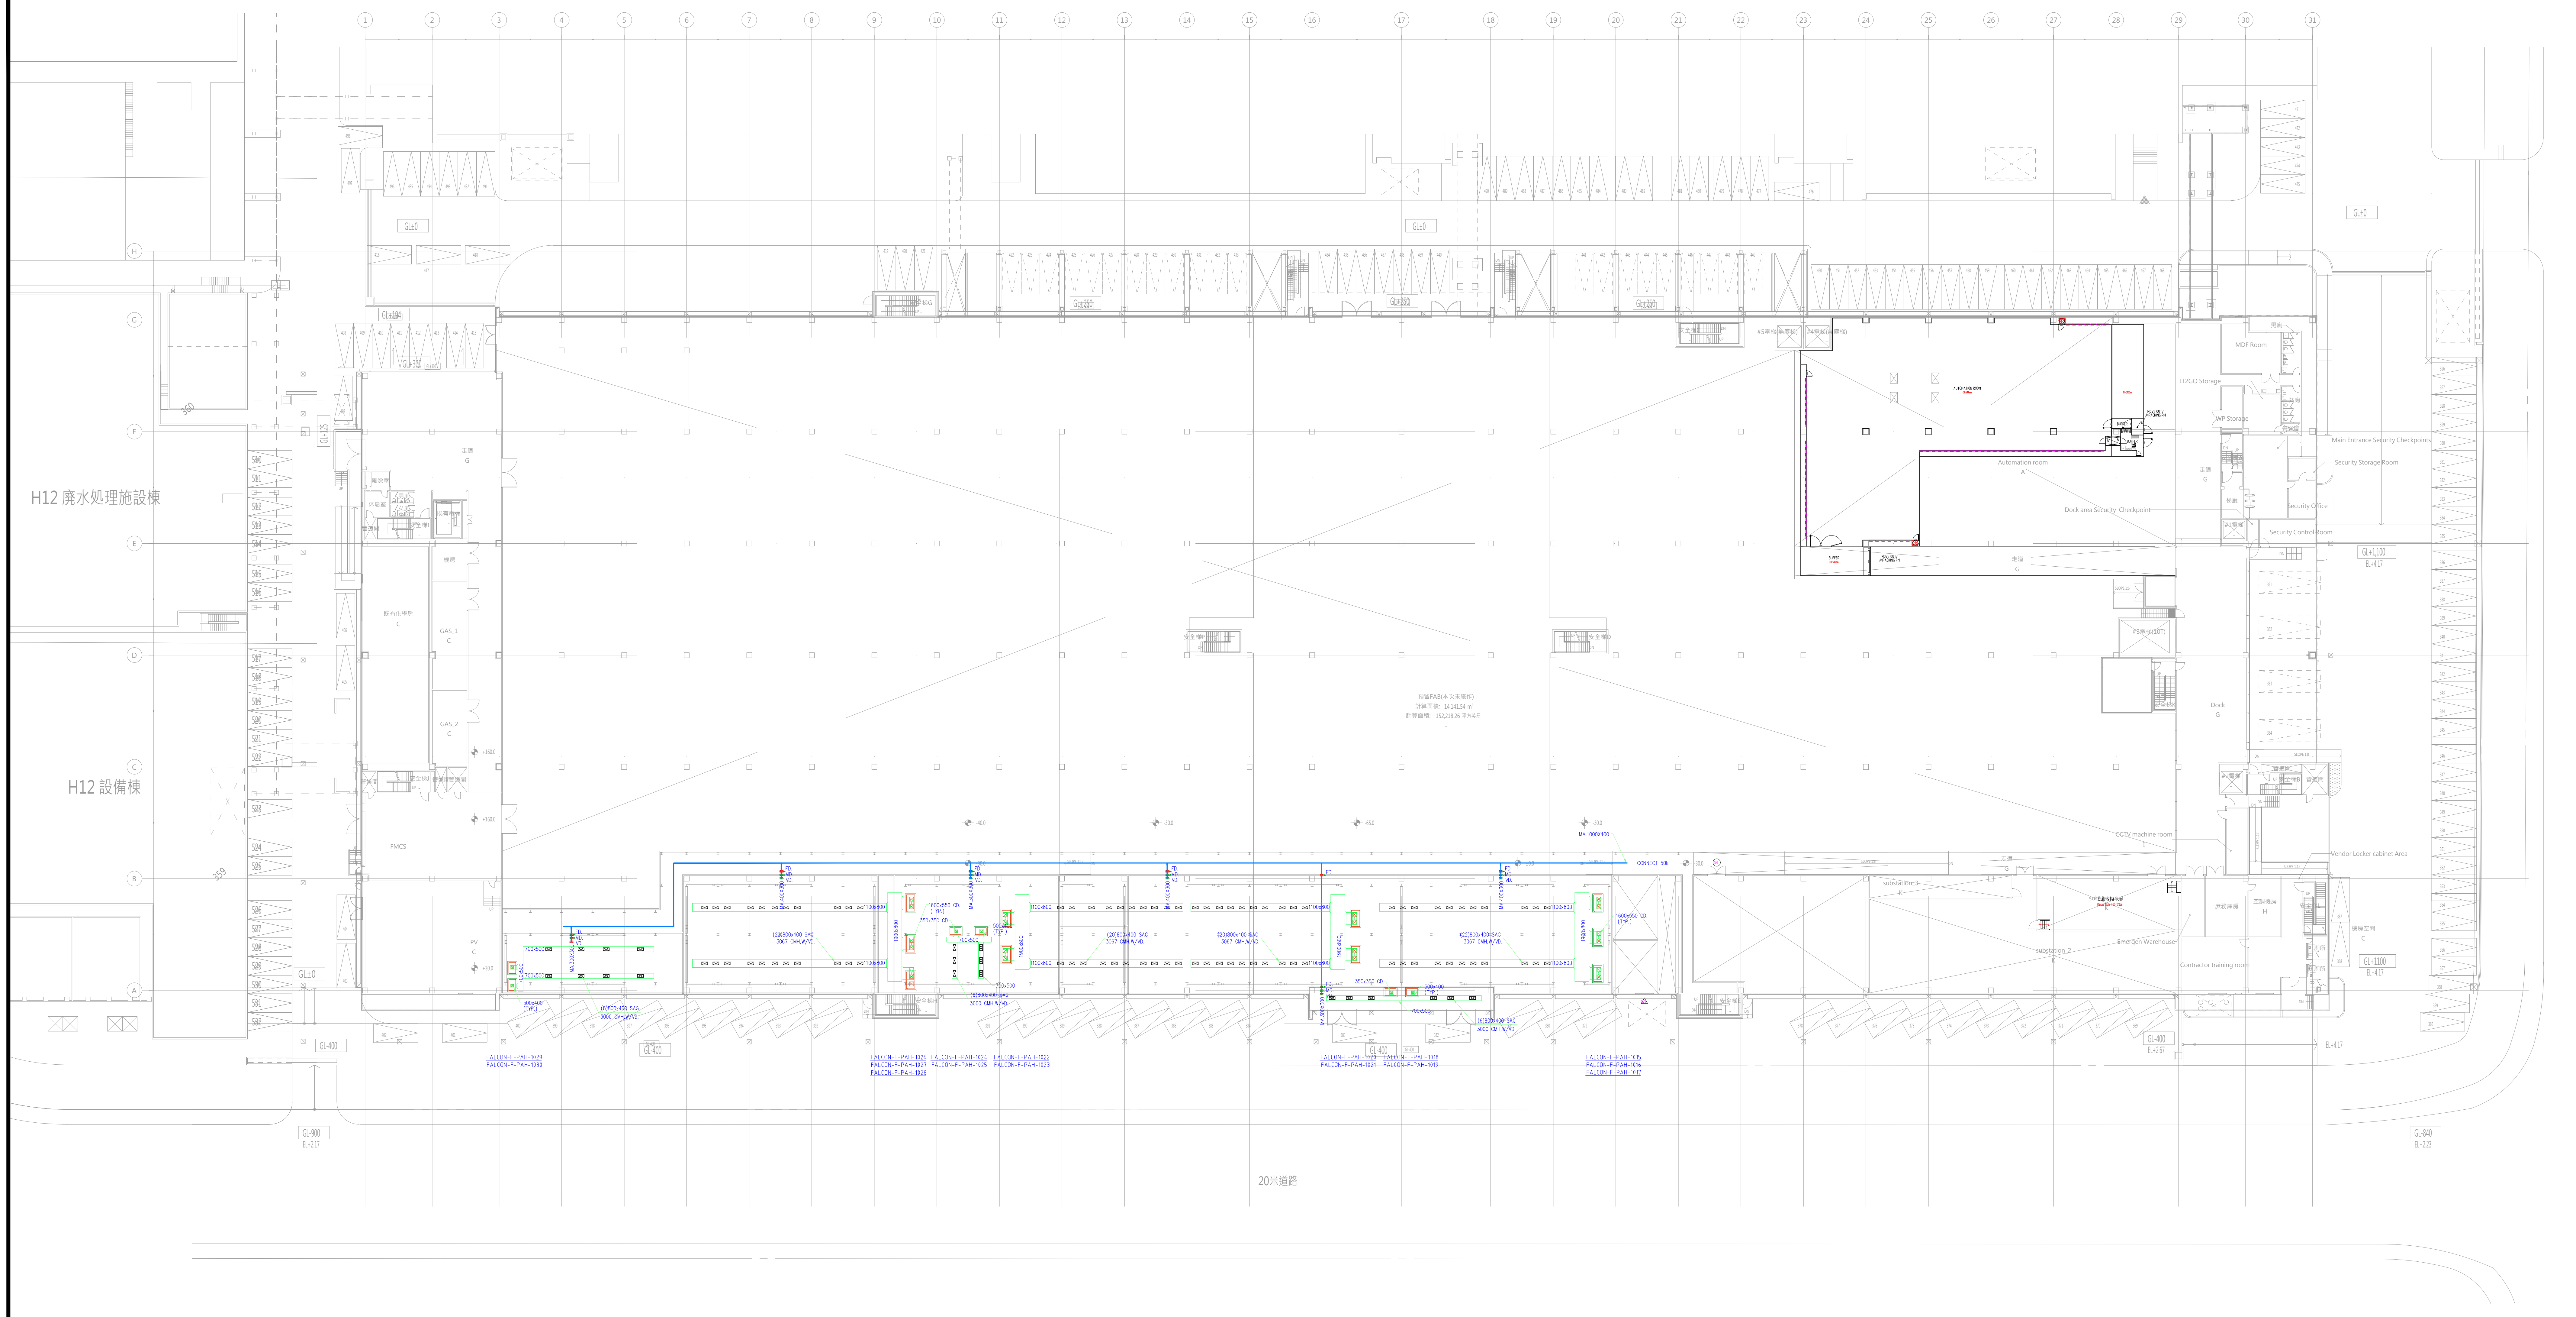

1
2
3
4
5
6
7
8
9
10
11
12
13
14
15
16
17
18
19
20
21
22
23
24
25
26
27
28
29
30
31
H
G
F
E
D
C
B
A
H12 廃水処理施設棟
H12 設備棟
GL±0
GL±184
GL+300
GL+125
GL±250
GL+1,100
EL+4.17
GL+1100
GL-400
EL+2.67
GL-900
EL+2.17
GL-840
EL+2.23
EL+4.17
走道
G
風除室
休息室
男廁
女廁
安全梯I
既有電梯
機房
既有化學房
C
GAS_1
C
GAS_2
C
安全梯J
管道間
FMCS
PV
C
+160.0
+30.0
-40.0
-30.0
-65.0
安全梯F
安全梯D
安全梯C
安全梯E
預留FAB(本次未施作)
計算面積: 14,141.54 m²
計算面積: 152,218.26 平方英尺
#5電梯(無塵梯)
#4電梯(無塵梯)
AUTOMATION ROOM
Automation room
A
Dock area Security Checkpoint
BUFFER
MOVE OUT/ UNPACKING RM
MDF Room
IT2GO Storage
WP Storage
Main Entrance Security Checkpoints
Security Storage Room
Security Office
Security Control Room
梯廳
#1電梯
#3電梯(10T)
安全梯K
Dock
G
#2電梯
安全梯B
CCTV machine room
Vendor Locker cabinet Area
substation_3
K
substation_2
K
Sub station
Emergen Warehouse
Contractor training room
庶務庫房
空調機房
H
機房空間
C
廁所
MA.1000X400
CONNECT 50k
MA.300X300
MA.400X300
FD.
MD.
VD.
1600x550 CD.
(TYP.)
350x350 CD.
500x400
(TYP.)
700x500
1100x800
1900x800
(22)800x400 SAG
3067 CMH,W/VD.
(20)800x400 SAG
3067 CMH,W/VD.
(8)800x400 SAG
3000 CMH,W/VD.
(6)800x400 SAG
3000 CMH,W/VD.
FALCON-F-PAH-1029
FALCON-F-PAH-1030
FALCON-F-PAH-1026
FALCON-F-PAH-1027
FALCON-F-PAH-1028
FALCON-F-PAH-1024
FALCON-F-PAH-1025
FALCON-F-PAH-1022
FALCON-F-PAH-1023
FALCON-F-PAH-1020
FALCON-F-PAH-1021
FALCON-F-PAH-1018
FALCON-F-PAH-1019
FALCON-F-PAH-1015
FALCON-F-PAH-1016
FALCON-F-PAH-1017
20米道路

OWNER / DEVELOPER

micron

ARCHITECTURAL CONSULTANT

JJP ARCHITECTS & PLANNERS 潘冀聯合建築師

CIVIL & STRUCTURAL CONSULTANT

TEAM 群策工程股份有限公司

MECHANICAL & ELECTRICAL CONSULTANT & CONTRACTOR

UIS United Integrated Services 漢唐集成股份有限公司

SUB-CONTRACTOR

PROJECT ADDRESS

KEY PLAN

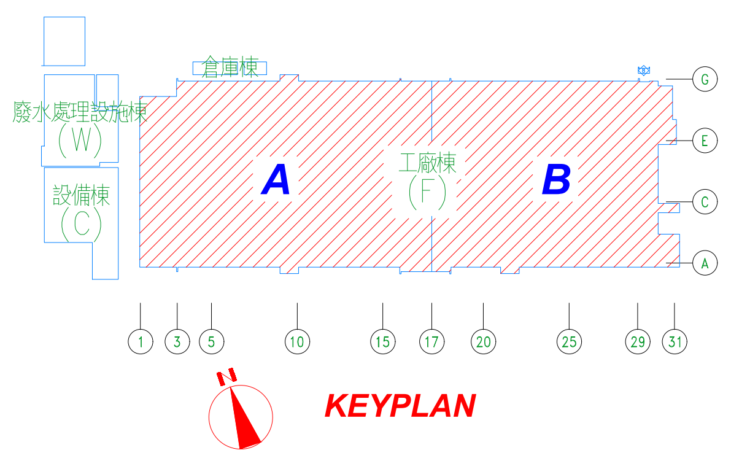

倉庫棟
廢水處理設施棟
(W)
設備棟
(C)
A
工廠棟
(F)
B
G
E
C
A
1
3
5
10
15
17
20
25
29
31
N
KEYPLAN

REV	DATE	DESCRIPTION	ISSUED BY
A	2025/01/02	REVIEW Drawing	

Revisions

PROJECT TITLE

Micron Falcon A Project (200K)

PROJECT PHASE

Concept Design

DRAWING TITLE

FLOOR PLAN -
DUCT SYSTEM
FAB A LEVEL 05
(OVERALL)

DESIGNED : JACK CHANG
DRAWN : JACK CHANG
CHECKED : C.S.HU
DATE : 2024/11/20
JOB NO. :
SCALE : 1:500

DRAWING NO. DE_F1_FAB_B001_M_DUCT_2L05-00
REV 0
SHEET:
SIZE A1