


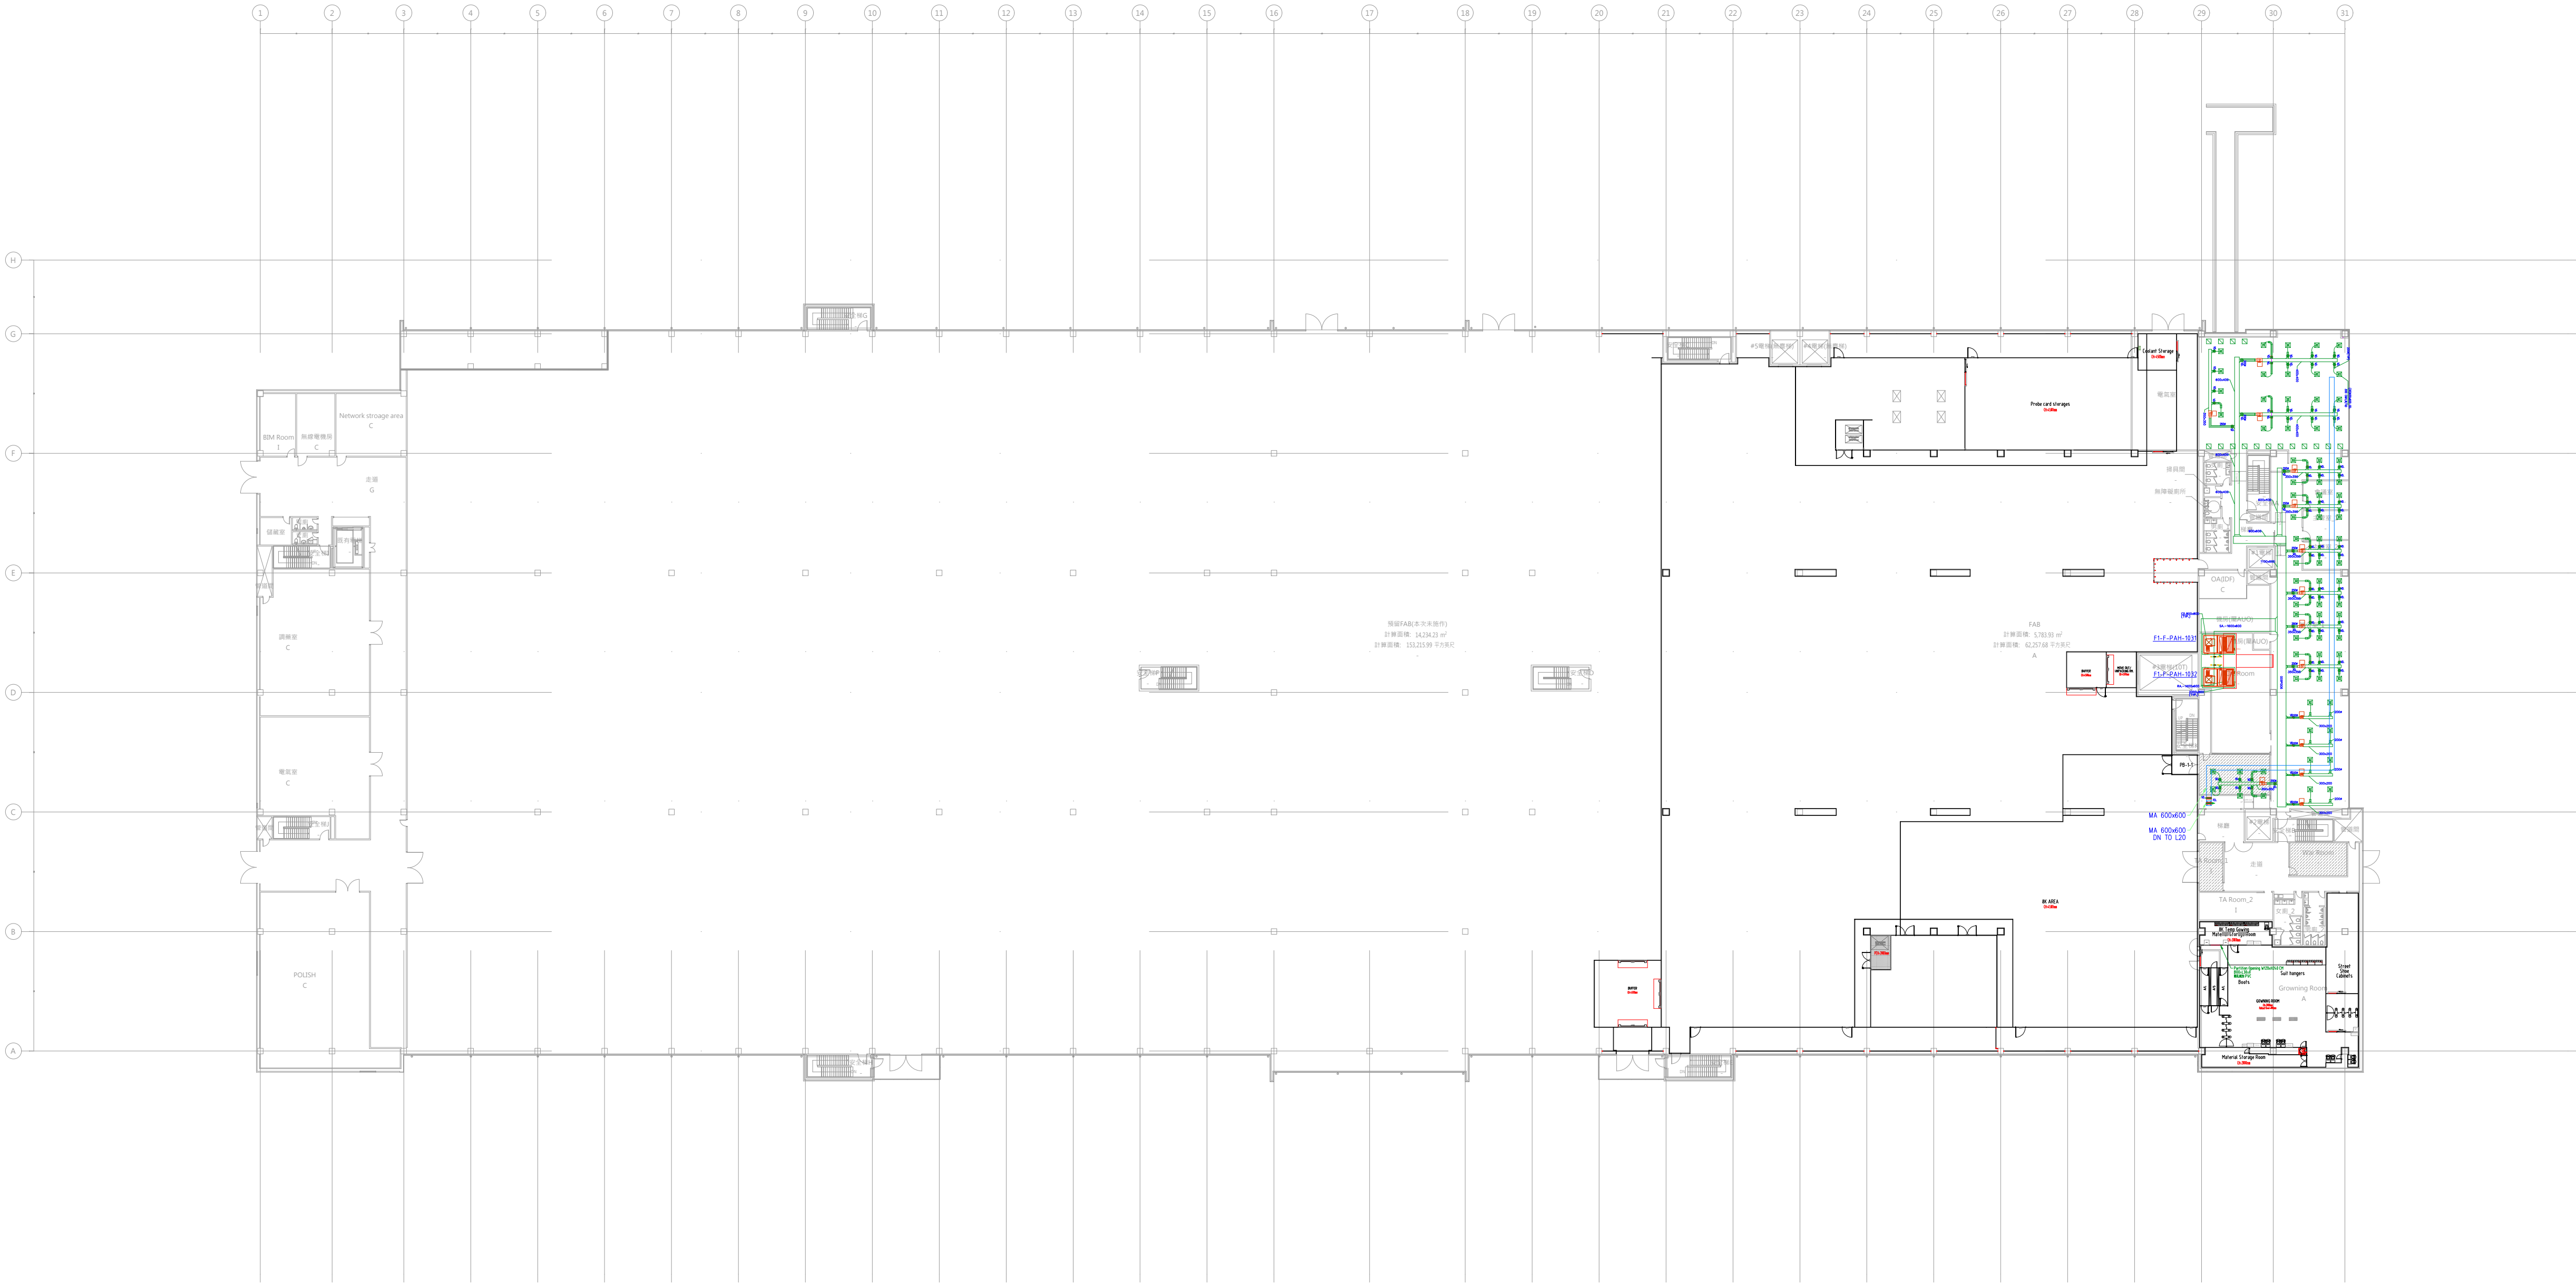

OWNER / DEVELOPER

micron

ARCHITECTURAL CONSULTANT

JJP ARCHITECTS & PLANNERS 潘冀聯合建築師

CIVIL & STRUCTURAL CONSULTANT


TEAM 群策工程股份有限公司

MECHANICAL & ELECTRICAL CONSULTANT & CONTRACTOR

uis 漢唐集成股份有限公司

SUB-CONTRACTOR

PROJECT ADDRESS

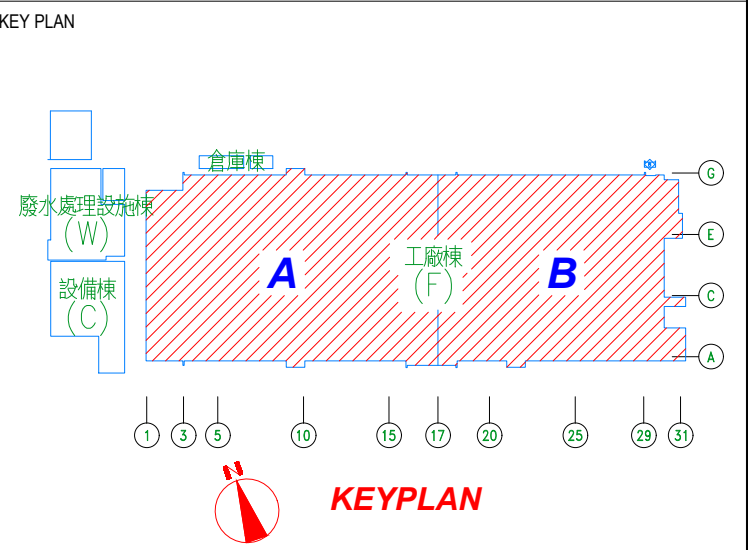

REV	DATE	DESCRIPTION	ISSUED BY
A	2025/01/02	REVIEW Drawing	

PROJECT TITLE

Micron Falcon A Project (200K)

PROJECT PHASE

Concept Design

DRAWING TITLE

**FLOOR PLAN -
DUCT SYSTEM
FAB A LEVEL 30
(OVERALL)**

DESIGNED: JACK CHANG	DRAWN: JACK CHANG	CHECKED: C.S.HU
DATE: 2024/11/20	JOB NO.:	SCALE: 1:500
DRAWING NO. DE_F1_FAB_B001_M_DUCT_2L30-00	REV 0	SIZE A1