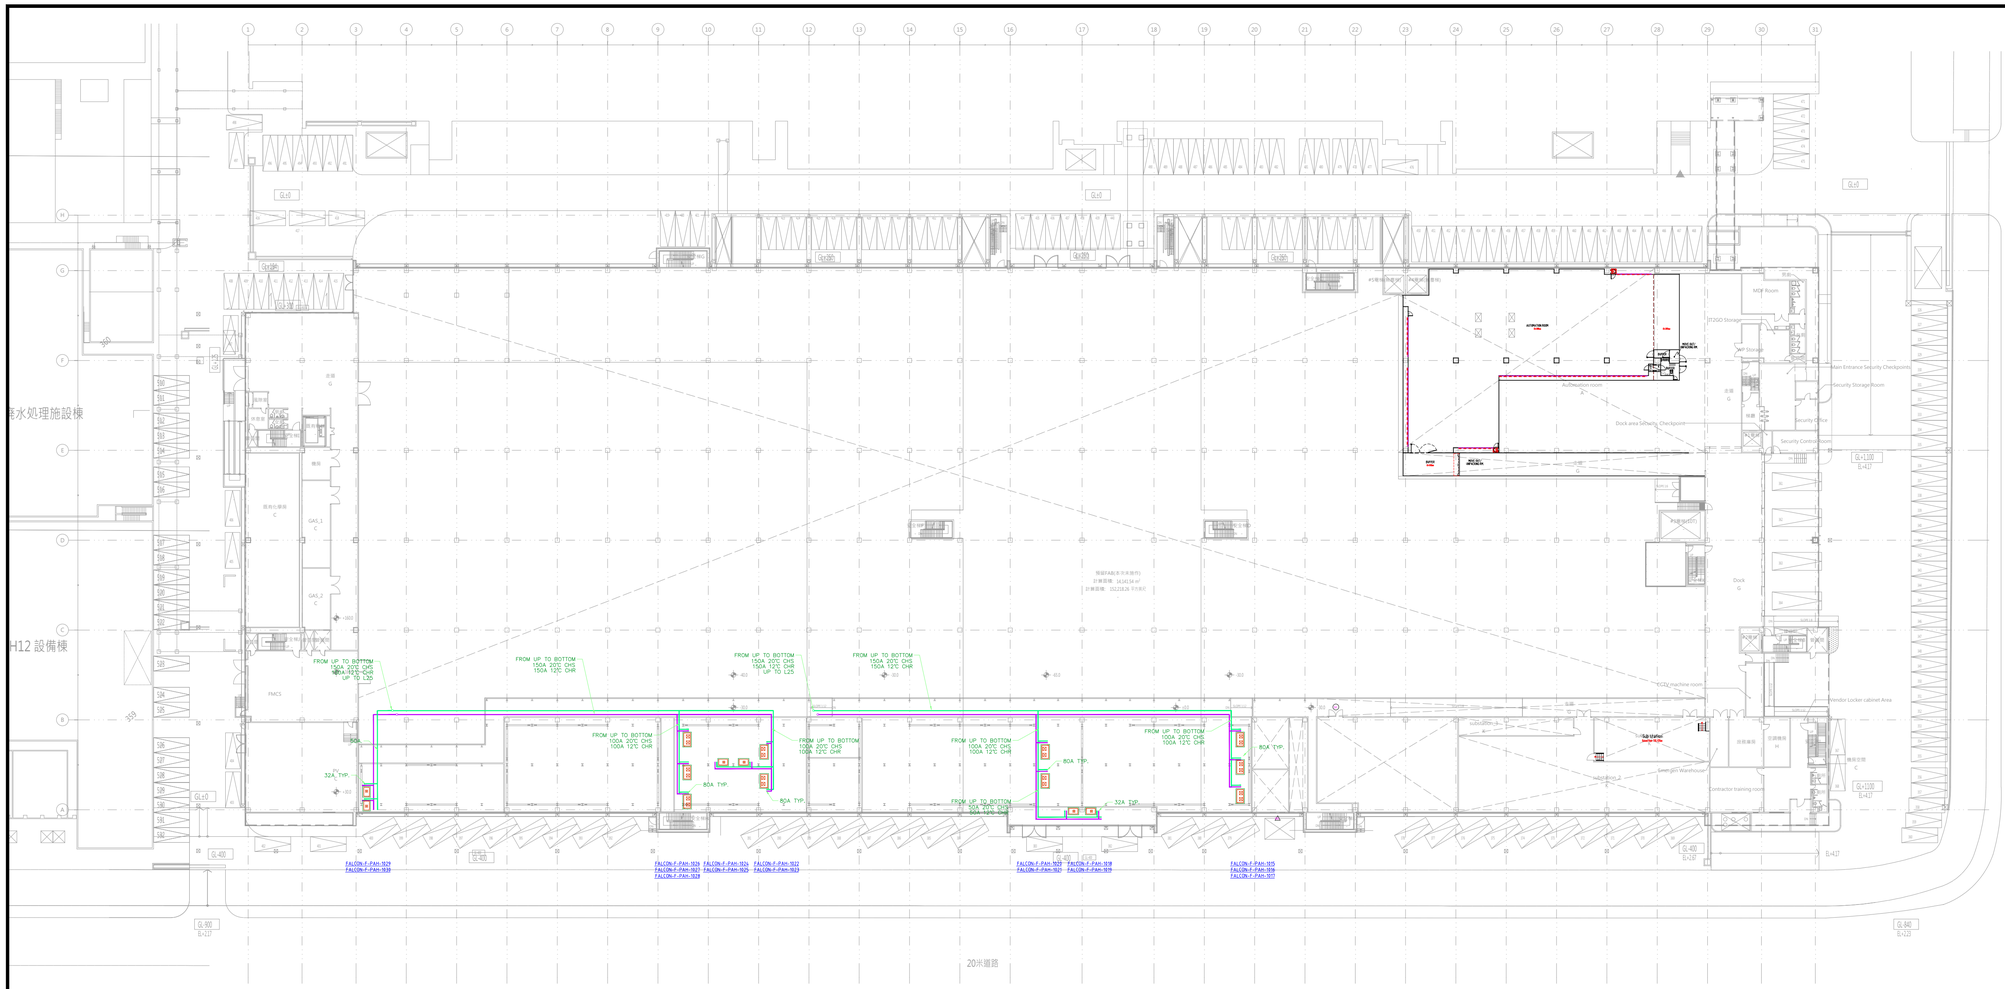

OWNER / DEVELOPER

micron

ARCHITECTURAL CONSULTANT

JJP ARCHITECTS & PLANNERS 潘冀聯合建築師

CIVIL & STRUCTURAL CONSULTANT

TEAM 群策工程股份有限公司

MECHANICAL & ELECTRICAL CONSULTANT & CONTRACTOR

UIS United Integrated Services 漢唐集成股份有限公司

SUB-CONTRACTOR

PROJECT ADDRESS

KEY PLAN

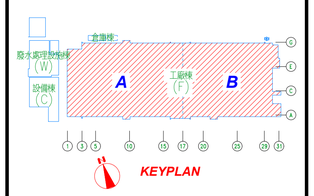

REV	DATE	DESCRIPTION	ISSUED BY
A	2025/01/02	REVIEW Drawing	

Revisions

PROJECT TITLE

Micron Falcon A Project (200K)

PROJECT PHASE

Concept Design

DRAWING TITLE

FLOOR PLAN -
PIPE SYSTEM
FAB A LEVEL 05
(OVERALL)

DESIGNED : JACK CHANG	DRAWN : JACK CHANG	CHECKED : C.S.HU	
DATE : 2024/11/20	JOB NO. :	SCALE : 1:500	
DRAWING NO. DE_F1_FAB_B001_M_PIPE_2L05-00			REV 0
		SHEET:	SIZE A1