

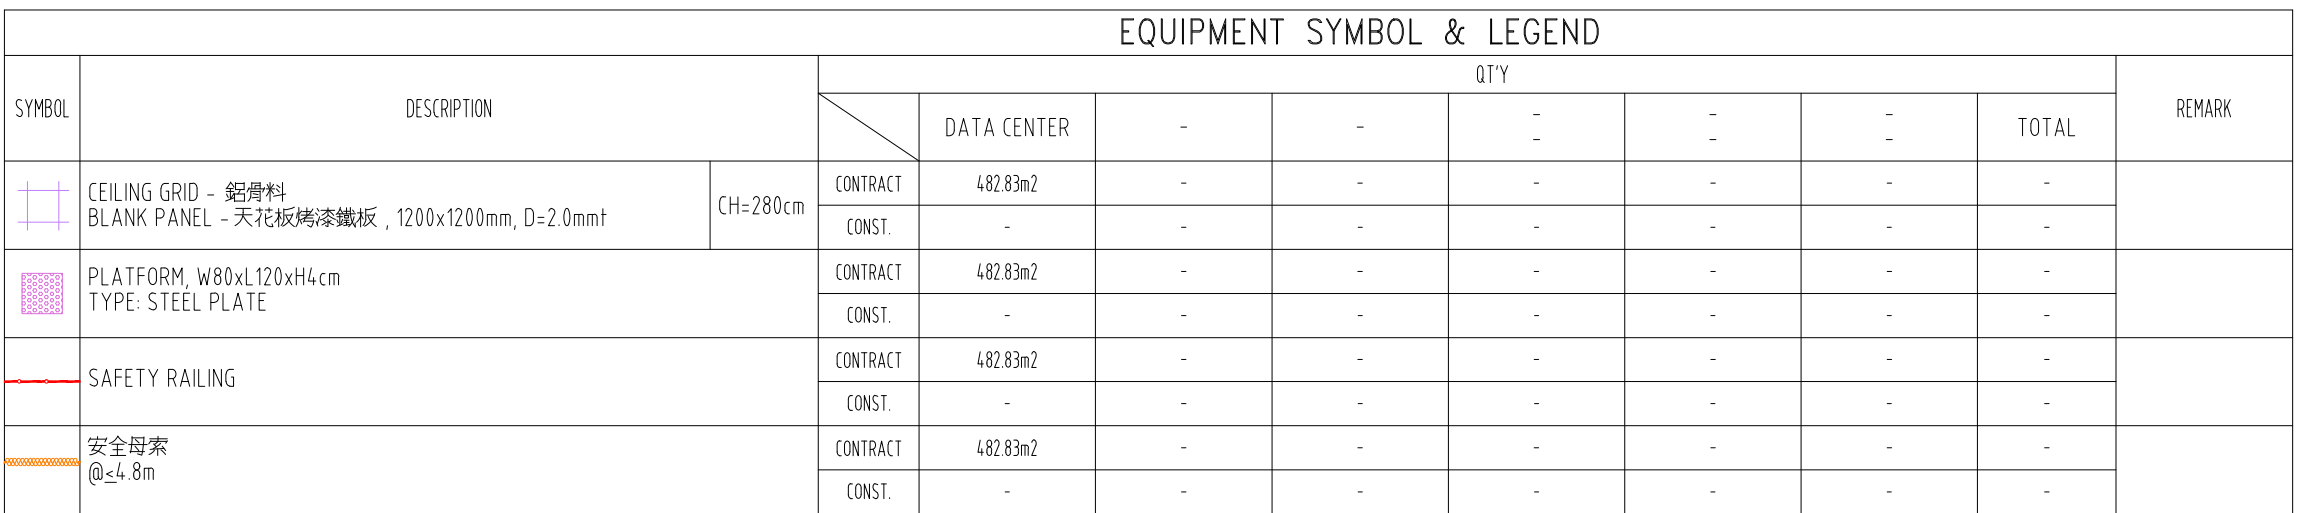


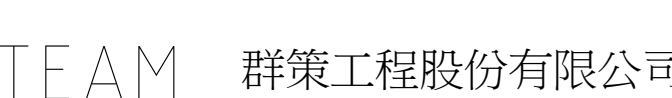

OWNER / DEVELOPER	
ARCHITECTURAL CONSULTANT	 
CIVIL & STRUCTURAL CONSULTANT	
MECHANICAL & ELECTRICAL CONSULTANT & CONTRACTOR	

PROJECT ADDRESS

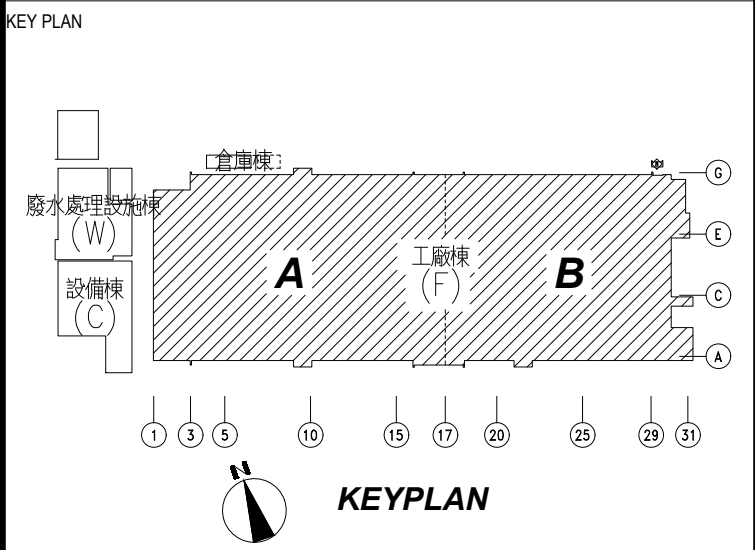

A	2025/01/02	REVIEW Drawing	
REV	DATE	DESCRIPTION	ISSUED BY
		Revisions	

PROJECT TITLE
Micron Falcon A Project (200K)

PROJECT PHASE

Concept Design

DRAWING TITLE

FLOOR PLAN -
CEILING SYSTEM
CUB LEVEL 20
(OVERALL)

DESIGNED : YEATS CHU		DRAWN : YEATS CHU		CHECKED : C.S.HU	
DATE : 2024/11/20		JOB NO.:		SCALE : 1:200	
DRAWING NO. DE_F1_CUB_B001_B_CEIL_2L20-00					REV 0
				SHEET:	SIZE A1