


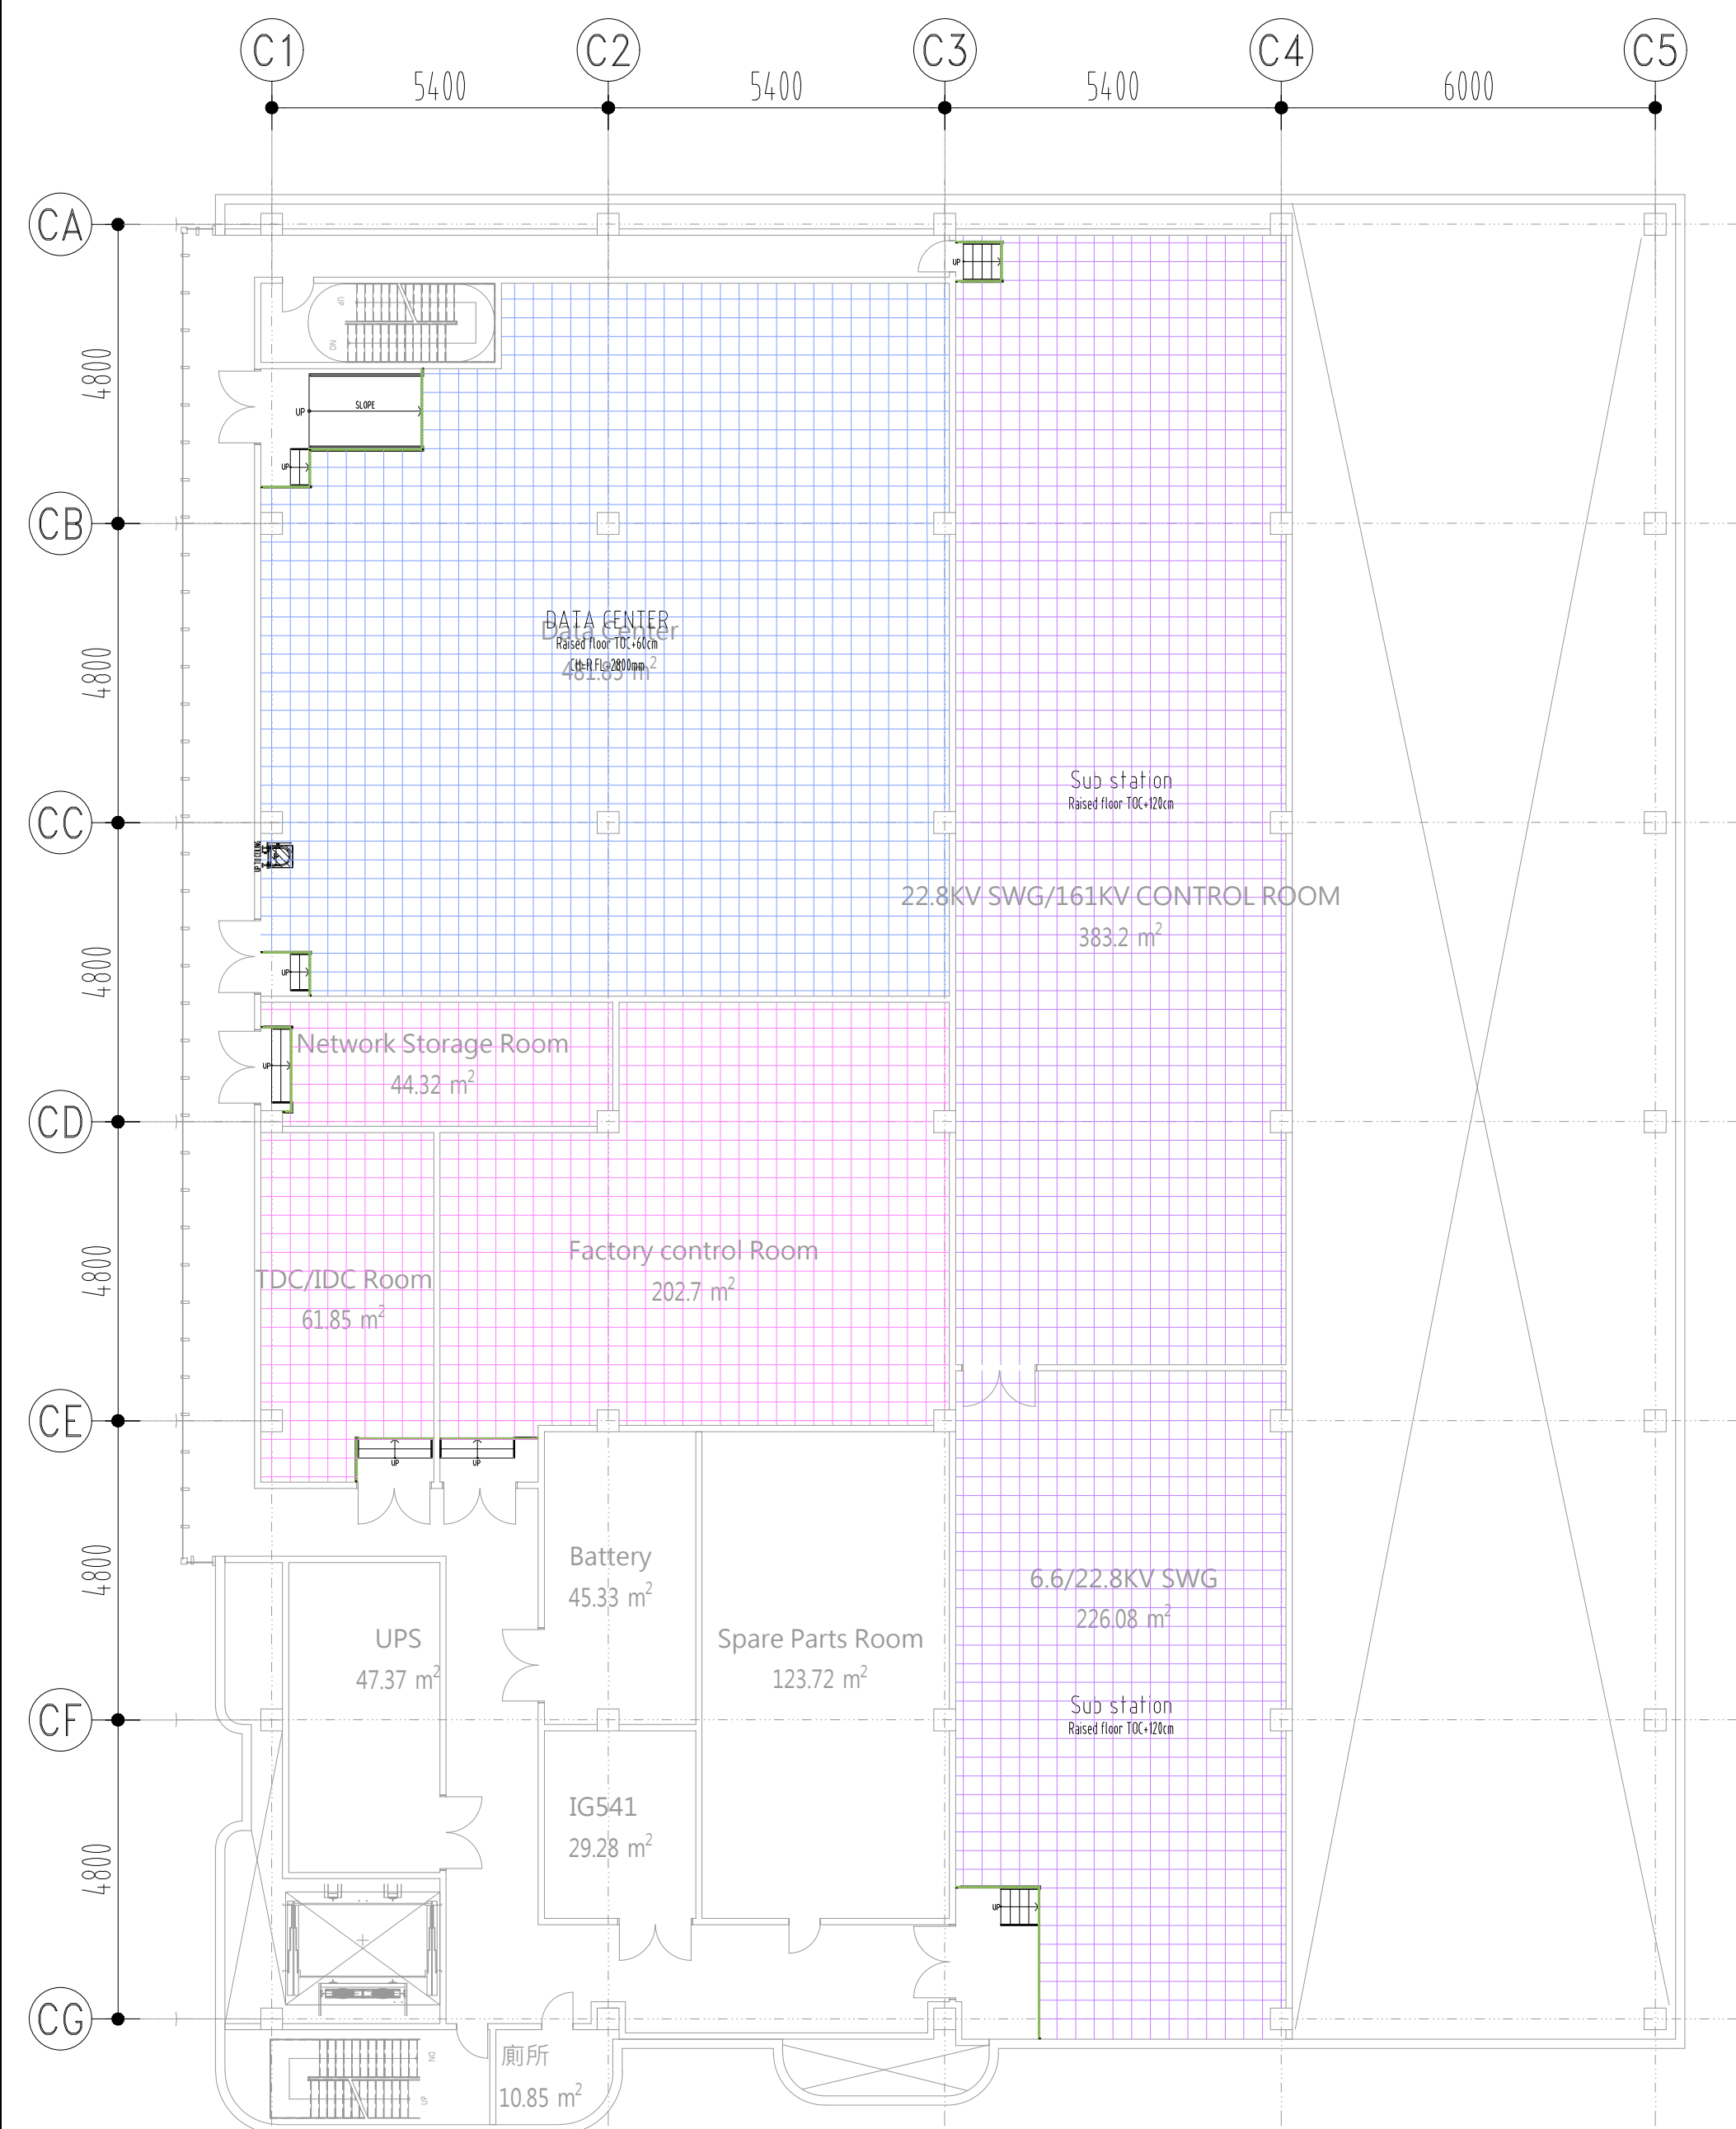

EQUIPMENT SYMBOL & LEGEND									
SYMBOL	DESCRIPTION	QTY							REMARK
		DATA CENTER	Sub station (1)	Sub station (2)	Network Storage ROOM	TDC/ADC ROOM	Factory control ROOM	TOTAL	
	RAISED FLOOR, 750mm 60x60cm, RH=45cm	CONTRACT	-	-	-	44.44m2	5168m2	2000m2	-
		CONST.	-	-	-	-	-	-	-
	RAISED FLOOR, 1000mm 60x60cm, RH=58cm (for DATA CENTER)	CONTRACT	4828m2	-	-	-	-	-	-
		CONST.	-	-	-	-	-	-	-
	RAISED FLOOR, 750mm 60x60cm, RH=120cm (for Substation)	CONTRACT	-	3796m2	27159m2	-	-	-	-
		CONST.	-	-	-	-	-	-	-
	DIVIDER, H=45cm (UNDER RAISED FLOOR)	CONTRACT	-	-	-	-	-	-	-
		CONST.	-	-	-	-	-	-	-
	DIVIDER, H=60cm (UNDER RAISED FLOOR) (for DATA CENTER)	CONTRACT	-	-	-	-	-	-	-
		CONST.	-	-	-	-	-	-	-
	DIVIDER, H=120cm (UNDER RAISED FLOOR) (for Substation)	CONTRACT	-	-	-	-	-	-	-
		CONST.	-	-	-	-	-	-	-



A	2025/01/02	REVIEW Drawing													
REV	DATE	DESCRIPTION						ISSUED BY							
Revisions															
PROJECT TITLE															
Micron Falcon A Project (200K)															
PROJECT PHASE															
Concept Design															
DRAWING TITLE															
FLOOR PLAN - FLOOR SYSTEM CUB LEVEL 20 (OVERALL)															
DESIGNED : YEATS CHU			DRAWN : YEATS CHU			CHECKED : C.S.HUI									
DATE : 2024/11/20			JOB NO. :			SCALE : 1/200									
DRAWING NO.									REV						
DE_F1_CUB_B001_B_RAFL_2L20-00									0						
							SHEET:	SIZE A1							