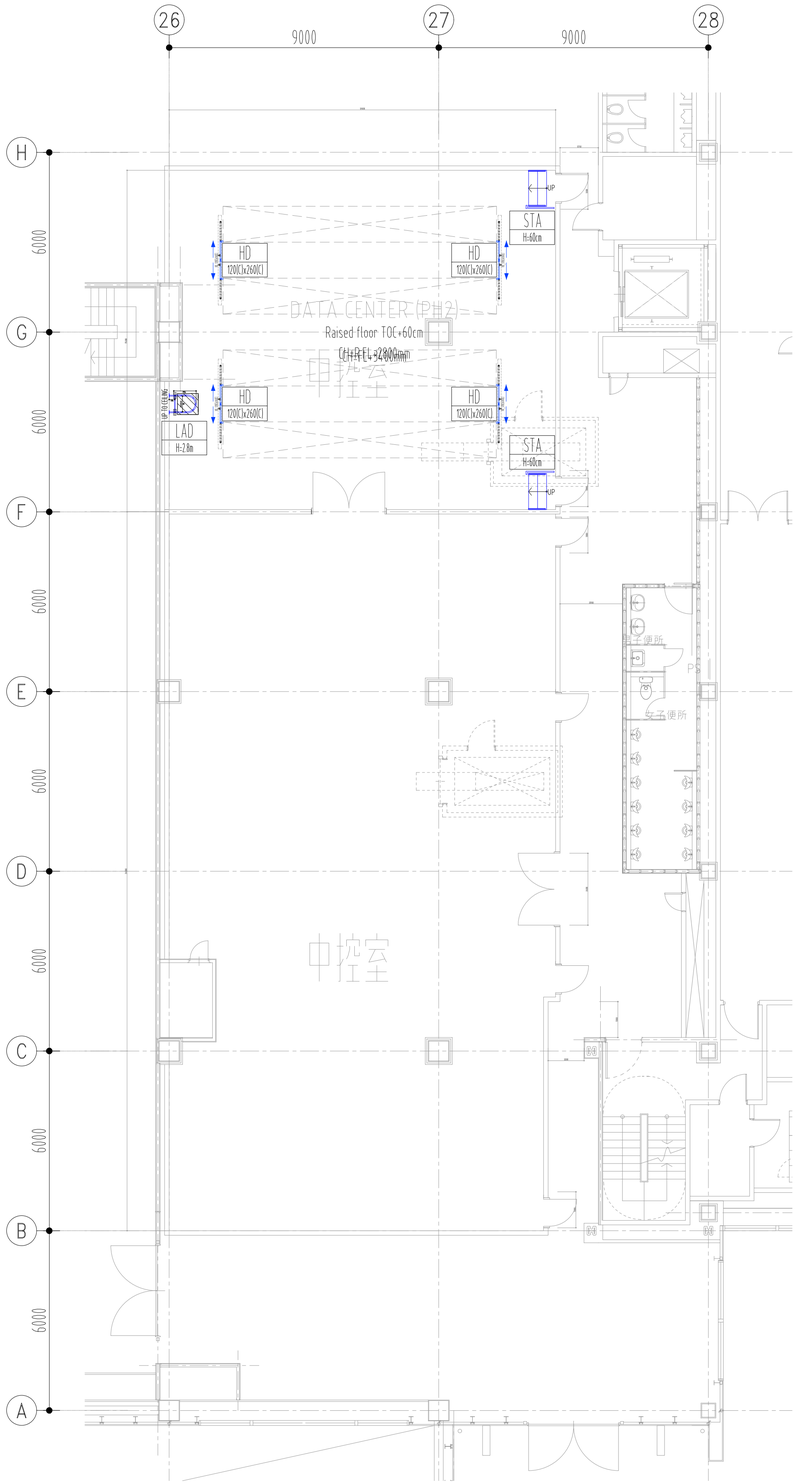

圖例說明

SYMBOL 圖例		MATERIAL 材料名稱	耐燃等級	WALL HEIGHT 高度 (m)
	Ps1	CLEANROOM WALL-ALUMINUM HONEYCOMB CORE, SINGLE SIDED ANTI-STATIC - 12mmT 蜜蜂巢金屬庫板牆，單面抗靜電	耐燃一級	-
	Pd2	CLEANROOM WALL-ALUMINUM HONEYCOMB CORE, DOUBLE SIDED ANTI-STATIC - 46mmT 蜜蜂巢金屬庫板牆，雙面抗靜電	耐燃一級	-
	P3	CLEANROOM WALL-ALUMINUM HONEYCOMB CORE - H-TYPE(46mmT) 蜜蜂巢金屬庫板牆	耐燃一級	2.8
	Ps4	CLEANROOM WALL-ALUMINUM HONEYCOMB CORE, SINGLE SIDED - H-TYPE(46mmT) 蜜蜂巢金屬庫板牆，單面抗靜電	耐燃一級	-
	R1	ROCKWOOL WALL- 50mmT 岩棉金屬隔間分間牆 (50mmT)	防火一小時	-
	Rs1	ROCKWOOL WALL- 50mmT SINGLE SIDED ANTI-STATIC - 100mmT 岩棉金屬隔間分間牆 (50mmT),單面抗靜電	防火一小時	-
	R2	ROCKWOOL WALL- 100mmT - 岩棉金屬隔間分間牆 (100mmT)	防火二小時	-
	Rs2	ROCKWOOL WALL SINGLE SIDED ANTI-STATIC - 100mmT 岩棉金屬隔間分間牆 (100mmT),單面抗靜電	防火二小時	-
	Rd2	ROCKWOOL WALL DOUBLE SIDED ANTI-STATIC - 100mmT 岩棉金屬隔間分間牆 (100mmT),雙面抗靜電	防火二小時	-
	D2	STEEL PANEL WITH HVAC EQUIPMENT & RETRUN AIR SHAFT 鐵皮隔間牆	不燃	-

EQUIPMENT SYMBOL & LEGEND

SYMBOL	DESCRIPTION	Q'TY	CR	-	-	TOTAL	REMARK
LAD	LADDER (UP TO CEILING), H=2.8m CEILING MAINTAIN DOOR FOR LADDER (0.7m x 0.7m)	CONTRACT	-	-	-	-	
		CONST	-	-	-	-	
P3	STAIRS (H=60cm) (for DTAT CENTER)	CONTRACT	-	-	-	-	
		CONST.	-	-	-	-	
	SLOPE (STAINLESS STEEL) S=6°	CONTRACT	-	-	-	-	
		CONST.	-	-	-	-	
		CONTRACT	-	-	-	-	
		CONST.	-	-	-	-	
		CONTRACT	-	-	-	-	
		CONST.	-	-	-	-	

DOOR SYMBOL & LEGEND

NO.	SYMBOL	DESCRIPTION TYPE / SIZE(CM)	Q'TY	CR	-	-	TOTAL	REMARK
D WX H		DOUBLE WING DOOR, WITH GLAZING						
		190W x 250H	CONTRACT	-	-	-	-	
			CONST.	-	-	-	-	
		-	CONTRACT	-	-	-	-	
			CONST.	-	-	-	-	
HD WX H		HAND DUBLE SINGLE-LEAF DOOR, WITH GLAZING						
		120W x 260H(CM)(CLEAN)	CONTRACT	-	-	-	-	
			CONST.	-	-	-	-	
		-	CONTRACT	-	-	-	-	
			CONST.	-	-	-	-	
HS WX H		HAND SLIDES SINGLE-LEAF DOOR, WITH GLAZING						
		120W x 260H(CM)(CLEAN)	CONTRACT	-	-	-	-	
			CONST.	-	-	-	-	
		-	CONTRACT	-	-	-	-	
			CONST.	-	-	-	-	
		-	CONTRACT	-	-	-	-	
			CONST.	-	-	-	-	

OWNER / DEVELOPER

micron

ARCHITECTURAL CONSULTANT

JJP ARCHITECTS & PLANNERS 潘冀聯合建築師

CIVIL & STRUCTURAL CONSULTANT

TEAM 群策工程股份有限公司

MECHANICAL & ELECTRICAL CONSULTANT & CONTRACTOR

UIS United Integrated Services 漢唐集成股份有限公司

SUB-CONTRACTOR

PROJECT ADDRESS

KEY PLAN

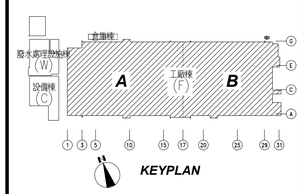

REV	DATE	DESCRIPTION	ISSUED BY
A	2025/01/02	REVIEW Drawing	

Revisions

PROJECT TITLE

Micron Falcon A Project (200K)

PROJECT PHASE

Concept Design

DRAWING TITLE

FLOOR PLAN -
PARTITION SYSTEM
NORTH FAB DATA CENTER LEVEL 20
(OVERALL)

DESIGNED :	YEATS CHU	DRAWN :	YEATS CHU	CHECKED :	C.S.HU
DATE :	2024/11/20	JOB NO. :		SCALE :	1:100

DRAWING NO. DE_F1_DATA_B001_B_PRTN_2L20-00

REV 0

SHEET:

SIZE A1