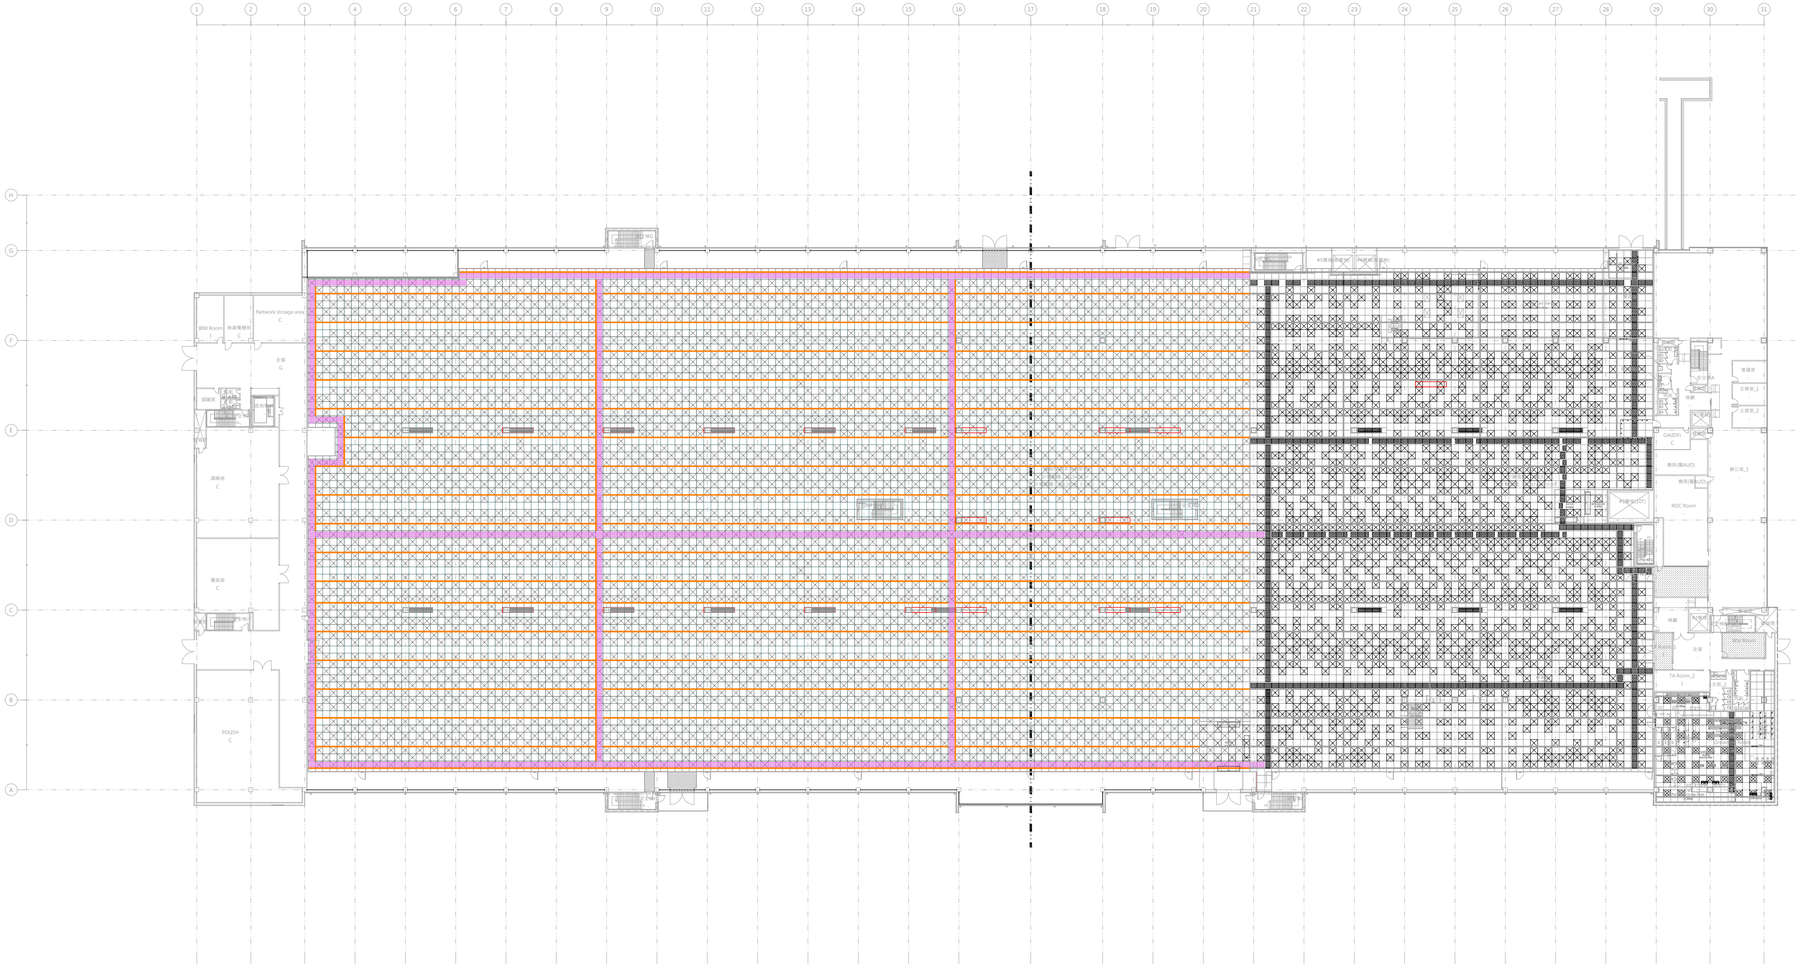

圖例說明

SYMBOL 圖例		MATERIAL 材料名稱	耐燃等級	WALL HEIGHT 高度 (m)
	-	CLEANROOM WALL-ALUMINUM HONEYCOMB CORE, SINGLE SIDED ANTI-STATIC - 12mm† 潔淨無金屬庫板牆，單面抗靜電	耐燃一級	-
	-	CLEANROOM WALL-ALUMINUM HONEYCOMB CORE, DOUBLE SIDED ANTI-STATIC - 46mm† 潔淨無金屬庫板牆，雙面抗靜電	耐燃一級	-
	-	CLEANROOM WALL-ALUMINUM HONEYCOMB CORE, - H-TYPE(46mm†) 潔淨無金屬庫板牆	耐燃一級	-
	-	CLEANROOM WALL-ALUMINUM HONEYCOMB CORE, SINGLE SIDED - H-TYPE(46mm†) 潔淨無金屬庫板牆，單面抗靜電	耐燃一級	-
	-	1 HOUR FIRE-RATED WALL - 50mm† 岩棉金屬隔間分間牆 (50mm†)	防火一小時	-
	-			-
	-	1 HOUR FIRE-RATED WALL - 50mm† 岩棉金屬隔間分間牆 (50mm†)	防火一小時	-
	-			-
	-	2 HOUR FIRE-RATED WALL - 100mm† 岩棉金屬隔間分間牆 (100mm†)	防火二小時	-
	-	2 HOUR FIRE-RATED WALL SINGLE SIDED ANTI-STATIC - 100mm† 岩棉金屬隔間分間牆 (100mm†)，單面抗靜電	防火二小時	-
	-	2 HOUR FIRE-RATED WALL DOUBLE SIDED ANTI-STATIC - 100mm† 岩棉金屬隔間分間牆 (100mm†)，雙面抗靜電	防火二小時	-
	-	STEEL PANEL WITH HVAC EQUIPMENT & RETURN AIR SHAFT 鐵皮隔間牆	不燃	-
	-	DIVIDER (ON CEILING) 鐵皮隔間牆	不燃	3.9~4.9

EQUIPMENT SYMBOL & LEGEND

SYMBOL	DESCRIPTION	Q'TY	CR	-	-	TOTAL	REMARK
	PLATFORM, W80xL120xH4cm TYPE: STEEL PLATE	CONTRACT	-	-	-	-	
		CONST.	-	-	-	-	
	PLATFORM, W60xL120xH4cm TYPE: STEEL PLATE	CONTRACT	-	-	-	-	
		CONST.	-	-	-	-	
	PLATFORM, W80xL55xH4cm TYPE: STEEL PLATE	CONTRACT	-	-	-	-	
		CONST.	-	-	-	-	
	PLATFORM, OTHER TYPE: STEEL PLATE	CONTRACT	-	-	-	-	
		CONST.	-	-	-	-	
	SAFETY RAILING	CONTRACT	-	-	-	-	
		CONST.	-	-	-	-	
	安全母索 @≤4.8m	CONTRACT	-	-	-	-	
		CONST.	-	-	-	-	
		CONTRACT	-	-	-	-	
		CONST.	-	-	-	-	
		CONTRACT	-	-	-	-	
		CONST.	-	-	-	-	

DOOR SYMBOL & LEGEND

NO.	SYMBOL	DESCRIPTION TYPE / SIZE(CM)	Q'TY	CR	-	-	TOTAL	REMARK
M1 1.0xW		CEILING MAINTAIN DOOR, STEEL PLANT (FOR LADDER)						
		70L x 70W	CONTRACT	-	-	-	-	
			CONST.	-	-	-	-	
		-	CONTRACT	-	-	-	-	
			CONST.	-	-	-	-	
		-	CONTRACT	-	-	-	-	
			CONST.	-	-	-	-	
M5 W=1.8		SINGLE WING DOOR (圓型拉環鎖 + 輔助鎖)						
		180W x 200H	CONTRACT	-	-	-	-	
			CONST.	-	-	-	-	
		-	CONTRACT	-	-	-	-	
			CONST.	-	-	-	-	
		-						
		-	CONTRACT	-	-	-	-	
			CONST.	-	-	-	-	
		-	CONTRACT	-	-	-	-	
			CONST.	-	-	-	-	
		-						
		-	CONTRACT	-	-	-	-	
			CONST.	-	-	-	-	
		-	CONTRACT	-	-	-	-	
			CONST.	-	-	-	-	

OWNER / DEVELOPER

micron

ARCHITECTURAL CONSULTANT

JJP ARCHITECTS & PLANNERS 潘冀聯合建築師

CIVIL & STRUCTURAL CONSULTANT

TEAM 群策工程股份有限公司

MECHANICAL & ELECTRICAL CONSULTANT & CONTRACTOR

UIS United Integrated Services 漢唐集成股份有限公司

SUB-CONTRACTOR

PROJECT ADDRESS

KEY PLAN

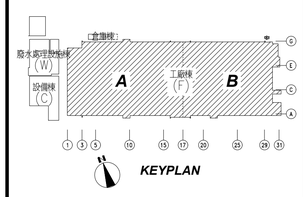

REV	DATE	DESCRIPTION	ISSUED BY
A	2025/01/02	REVIEW Drawing	

Revisions

PROJECT TITLE

Micron Falcon A Project (200K)

PROJECT PHASE

Concept Design

DRAWING TITLE

FLOOR PLAN -
CATWALK SYSTEM
FAB LEVEL 35
(OVERALL)

DESIGNED : YEATS CHU	DRAWN : YEATS CHU	CHECKED : C.S.HU	
DATE : 2024/11/20	JOB NO. :	SCALE : 1:500	

DRAWING NO. DE_F1_FAB_B001_B_CATW_2L35-00 REV 0

SHEET: SIZE A1