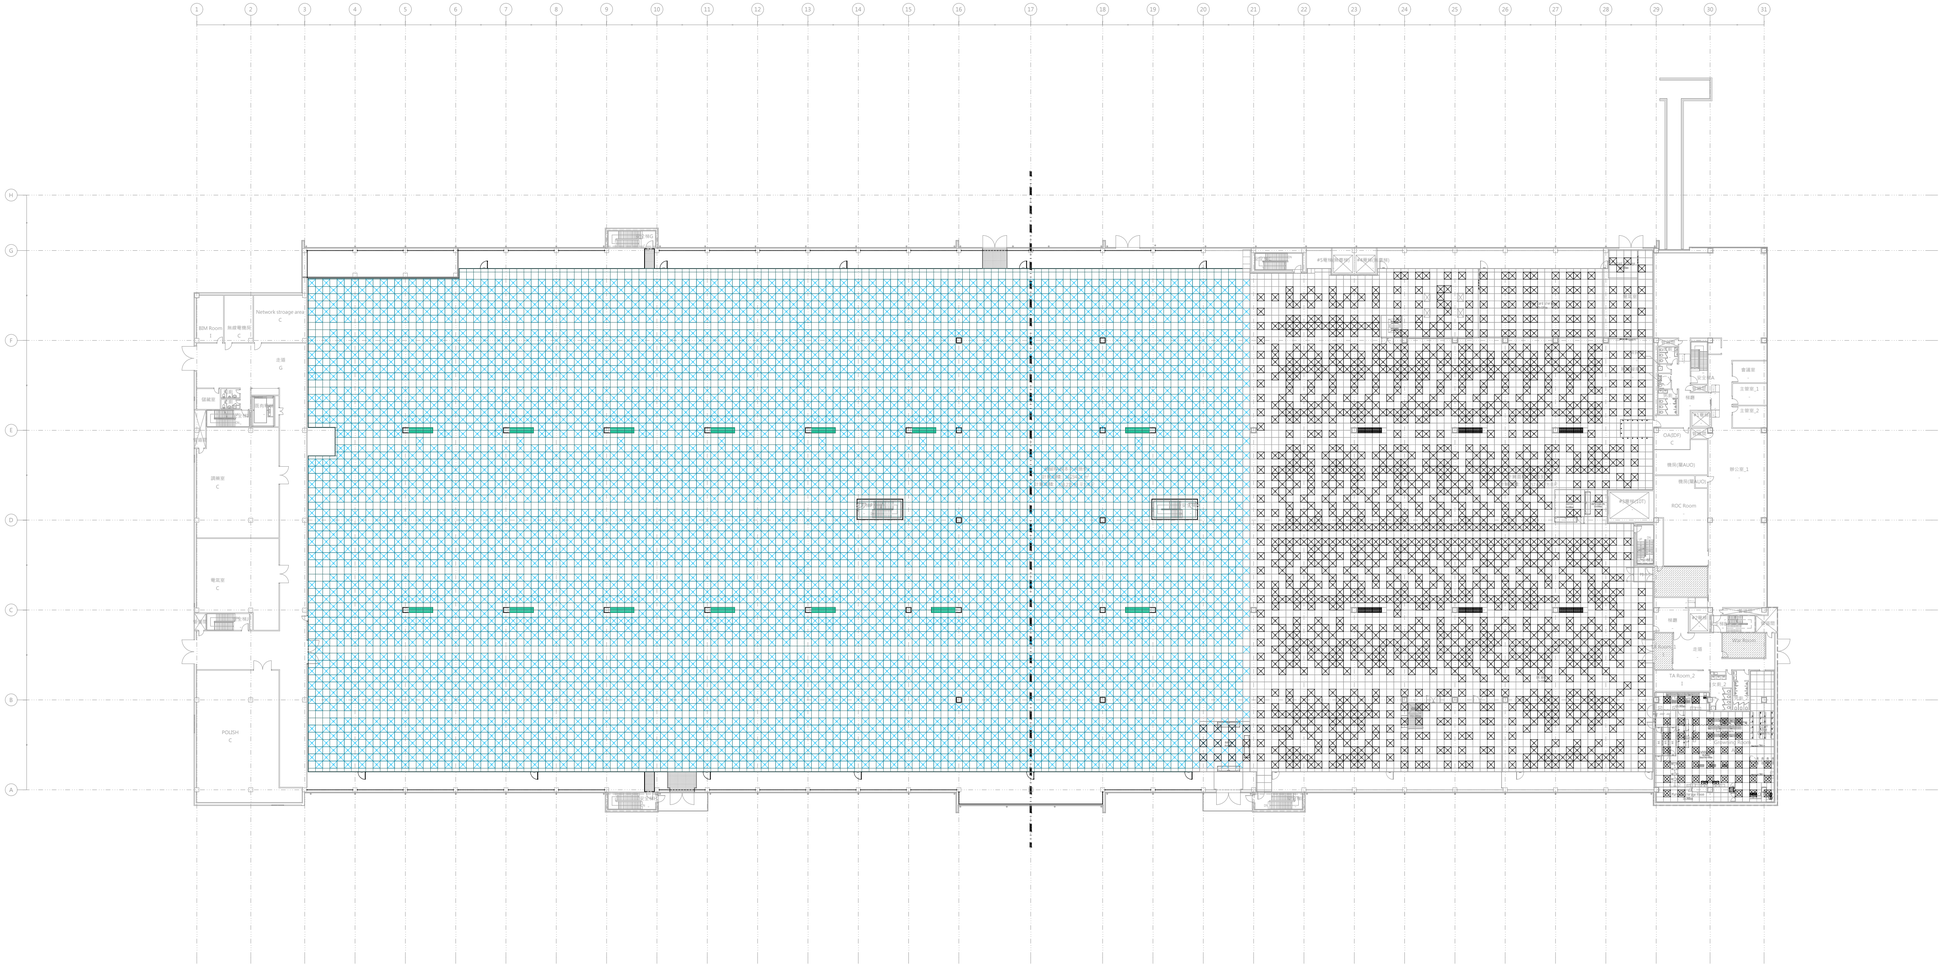

CEILING SYSTEM SYMBOL & LEGEND

SYMBOL	DESCRIPTION	QT'Y	CR	GOWN	-	-	TOTAL	REMARK
	FAN FILTER UNIT (HEPA), 120x120cm	CONTRACT	-	-	-	-	-	
		CONST.	-	-	-	-	-	
	FAN FILTER UNIT (ULPA), 120x120cm	CONTRACT	1,460	42	-	-	-	
		CONST.	-	-	-	-	-	
	FAN FILTER UNIT (ULPA), PTFE 120x120cm	CONTRACT	-	-	-	-	-	
		CONST.	-	-	-	-	-	
	AIR RETURN (FOR CEILING) 120x120cm	CONTRACT	-	-	-	-	-	
		CONST.	-	-	-	-	-	
	STRAIGHT JOINT	CONTRACT	-	-	-	-	-	
		CONST.	-	-	-	-	-	
	STRAIGHT JOINT (K=8.1)	CONTRACT	-	-	-	-	-	
		CONST.	-	-	-	-	-	
	CH-280cm							
	-							
	-							
	-							
	-	CEILING GRID - BLANK PANEL 120x120cm, D=2.0mm†						
	-							
	CH=450cm							
	-							
	-							
	-							
	DRY COOLING COIL							
	SMOKE EXHAUST GRILLE 120x120cm							
	LIGHTING FIXTURE 120x60cm							

OWNER / DEVELOPER

micron

ARCHITECTURAL CONSULTANT

JJP ARCHITECTS & PLANNERS 潘冀聯合建築師

CIVIL & STRUCTURAL CONSULTANT

TEAM 群策工程股份有限公司

MECHANICAL & ELECTRICAL CONSULTANT & CONTRACTOR

uis Unified Integrated Services 漢唐集成股份有限公司

SUB-CONTRACTOR

PROJECT ADDRESS

KEY PLAN

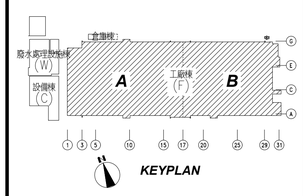

REV	DATE	DESCRIPTION	ISSUED BY
A	2025/01/02	REVIEW Drawing	

Revisions

PROJECT TITLE

Micron Falcon A Project (200K)

PROJECT PHASE

Concept Design

DRAWING TITLE

FLOOR PLAN -
CEILING SYSTEM
FAB LEVEL 30
(OVERALL)

DESIGNED :	YEATS CHU	DRAWN :	YEATS CHU	CHECKED :	C.S.HU
DATE :	2024/11/20	JOB NO. :		SCALE :	1:500

DRAWING NO. DE_F1_FAB_B001_B_CEIL_2L30-00 REV 0

SHEET: SIZE A1