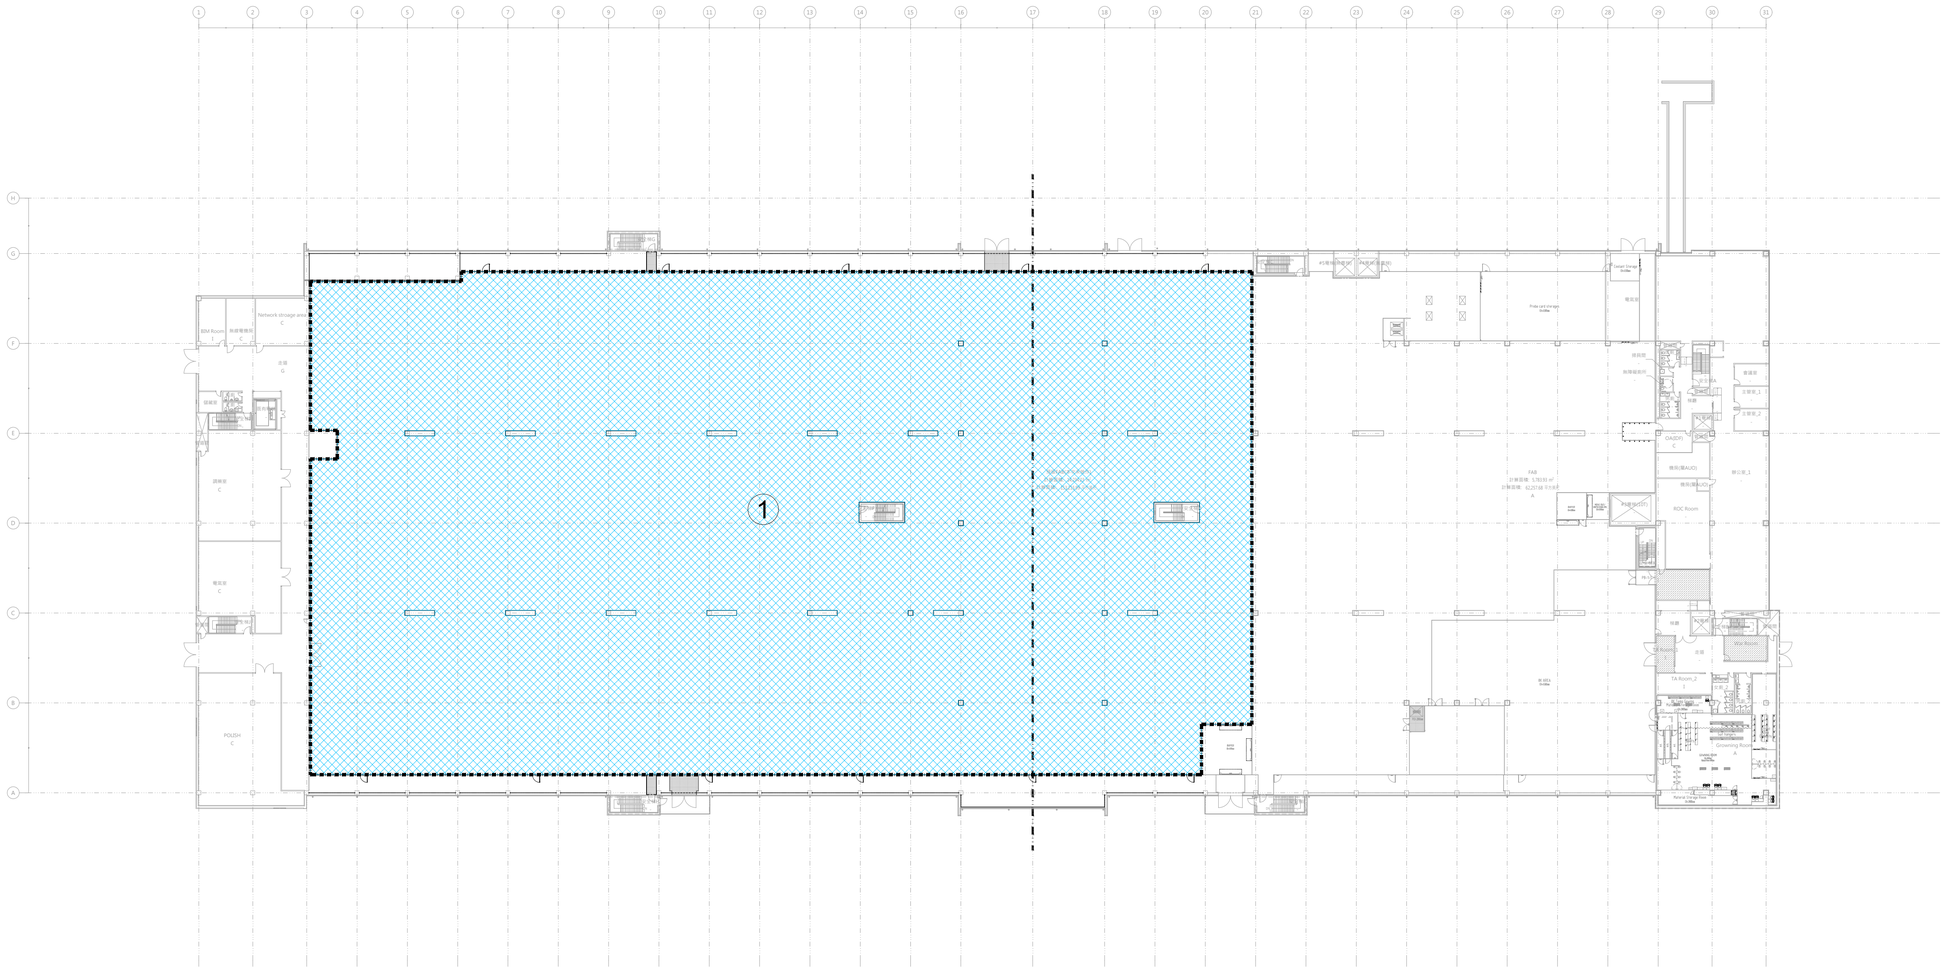


SYMBOL & LEGEND	
	ISO 6 (CLASS 1000)
	ISO 7 (CLASS 10K)

ROOM			CLEANLINESS AS-BUILT (ISO)	TEMPERATURE (°C)	RELATIVE HUMIDITY (%)	NOISE	ILLUMINANCE (lux)	REMARK'S
NO.	DESCRIPTION	CEILING HEIGHT (mm)						
1	CLEANROOM	4500	ISO 6	22.5±2	45±5	<NC60	500	
2	-	-	-	-	-	-	-	
3	-	-	-	-	-	-	-	
4	-	-	-	-	-	-	-	
5	-	-	-	-	-	-	-	
6	-	-	-	-	-	-	-	
8	-	-	-	-	-	-	-	

OWNER / DEVELOPER

micron

ARCHITECTURAL CONSULTANT

JJP ARCHITECTS & PLANNERS 潘冀聯合建築師

CIVIL & STRUCTURAL CONSULTANT

TEAM 群策工程股份有限公司


MECHANICAL & ELECTRICAL CONSULTANT & CONTRACTOR

uis United Integrated Services 漢唐集成股份有限公司

SUB-CONTRACTOR

PROJECT ADDRESS

KEY PLAN

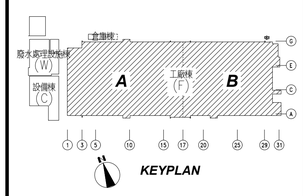

REV	DATE	DESCRIPTION	ISSUED BY
A	2025/01/02	REVIEW Drawing	

Revisions

PROJECT TITLE

Micron Falcon A Project (200K)

PROJECT PHASE

Concept Design

DRAWING TITLE

FLOOR PLAN -
CLEAN CLEANLINESS
FAB LEVEL 30
(OVERALL)

DESIGNED :	YEATS CHU	DRAWN :	YEATS CHU	CHECKED :	C.S.HU
DATE :	2024/11/20	JOB NO. :		SCALE :	1:500

DRAWING NO. DE_F1_FAB_B001_B_CLZN_2L30-00 REV 0

SHEET: SIZE A1