


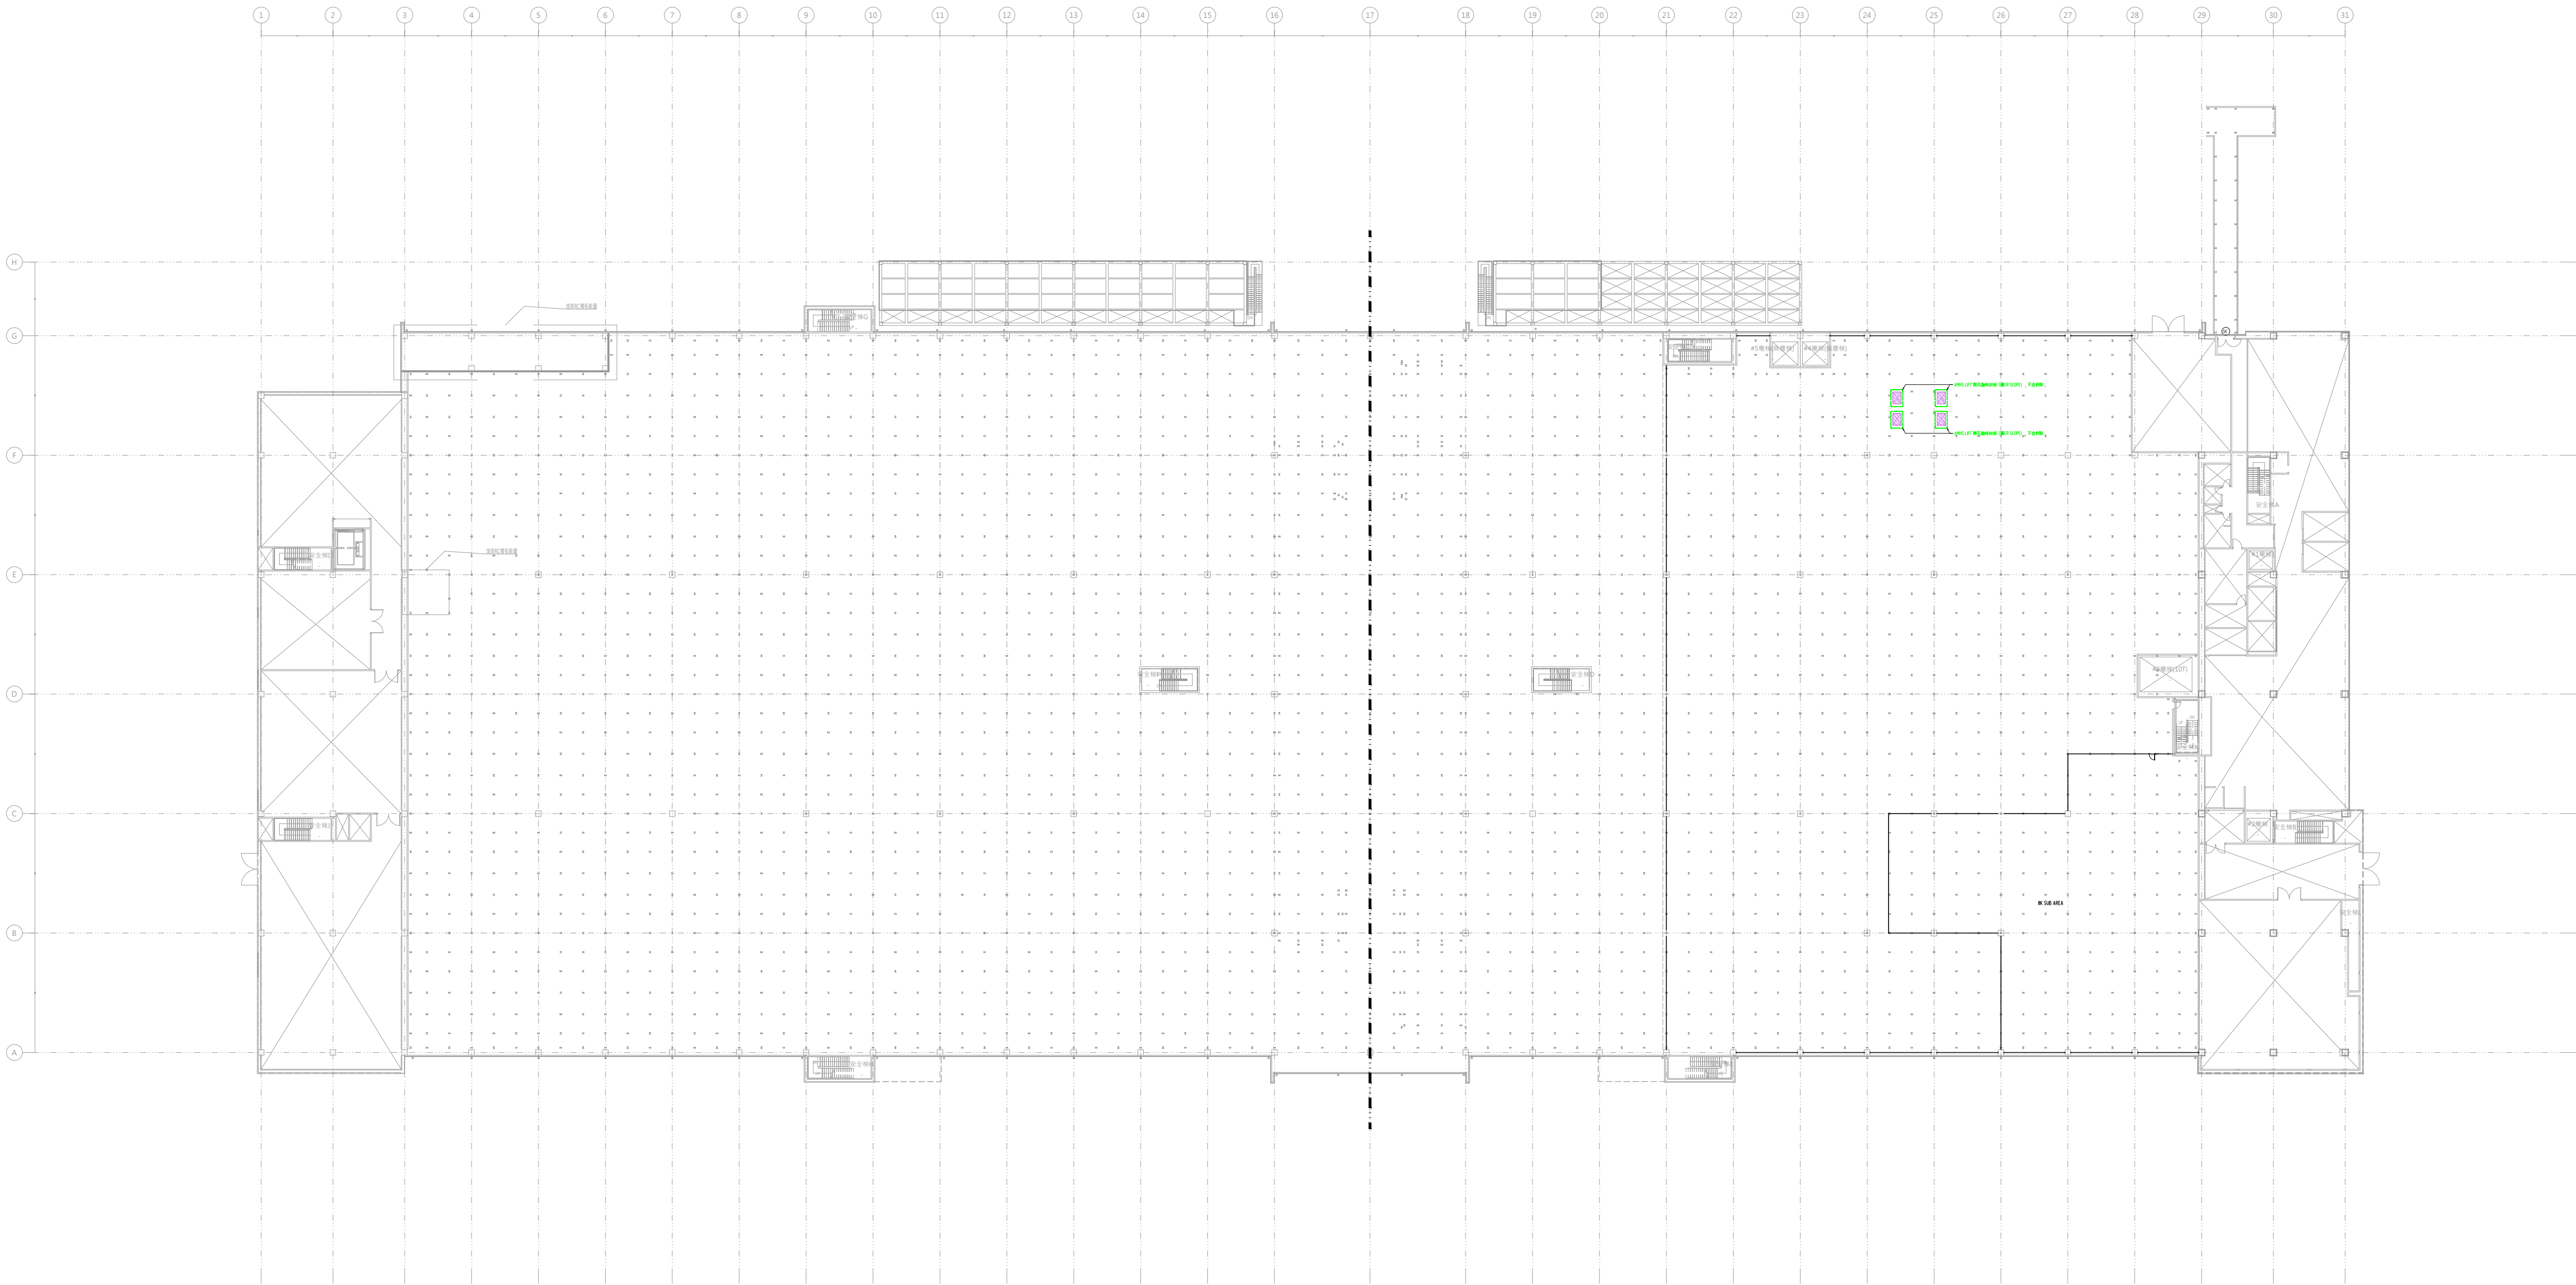

圖例說明

SYMBOL 圖例		MATERIAL 材料名稱	耐燃等級	WALL HEIGHT 高度 (m)	DOOR SYMBOL & LEGEND								
					NO.	SYMBOL	DESCRIPTION TYPE / SIZE (CM)	QTY				REMARK	
					YES NO		SINGLE E WING DOOR (雙型拉環鎖, 輔助鎖)		CR	-	-	TOTAL	
	Ps1	CLEANROOM WALL-ALUMINUM HONEYCOMB CORE, SINGLE SIDED ANTI-STATIC - 12mm 絕緣巢金屬單板牆, 單面抗靜電	耐燃一級	-			80W x 190H	CONTRACT	-	-	-	-	
	Pd2	CLEANROOM WALL-ALUMINUM HONEYCOMB CORE, DOUBLE SIDED ANTI-STATIC - 46mm 絕緣巢金屬單板牆, 雙面抗靜電	耐燃一級	-				CONST.	-	-	-	-	
	P3	CLEANROOM WALL-ALUMINUM HONEYCOMB CORE - H-TYPE(46mm) 絕緣巢金屬單板牆	耐燃一級	1.9				CONTRACT	-	-	-	-	
	Ps4	CLEANROOM WALL-ALUMINUM HONEYCOMB CORE, SINGLE SIDED - H-TYPE(46mm) 絕緣巢金屬單板牆, 單面抗靜電	耐燃一級	-				CONST.	-	-	-	-	
	R1	ROCKWOOL WALL- 50mm 岩棉金屬隔間分間牆 (50mm)	防火一小時	1.9				CONTRACT	-	-	-	-	
	Rs1	ROCKWOOL WALL- 50mm SINGLE SIDED ANTI-STATIC - 100mm 岩棉金屬隔間分間牆 (50mm), 單面抗靜電	防火一小時	-				CONST.	-	-	-	-	
	R2	ROCKWOOL WALL- 100mm 岩棉金屬隔間分間牆 (100mm)	防火二小時	-				CONTRACT	-	-	-	-	
	Rs2	ROCKWOOL WALL SINGLE SIDED ANTI-STATIC - 100mm 岩棉金屬隔間分間牆 (100mm), 單面抗靜電	防火二小時	-				CONST.	-	-	-	-	
	Rd2	ROCKWOOL WALL DOUBLE SIDED ANTI-STATIC - 100mm 岩棉金屬隔間分間牆 (100mm), 雙面抗靜電	防火二小時	-				CONTRACT	-	-	-	-	
	D2	STEEL PANEL WITH HVAC EQUIPMENT & RETURN AIR SHAFT 鐵皮隔間牆	不燃	-				CONST.	-	-	-	-	

OWNER / DEVELOPER

micron.

ARCHITECTURAL CONSULTANT

JJP ARCHITECTS & PLANNERS

潘冀聯合建築師

CIVIL & STRUCTURAL CONSULTANT

TEAM

群策工程股份有限公司

MECHANICAL & ELECTRICAL CONSULTANT & CONTRACTOR

uis 漢唐集成股份有限公司

SUB-CONTRACTOR

PROJECT ADDRESS

KEY PLAN

廠水電工程設備

設備梯

工廠梯

倉庫梯

A

F

B

1

3

5

10

15

20

25

29

31

1

2

3

4

KEYPLAN

PROJECT TITLE

Micron Falcon A Project (200K)

PROJECT PHASE

Concept Design

DRAWING TITLE

FLOOR PLAN - PARTITION SYSTEM
FAB LEVEL 25
(OVERALL)

DESIGNED : YEATS CHU

DRAWN : YEATS CHU

CHECKED : C.S.HU

DATE : 2024/11/20

JOB NO. :

SCALE : 1:500

DRAWING NO.

DE_F1_FAB_B001_B_PRTN_2L25-00

REV

0

SHEET:

SIZE

A1