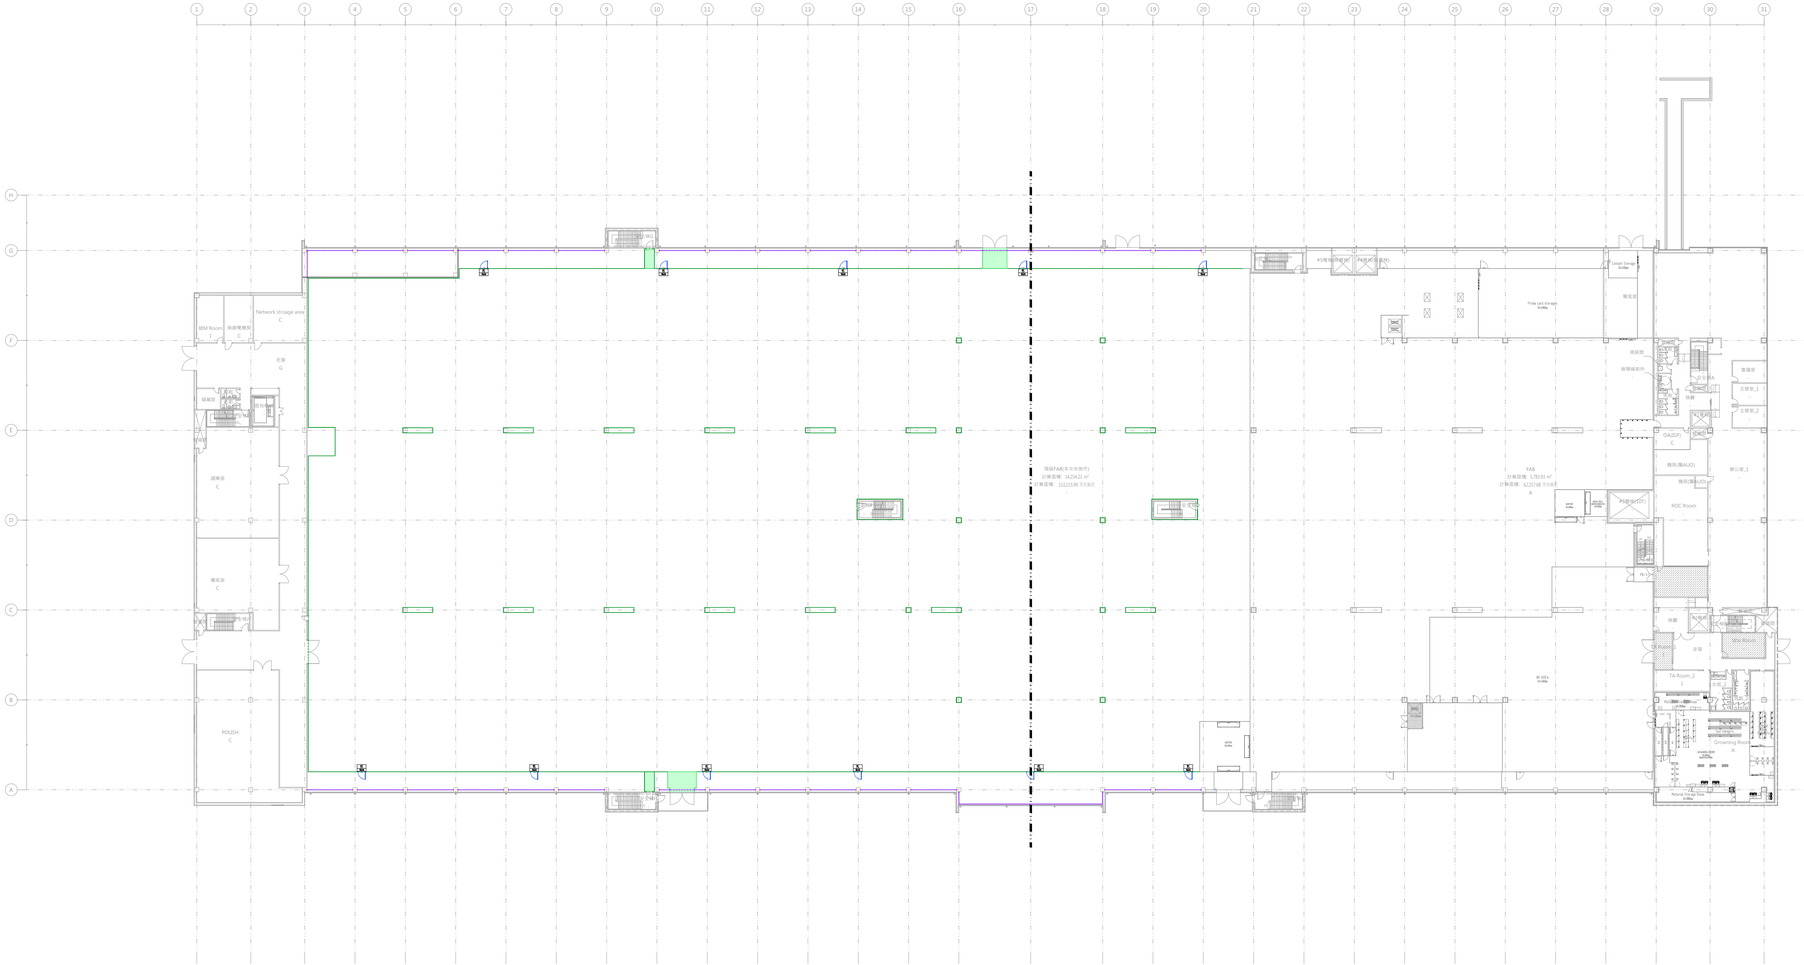


圖例說明

SYMBOL 圖例		MATERIAL 材料名稱	耐燃等級	WALL HEIGHT 高度 (m)
	Ps1	CLEANROOM WALL-ALUMINUM HONEYCOMB CORE, SINGLE SIDED ANTI-STATIC - 12mm† 蜂巢鋁合屬庫板牆，單面抗靜電	耐燃一級	4.5/2.8
	Pd2	CLEANROOM WALL-ALUMINUM HONEYCOMB CORE, DOUBLE SIDED ANTI-STATIC - 46mm† 蜂巢鋁合屬庫板牆，雙面抗靜電	耐燃一級	4.5 2.8
	P3	CLEANROOM WALL-ALUMINUM HONEYCOMB CORE, - H-TYPE(46mm†) 蜂巢鋁合屬庫板牆	耐燃一級	-
	Ps4	CLEANROOM WALL-ALUMINUM HONEYCOMB CORE, SINGLE SIDED - H-TYPE(46mm†) 蜂巢鋁合屬庫板牆，單面抗靜電	耐燃一級	-
	R1	ROCKWOOL WALL- 50mm† 岩棉金屬隔間分間牆 (50mm†)	防火一小時	8.5
	Rs1	ROCKWOOL WALL - 50mm† SINGLE SIDED ANTI-STATIC - 100mm† 岩棉金屬隔間分間牆 (50mm†)，單面抗靜電	防火一小時	-
	R2	ROCKWOOL WALL - 100mm† 岩棉金屬隔間分間牆 (100mm†)	防火二小時	-
	Rs2	ROCKWOOL WALL SINGLE SIDED ANTI-STATIC - 100mm† 岩棉金屬隔間分間牆 (100mm†)，單面抗靜電	防火二小時	-
	Rd2	ROCKWOOL WALL DOUBLE SIDED ANTI-STATIC - 100mm† 岩棉金屬隔間分間牆 (100mm†)，雙面抗靜電	防火二小時	-
	D2	STEEL PANEL WITH HVAC EQUIPMENT & RETRUN AIR SHAFT 鐵皮隔間牆	不燃	8.5

EQUIPMENT SYMBOL & LEGEND

SYMBOL	DESCRIPTION	QT'Y	CR	-	-	TOTAL	REMARK
LAD	LADDER (UP TO CEILING), H=2.8m CEILING MAINTAIN DOOR FOR LADDER (0.7m x 0.7m)	CONTRACT	-	-	-	-	
		CONST.	-	-	-	-	
	HONEYCOMB PARTITION WITH CEILING	CONTRACT	-	-	-	-	
		CONST.	-	-	-	-	
	WINDOW 800Wx1000H(mm) (in clean room interior shall no less than 50%)	CONTRACT	-	-	-	-	
		CONST.	-	-	-	-	

DOOR SYMBOL & LEGEND

NO.	SYMBOL	DESCRIPTION TYPE / SIZE(CM)	QT'Y	CR	-	-	TOTAL	REMARK
D W×H		DOUBLE WING DOOR, WITH GLAZING						
		-	CONTRACT	-	-	-	-	
			CONST.	-	-	-	-	
		240W x 240H	CONTRACT	-	-	-	-	
			CONST.	-	-	-	-	
		210W x 200H	CONTRACT	-	-	-	-	
			CONST.	-	-	-	-	
		150W x 240H	CONTRACT	-	-	-	-	
			CONST.	-	-	-	-	
FAU W×H		ROLLING DOOR, WITH GLAZING						
		300W x 300H	CONTRACT	-	-	-	-	
			CONST.	-	-	-	-	
		-	CONTRACT	-	-	-	-	
			CONST.	-	-	-	-	
AS W×H		SINGLE SLIDING DOOR, WITH GLAZING						
		165W x 250H	CONTRACT	-	-	-	-	
			CONST.	-	-	-	-	
		120W x 240H	CONTRACT	-	-	-	-	
			CONST.	-	-	-	-	
S W×H		SINGLE WING DOOR, WITH GLAZING						
		100W x 240H	CONTRACT	-	-	-	-	
			CONST.	-	-	-	-	
		-	CONTRACT	-	-	-	-	
			CONST.	-	-	-	-	
MS W×H		SINGLE WING DOOR (圓型拉環鎖 + 輔助鎖)						
		130W x 240H	CONTRACT	-	-	-	-	
			CONST.	-	-	-	-	
		80W x 240H	CONTRACT	-	-	-	-	
			CONST.	-	-	-	-	
		65W x 180H	CONTRACT	-	-	-	-	
			CONST.	-	-	-	-	

OWNER / DEVELOPER

micron

ARCHITECTURAL CONSULTANT

JJP ARCHITECTS & PLANNERS 潘冀聯合建築師

CIVIL & STRUCTURAL CONSULTANT

TEAM 群策工程股份有限公司


MECHANICAL & ELECTRICAL CONSULTANT & CONTRACTOR

UIS United Integrated Services 漢唐集成股份有限公司

SUB-CONTRACTOR

PROJECT ADDRESS

KEY PLAN

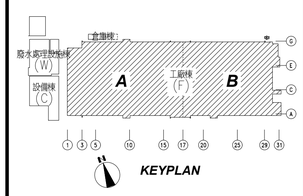

REV	DATE	DESCRIPTION	ISSUED BY
A	2025/01/02	REVIEW Drawing	

Revisions

PROJECT TITLE

Micron Falcon A Project (200K)

PROJECT PHASE

Concept Design

DRAWING TITLE

FLOOR PLAN -
PARTITION SYSTEM
FAB LEVEL 30
(OVERALL)

DESIGNED : YEATS CHU	DRAWN : YEATS CHU	CHECKED : C.S.HU	
DATE : 2024/11/20	JOB NO. :	SCALE : 1:500	

DRAWING NO. DE_F1_FAB_B001_B_PRTN_2L30-00 REV 0

SHEET: SIZE A1