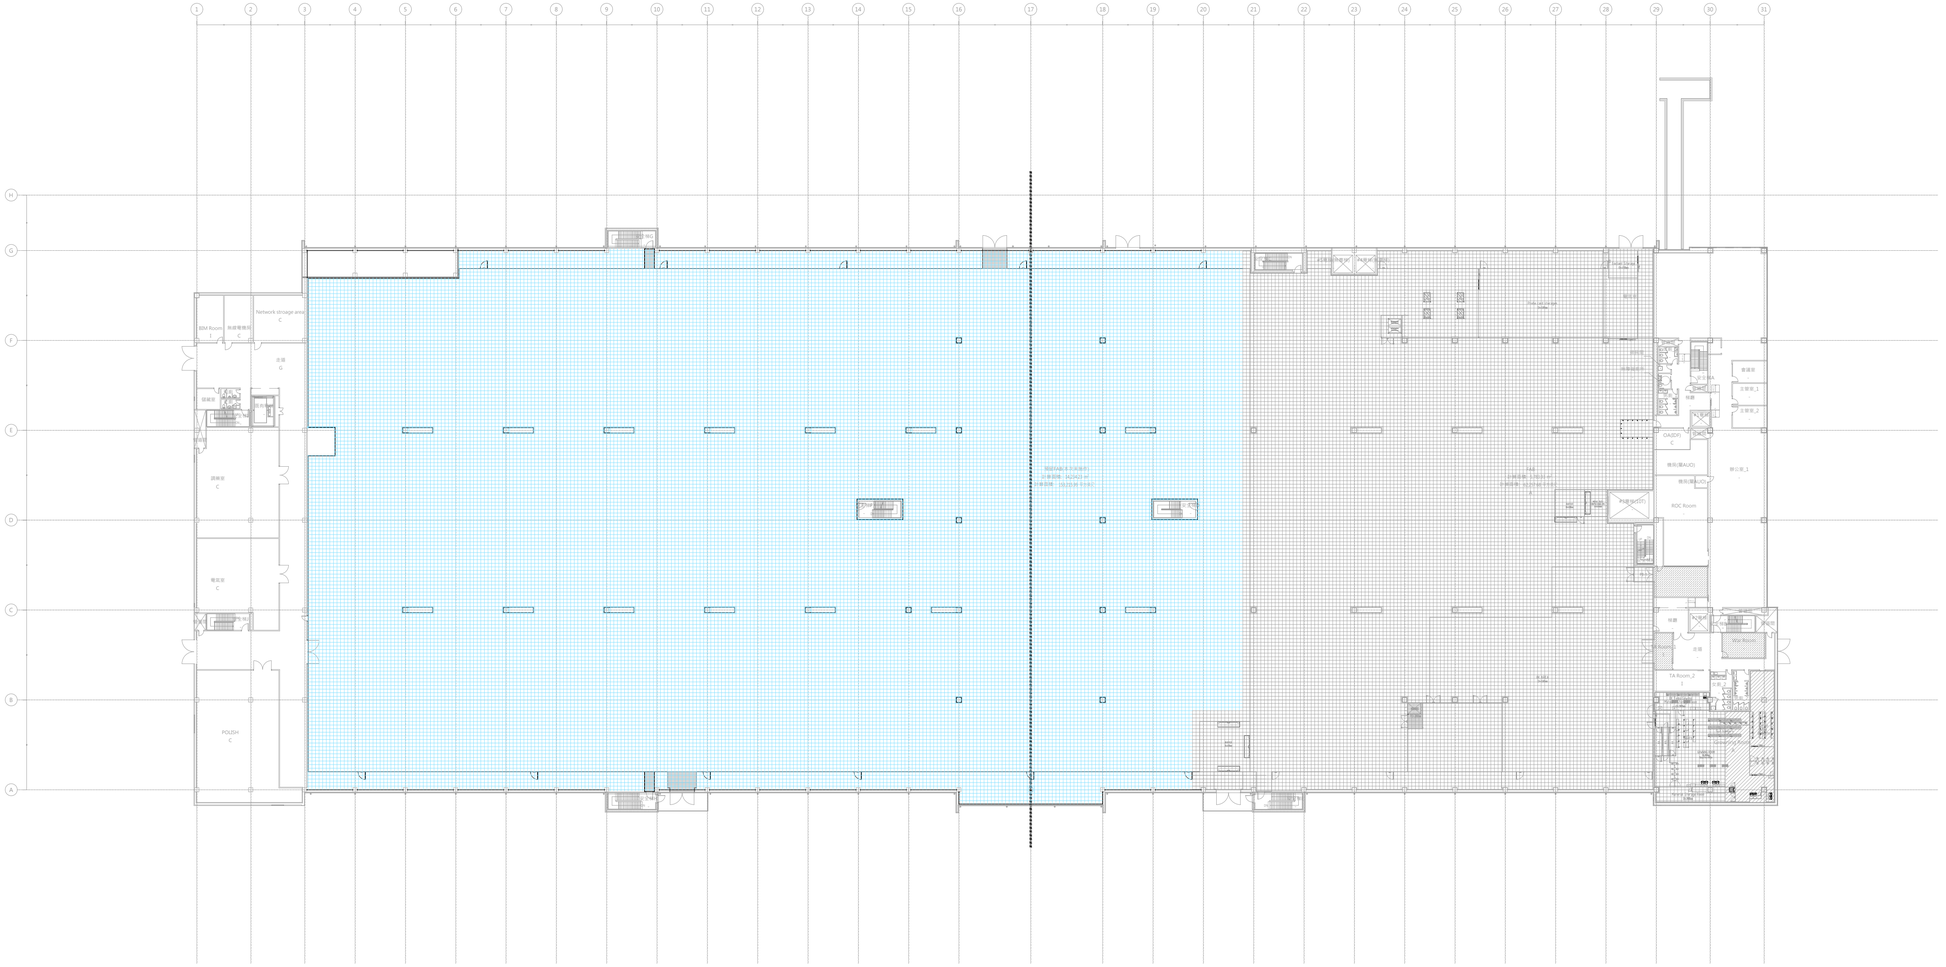

EQUIPMENT SYMBOL & LEGEND

SYMBOL	DESCRIPTION		QTY CR	-	- -			TOTAL	REMARK
	RAISED FLOOR 60x60cm, RH=20cm (全區使用TS00型)	CONTRACT	-	-	-	-	-	-	
		CONST.	-	-	-	-	-	-	
	RAISED FLOOR - MOVE-IN PATH 60x60cm, RH=20cm	CONTRACT	-	-	-	-	-	-	
		CONST.	-	-	-	-	-	-	
	RAISED FLOOR - PERFORATED PANELS, 60x60cm	CONTRACT	-	-	-	-	-	-	全面積 45%
		CONST.	-	-	-	-	-	-	
		CONTRACT	-	-	-	-	-	-	全面積 -
		CONST.	8,770	-	-	-	-	-	
	PVC CONDUCTIVE TILE, 2.0mmt	CONTRACT	-	-	-	-	-	-	
		CONST.	-	-	-	-	-	-	
	PVC TILE, 1.5mmt	CONTRACT	-	-	-	-	-	-	
		CONST.	-	-	-	-	-	-	
	GRATING	CONTRACT	-	-	-	-	-	-	
		CONST.	-	-	-	-	-	-	
	STEEL SHEET (導電處理)	CONTRACT	-	-	-	-	-	-	
		CONST.	-	-	-	-	-	-	
	DIVIDER , H=45cm (UNDER RAISED FLOOR)	CONTRACT	-	-	-	-	-	-	
		CONST.	-	-	-	-	-	-	
	SAFETY RAILING , H=1.2m	CONTRACT	-	-	-	-	-	-	
		CONST.	-	-	-	-	-	-	
		CONTRACT	-	-	-	-	-	-	
		CONST.	-	-	-	-	-	-	

OWNER / DEVELOPER

micron

ARCHITECTURAL CONSULTANT

JJP ARCHITECTS & PLANNERS 潘冀聯合建築師

CIVIL & STRUCTURAL CONSULTANT

TEAM 群策工程股份有限公司

MECHANICAL & ELECTRICAL CONSULTANT & CONTRACTOR

uis United Integrated Services 漢唐集成股份有限公司

SUB-CONTRACTOR

PROJECT ADDRESS

KEY PLAN

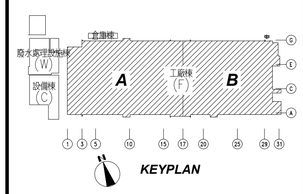

REV	DATE	DESCRIPTION	ISSUED BY
A	2025/01/02	REVIEW Drawing	

Revisions

PROJECT TITLE

Micron Falcon A Project (200K)

PROJECT PHASE

Concept Design

DRAWING TITLE

FLOOR PLAN -
FLOOR SYSTEM
FAB LEVEL 30
(OVERALL)

DESIGNED :	YEATS CHU	DRAWN :	YEATS CHU	CHECKED :	C.S.HU
DATE :	2024/11/20	JOB NO. :		SCALE :	1:500

DRAWING NO. DE_F1_FAB_B001_B_RAFL_2L30-00

REV 0

SHEET:

SIZE A1