
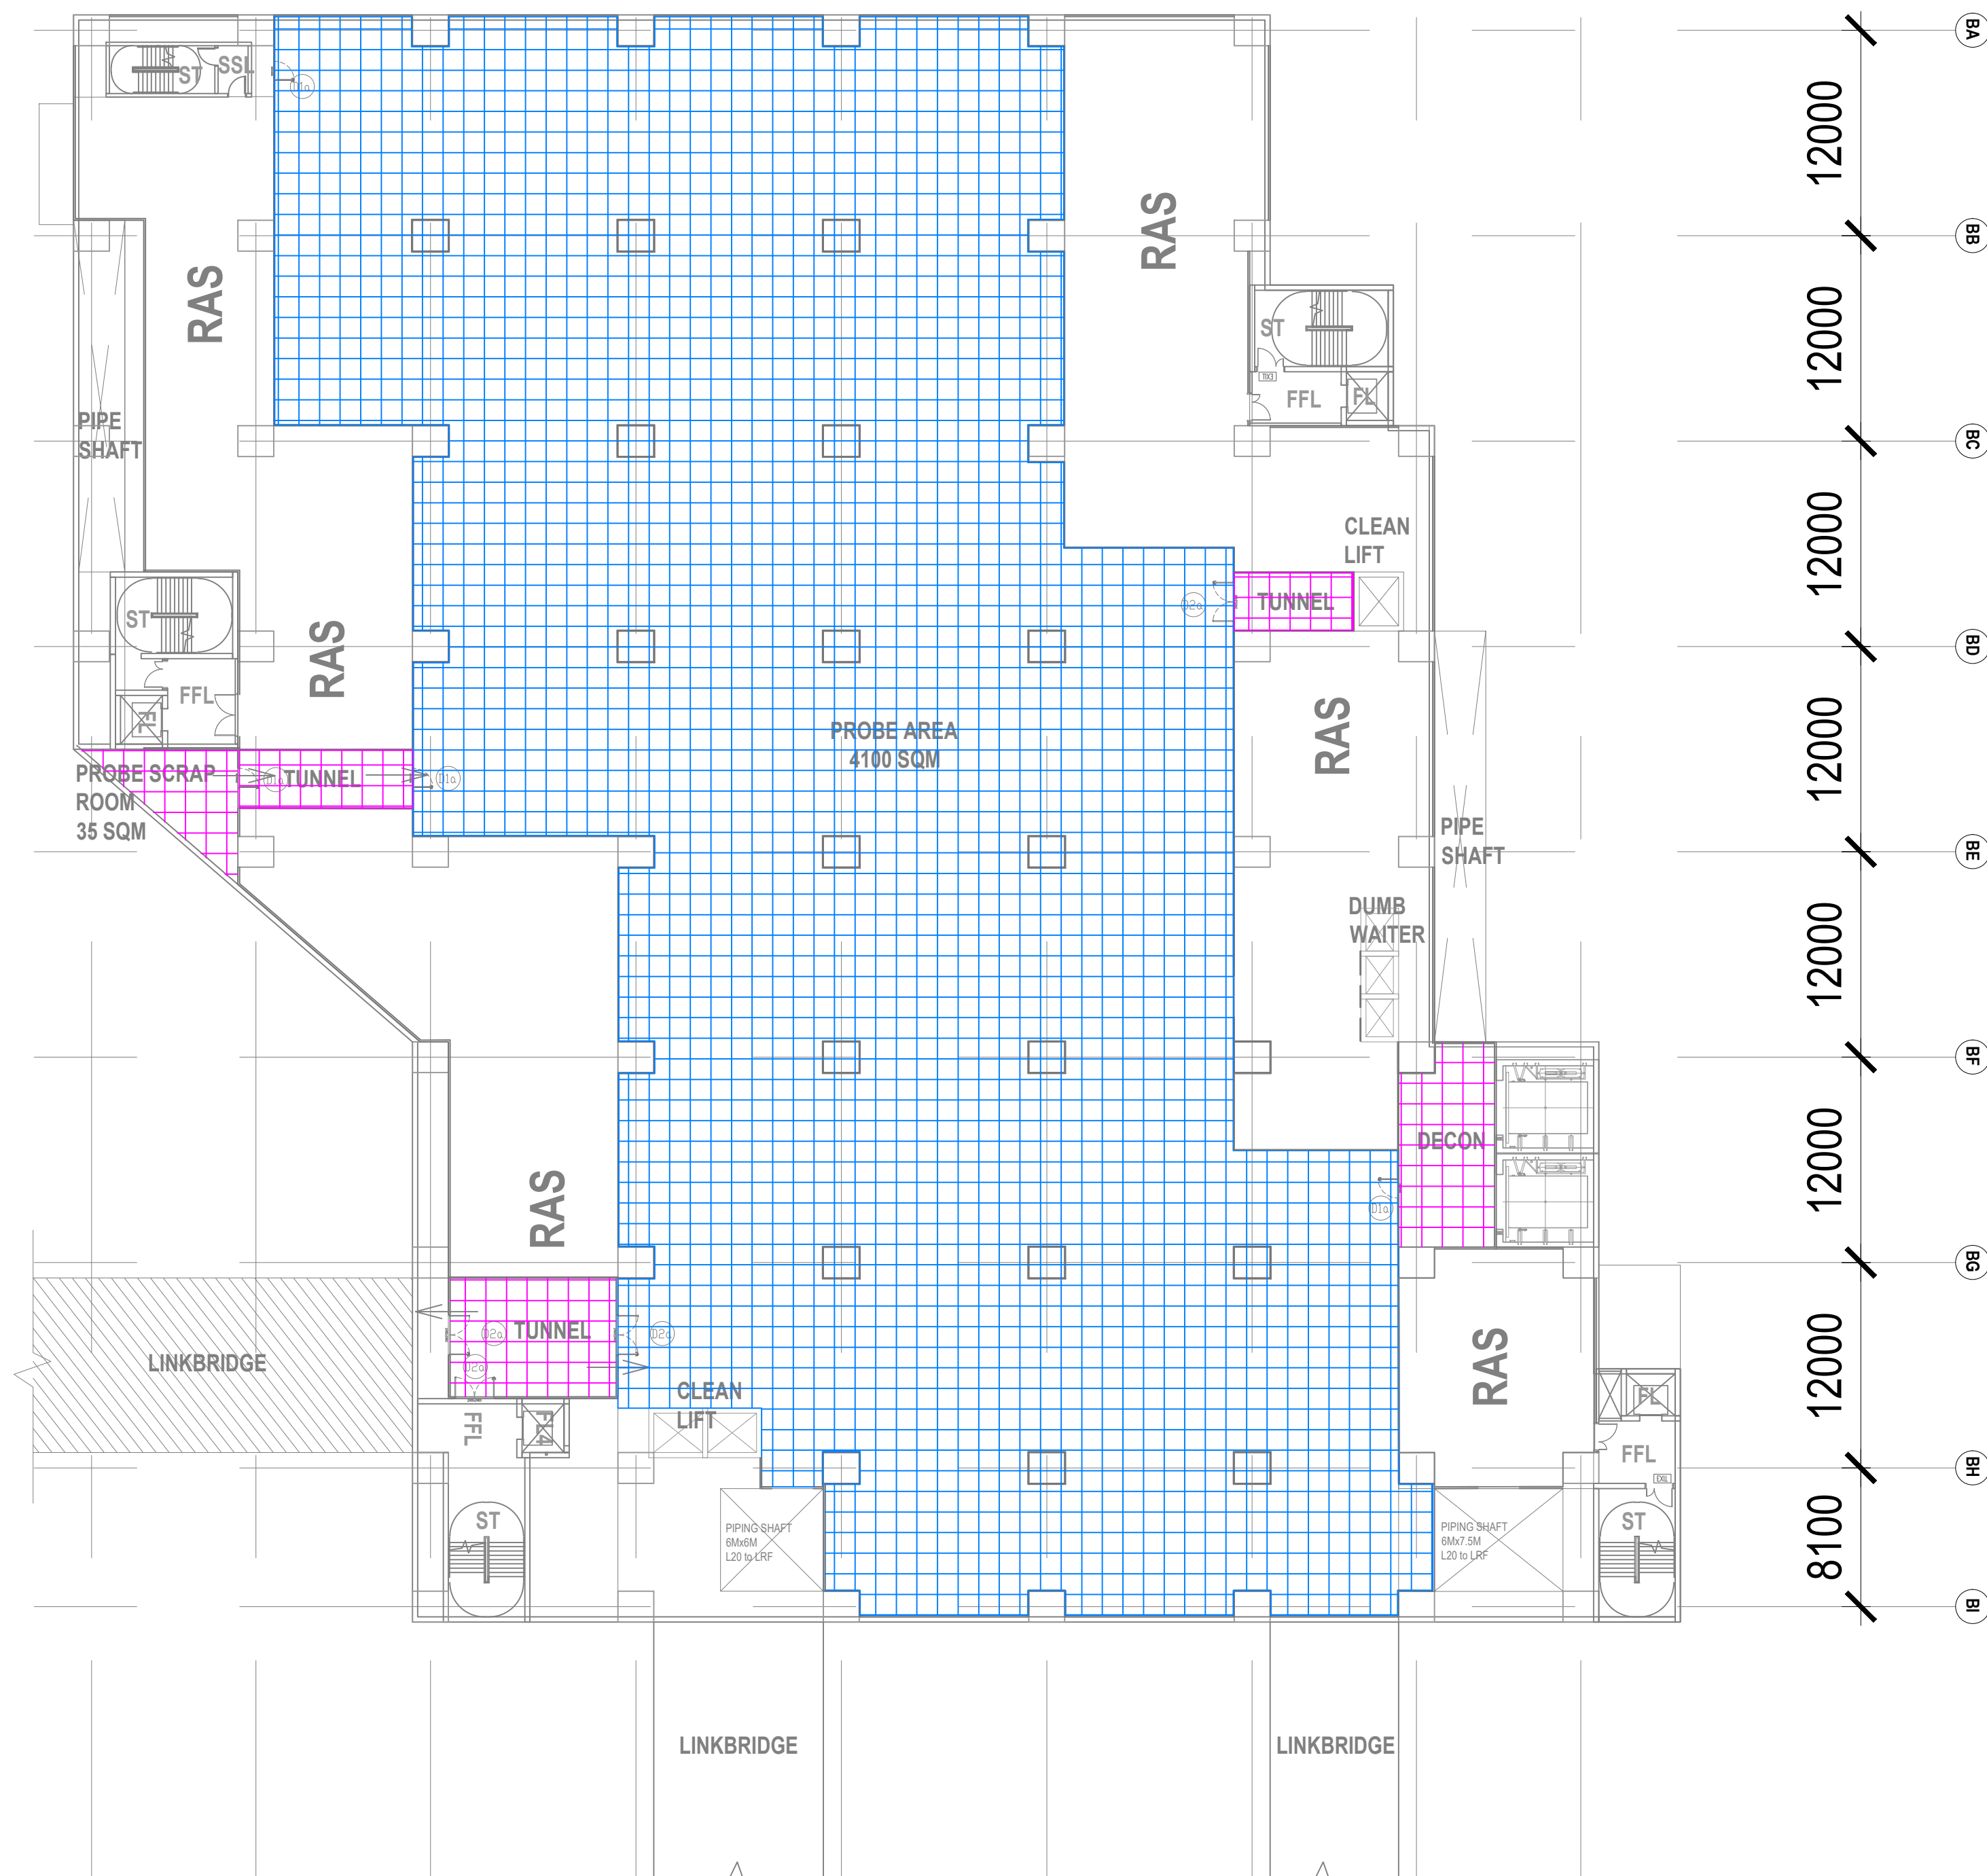


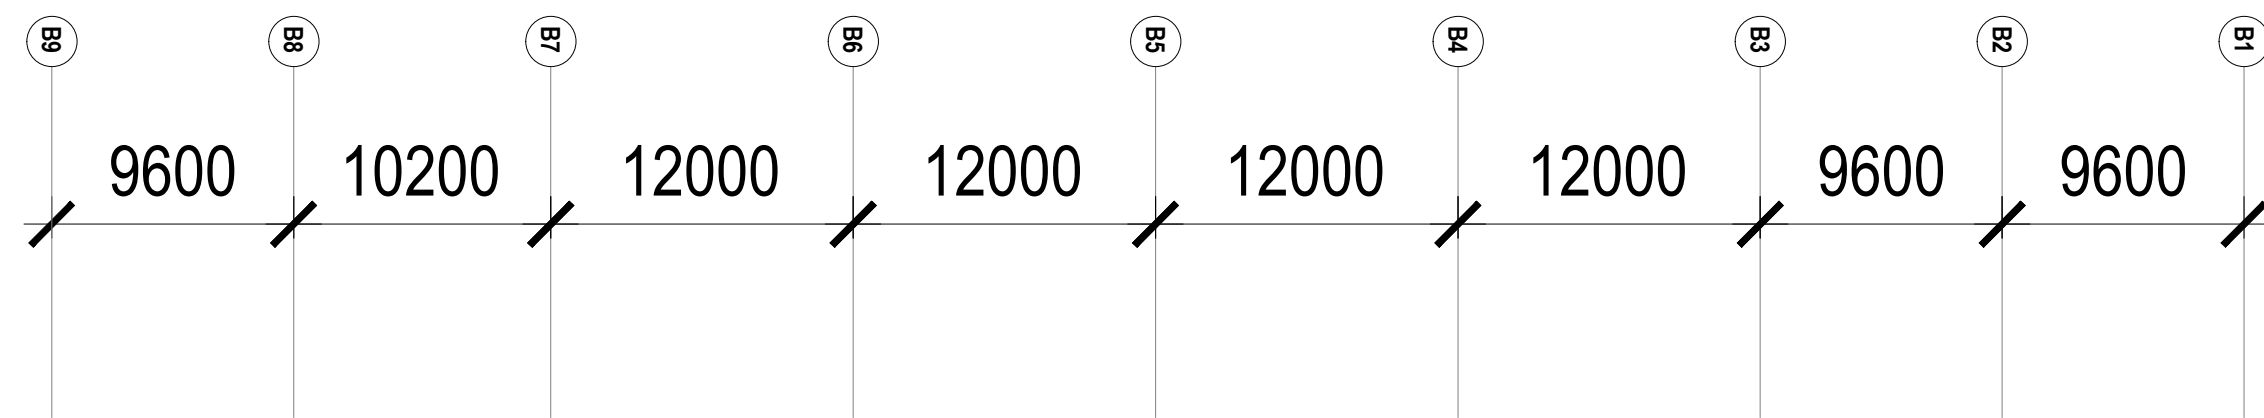

F10E2 L30, L40, L50, L70 ,L80 ,L100 CEILING LAYOUT SCALE 1:300

SYMBOL	DESCRIPTION
	CEILING GRID 天花板 1200mm x 1200mm CH=5000mm
	CEILING GRID 天花板 1200mm x 1200mm CH=3000mm

OWNER / DEVELOPER

micron™

ARCHITECTURAL CONSULTANT

CIVIL & STRUCTURAL CONSULTANT

MECHANICAL & ELECTRICAL CONSULTANT


DESIGN MANAGER

CTCI  CTCI Singapore Pte. Ltd.

PROJECT ADDRESS

North Coast Drive, Singapore

KEY PLAN

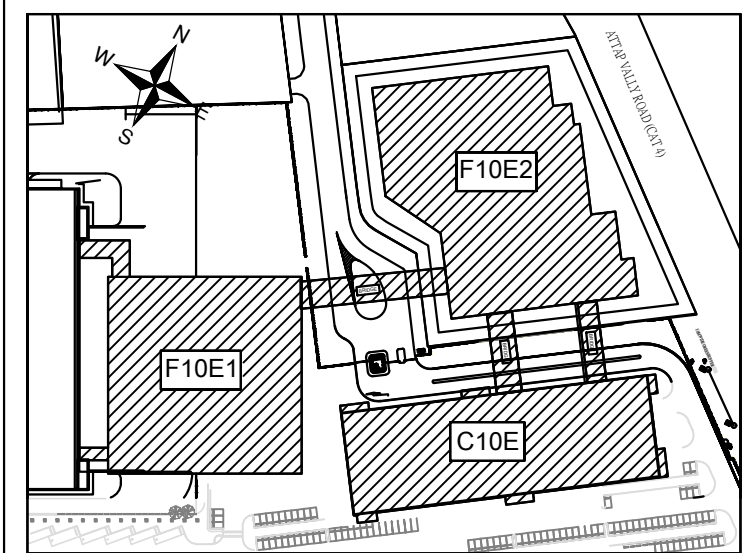

Secret
R3
Level

SHEET PURPOSE

[illegible]

PROJECT TITLE

Micron F10E Probe Project

PROJECT PHASE

A&E

DRAWING TITLE

Floor Plan - Ceiling Layout F10E2
L30, L40, L50, L70, L80, L100

DESIGNED :	設計者	DRAWN :	作者	CHECKED :	審圖員
DATE :	02/11/26	JOB NO. :		SCALE :	
Micro DRAWING NO.	F01-F10E-LAY-F10E2-00-K-120				REV
CTCI DRAWING NO.					0A
Reference Model					
CTCI			SHEET: 1 OF 1	SIZE A1	