



CONFIDENTIAL NOTICE: THE CONTENT OF THIS DOCUMENT IS EXCLUSIVE INFORMATION AND IS OWNED BY MICRON CORPORATION AND IS PROTECTED BY COPYRIGHT LAWS AND RELEVANT LEGISLATIONS. ONLY EMPLOYEES OF MICRON ARE ALLOWED TO ACCESS AND USE THIS SENSITIVE INFORMATION WITHIN THE WORK SCOPE UNDER THEIR SPECIFIC AND RESPECTIVE DUTIES AND OBLIGATIONS REQUIRED BY AGREEMENT WHICH IS NOT ALLOWED TO COPY, REPRODUCE, DISTRIBUTE PUBLICLY OR DISCLOSE IN WHATEVER MANNER TO ANY OTHER PARTY WITHOUT CTCI'S PRIOR AND WRITTEN CONSENT.

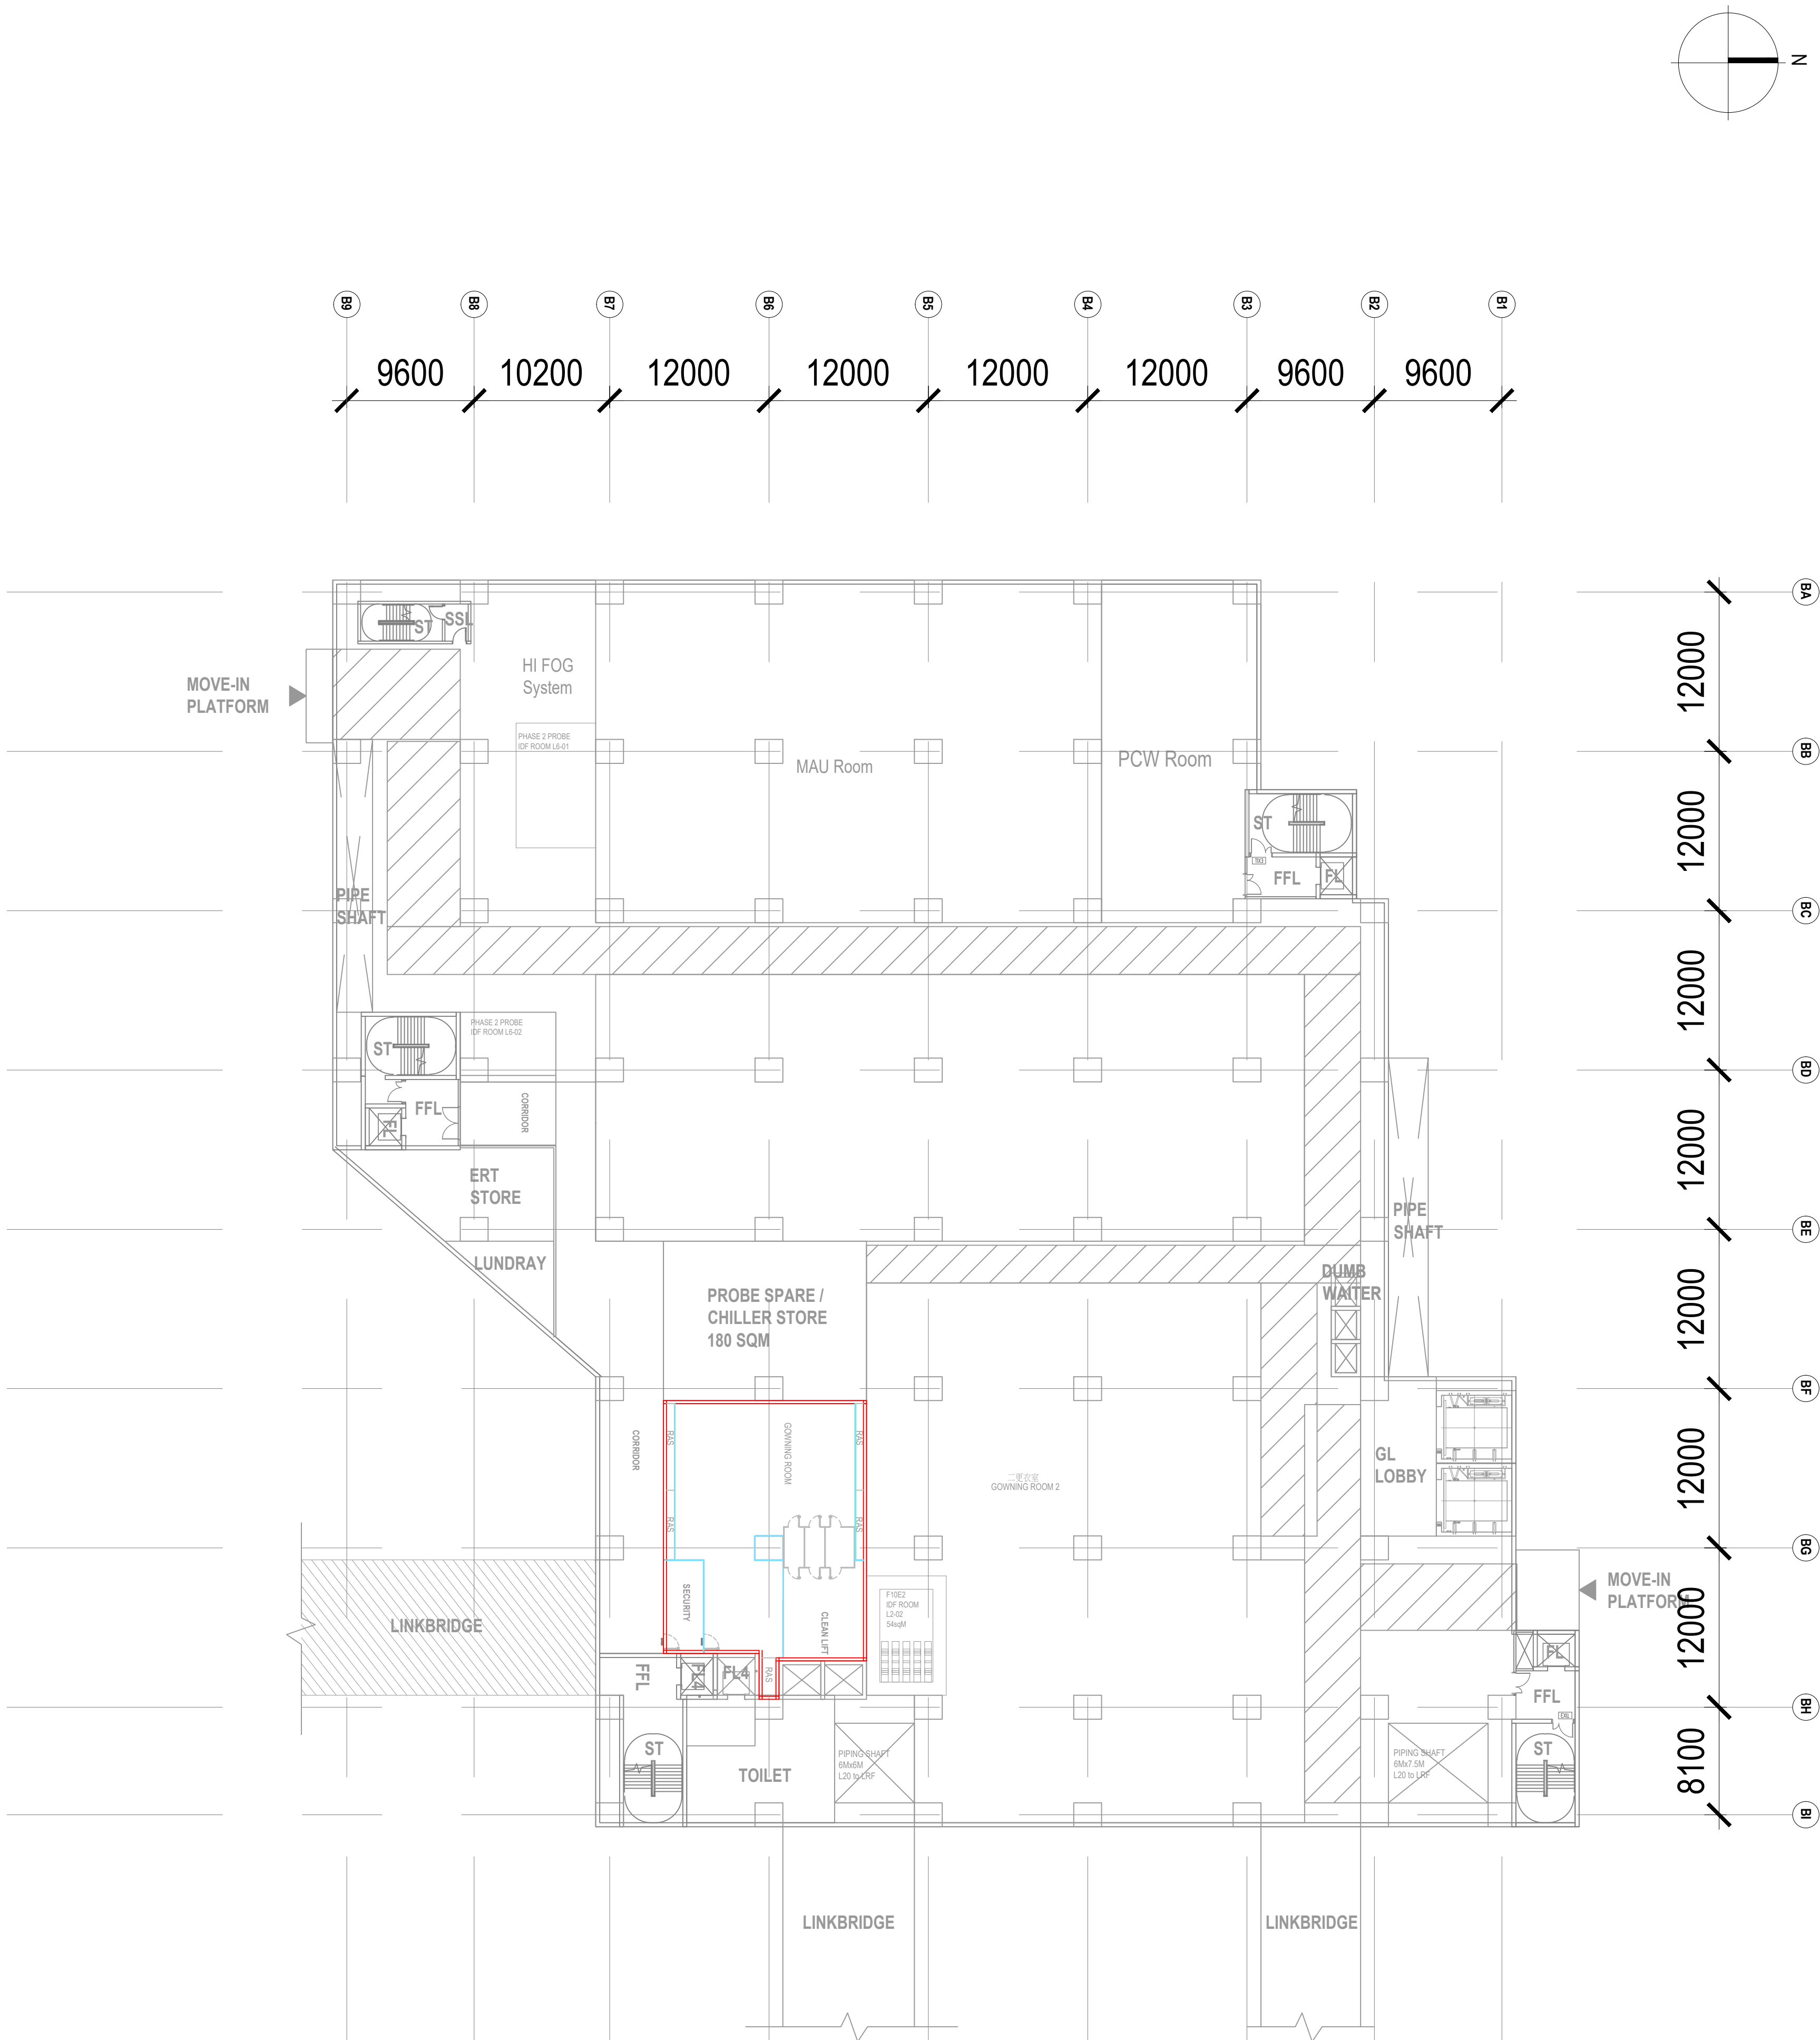

F10E2 L20 PARTITION LAYOUT SCALE 1:300

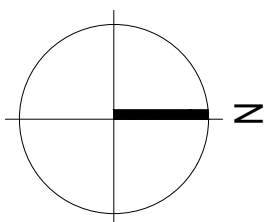

SYMBOL	DESCRIPTION
	2-HOUR FIRE-RATED ROCK WOOL PANEL PARTITION (t=100mm) SINGLE-SIDE ANTI-STATIC H=10000mm 防火二小時岩棉庫板隔間 (t=100mm) 單抗靜電 H=10000mm
	2-HOUR FIRE-RATED ROCK WOOL PANEL PARTITION (t=100mm) DOUBLE-SIDE ANTI-STATIC H=10000mm 防火二小時岩棉庫板隔間 (t=100mm) 雙面抗靜電 H=10000mm
	2-HOUR FIRE-RATED ROCK WOOL PANEL PARTITION (t=100mm) SINGLE-SIDE ANTI-STATIC H=3000mm 防火二小時岩棉庫板隔間 (t=100mm) 單抗靜電 H=3000mm
	ALUMINUM HONEYCOMB CLEANROOM PANEL PARTITION (t=50mm) DOUBLE-SIDE ANTI-STATIC H=5000mm 鋁蜂巢庫板隔間 (t=50mm) 雙面抗靜電 H=5000mm
	ALUMINUM HONEYCOMB CLEANROOM PANEL PARTITION (t=50mm) DOUBLE-SIDE ANTI-STATIC H=3000mm 鋁蜂巢庫板隔間 (t=50mm) 雙面抗靜電 H=3000mm
	ALUMINUM HONEYCOMB CLEANROOM PANEL PARTITION (t=50mm) SINGLE-SIDE ANTI-STATIC H=10000mm 鋁蜂巢庫板隔間 (t=50mm) 單抗靜電 H=10000mm
	RETURN AIR LOUVER 2500W x 2000H 回風百葉窗 2500W x 2000H

OWNER / DEVELOPER

ARCHITECTURAL CONSULTANT


CIVIL & STRUCTURAL CONSULTANT

MECHANICAL & ELECTRICAL CONSULTANT

DESIGN MANAGER

CTCI Singapore Pte. Ltd.

PROJECT ADDRESS
North Coast Drive, Singapore

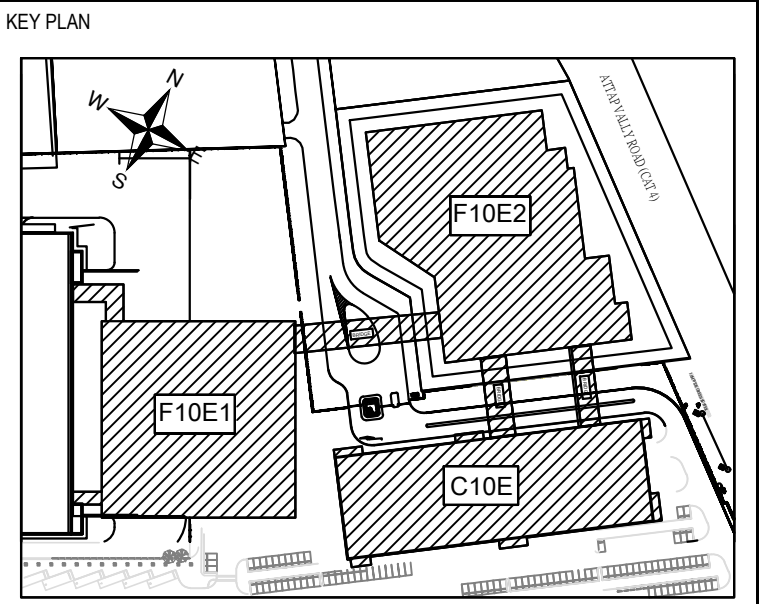

Secret
R3
Level

SHEET PURPOSE

REV	DATE	DESCRIPTION Revisions	ISSUED BY

PROJECT TITLE Micron F10E Probe Project			
PROJECT PHASE A&E			
DRAWING TITLE Floor Plan - Partition Wall Layout F10E2 L20			
DESIGNED : 設計者	DRAWN : 作者	CHECKED : 審圖員	
DATE : 02/11/26	JOB NO. :	SCALE :	
Micron DRAWING NO. : F01-F10E-LAY-F10E2-02-K-124			REV 0A
CTCI DRAWING NO. :			
Reference Model			
CTCI	SHEET: 1 OF 1	SIZE A1	