


PERMITAL NOTICE: THE CONTENT OF THIS DOCUMENT IS SENSITIVE INFORMATION MADE AND OWNED BY MICRON CORPORATION AND IS PROTECTED BY COPYRIGHT LAWS AND RELEVANT LAWS/REGULATIONS. ONLY EMPLOYEES OF MICRON ARE ALLOWED TO ACCESS AND USE THIS SENSITIVE INFORMATION WITHIN THE WORK SCOPE UNDER THEIR RESPECTIVE DUTIES AND OBLIGATIONS REQUIRED BY AGREEMENT WHICH IS NOT ALLOWED TO COPY, REPRODUCE, DISTRIBUTE, PUBLISH, OR DISCLOSE IN WHOLE OR IN PART TO ANY OTHER PARTY WITHOUT CTCTC PRIOR AND WRITTEN CONSENT.

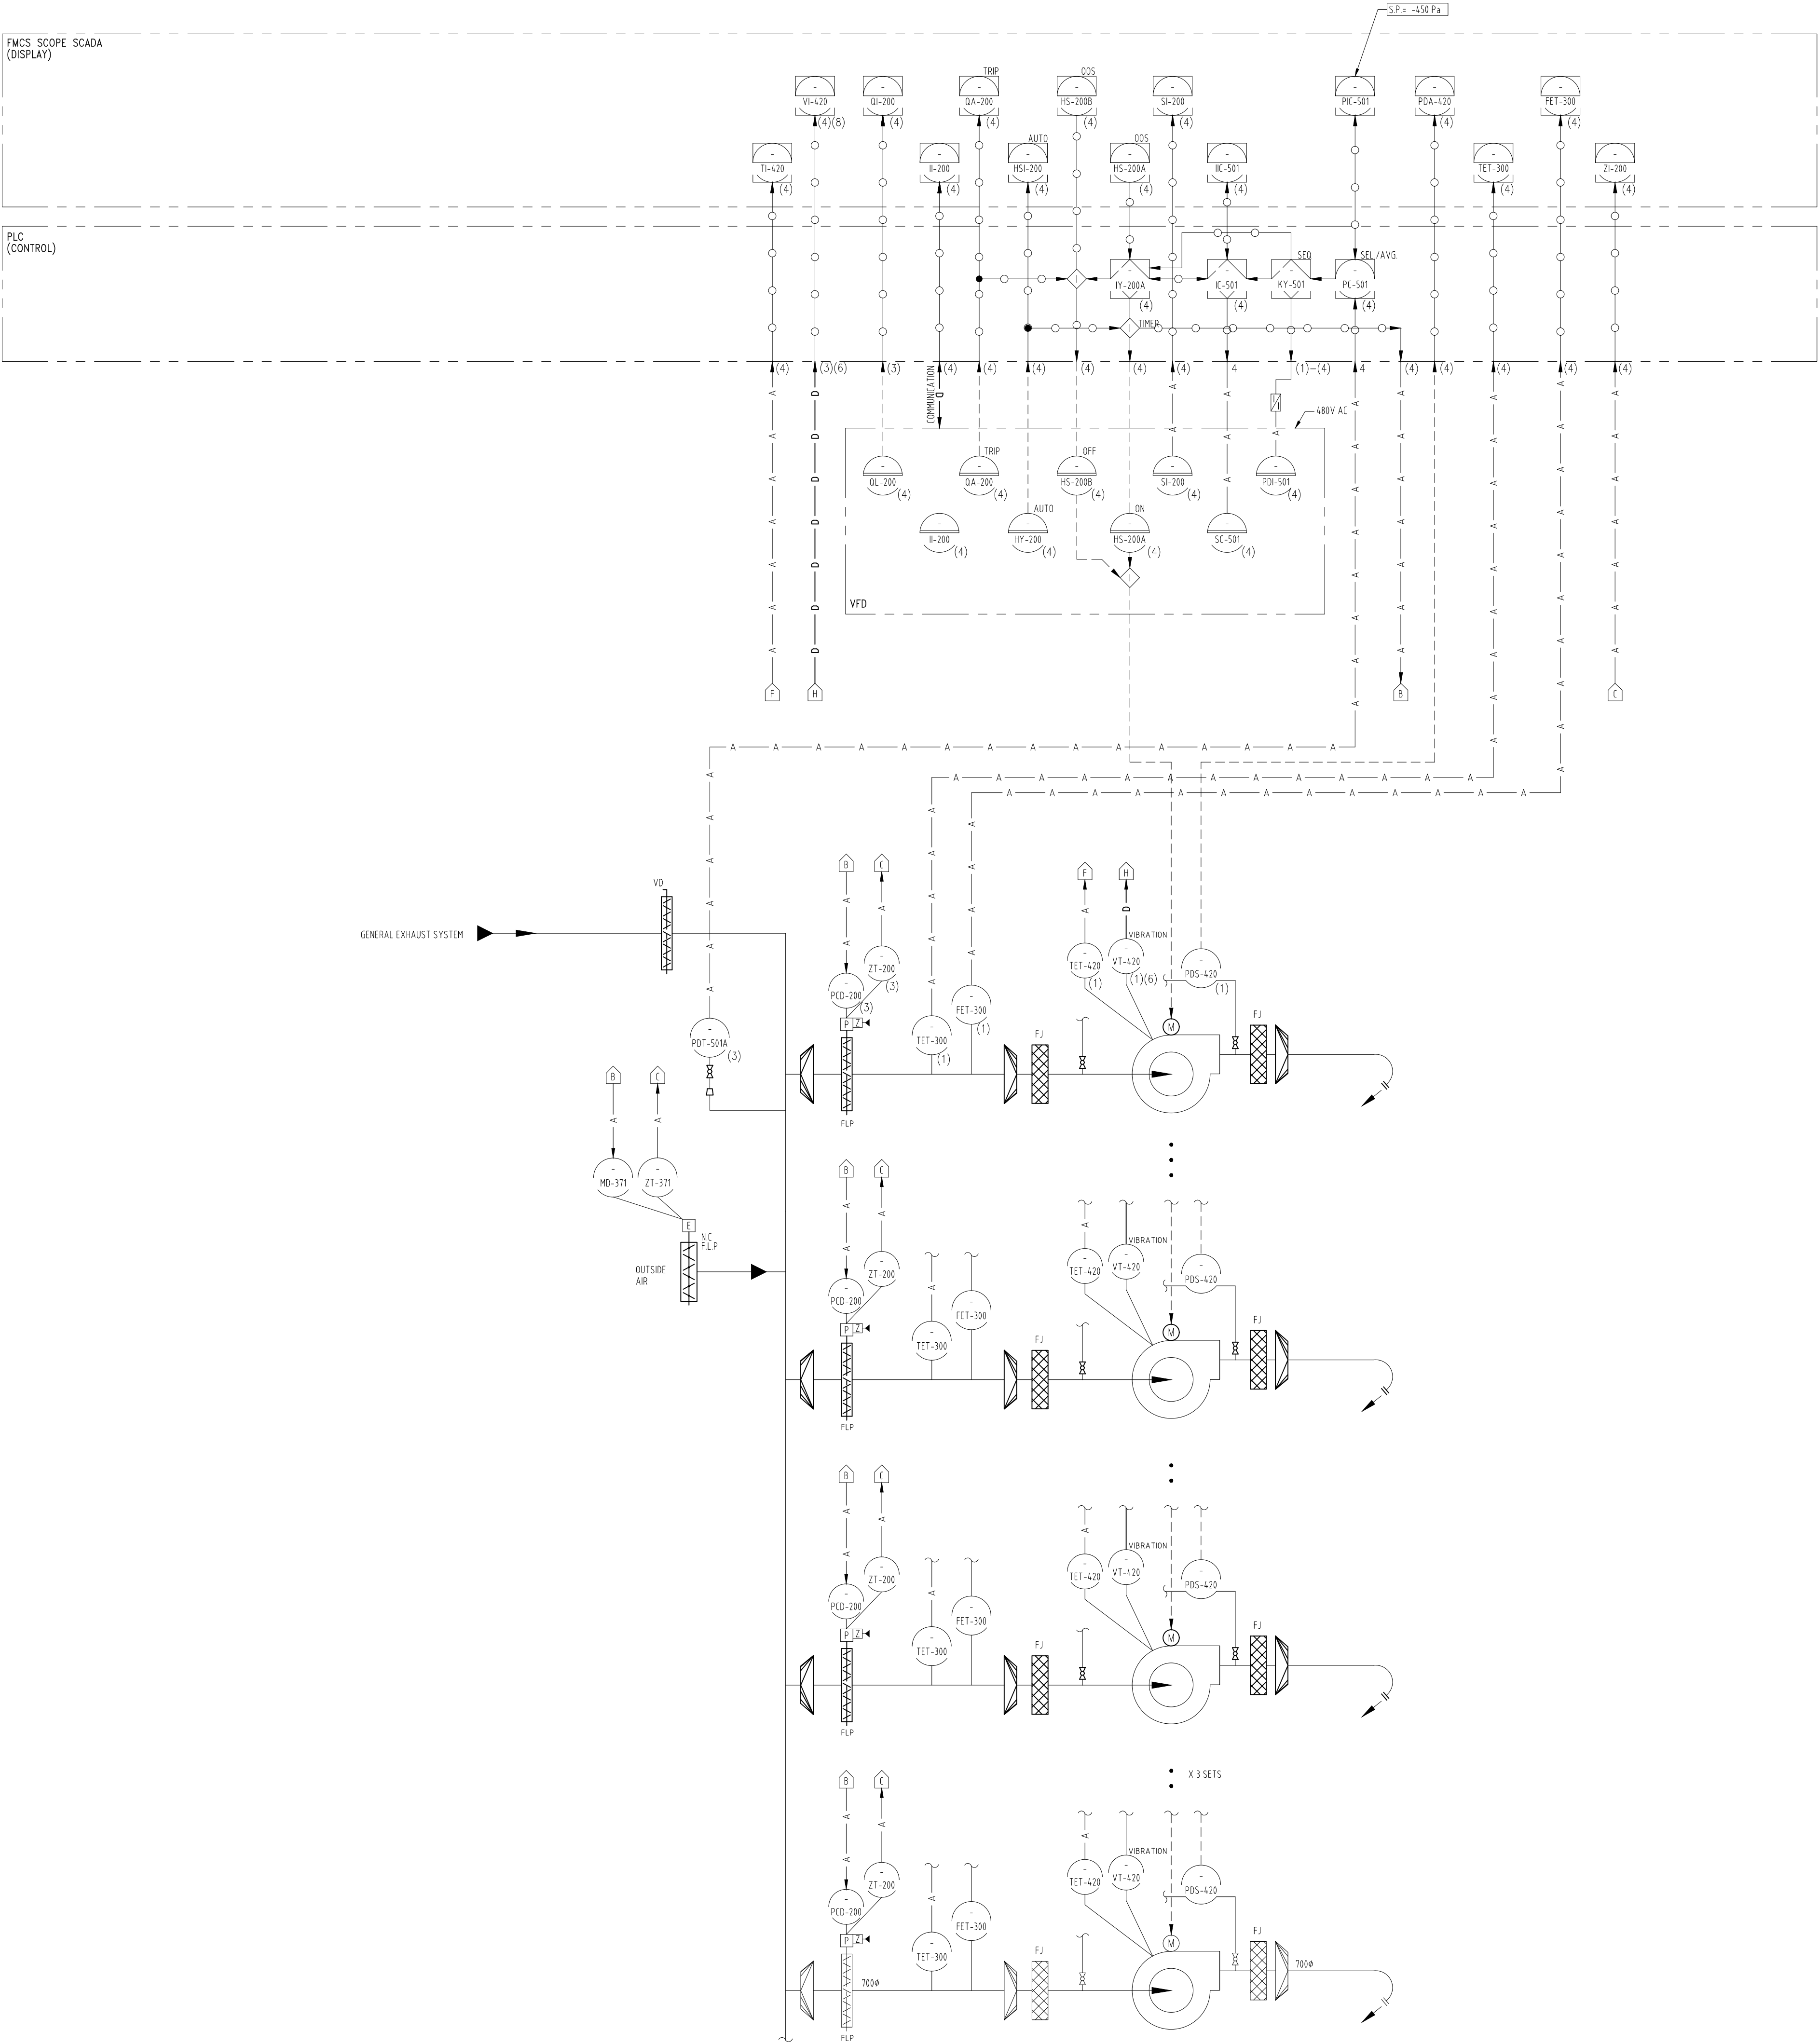

OWNER / DEVELOPER

ARCHITECTURAL CONSULTANT

CIVIL & STRUCTURAL CONSULTANT

MECHANICAL & ELECTRICAL CONSULTANT

DESIGN MANAGER

CTCI Singapore Pte. Ltd.

PROJECT ADDRESS
North Coast Drive, Singapore

KEY PLAN

Secret
R3
Level

FOR REVIEW

REV	DATE	DESCRIPTION Revisions	ISSUED BY

PROJECT TITLE

Micron F10E Probe Project

PROJECT PHASE

A&E

DRAWING TITLE

FIOW DIAGRAM
Exhasut Fan Control System P&ID

DESIGNED : 設計者	DRAWN : 作者	CHECKED : 審圖員
DATE : 02/12/20	JOB NO. :	SCALE :
Micron DRAWING NO. : F01-F10E-PFD-S0-00-K-110	REV	
CTCI DRAWING NO. :	A	
Reference Model		
CTCI	SHEET: 1 OF 1	SIZE A1