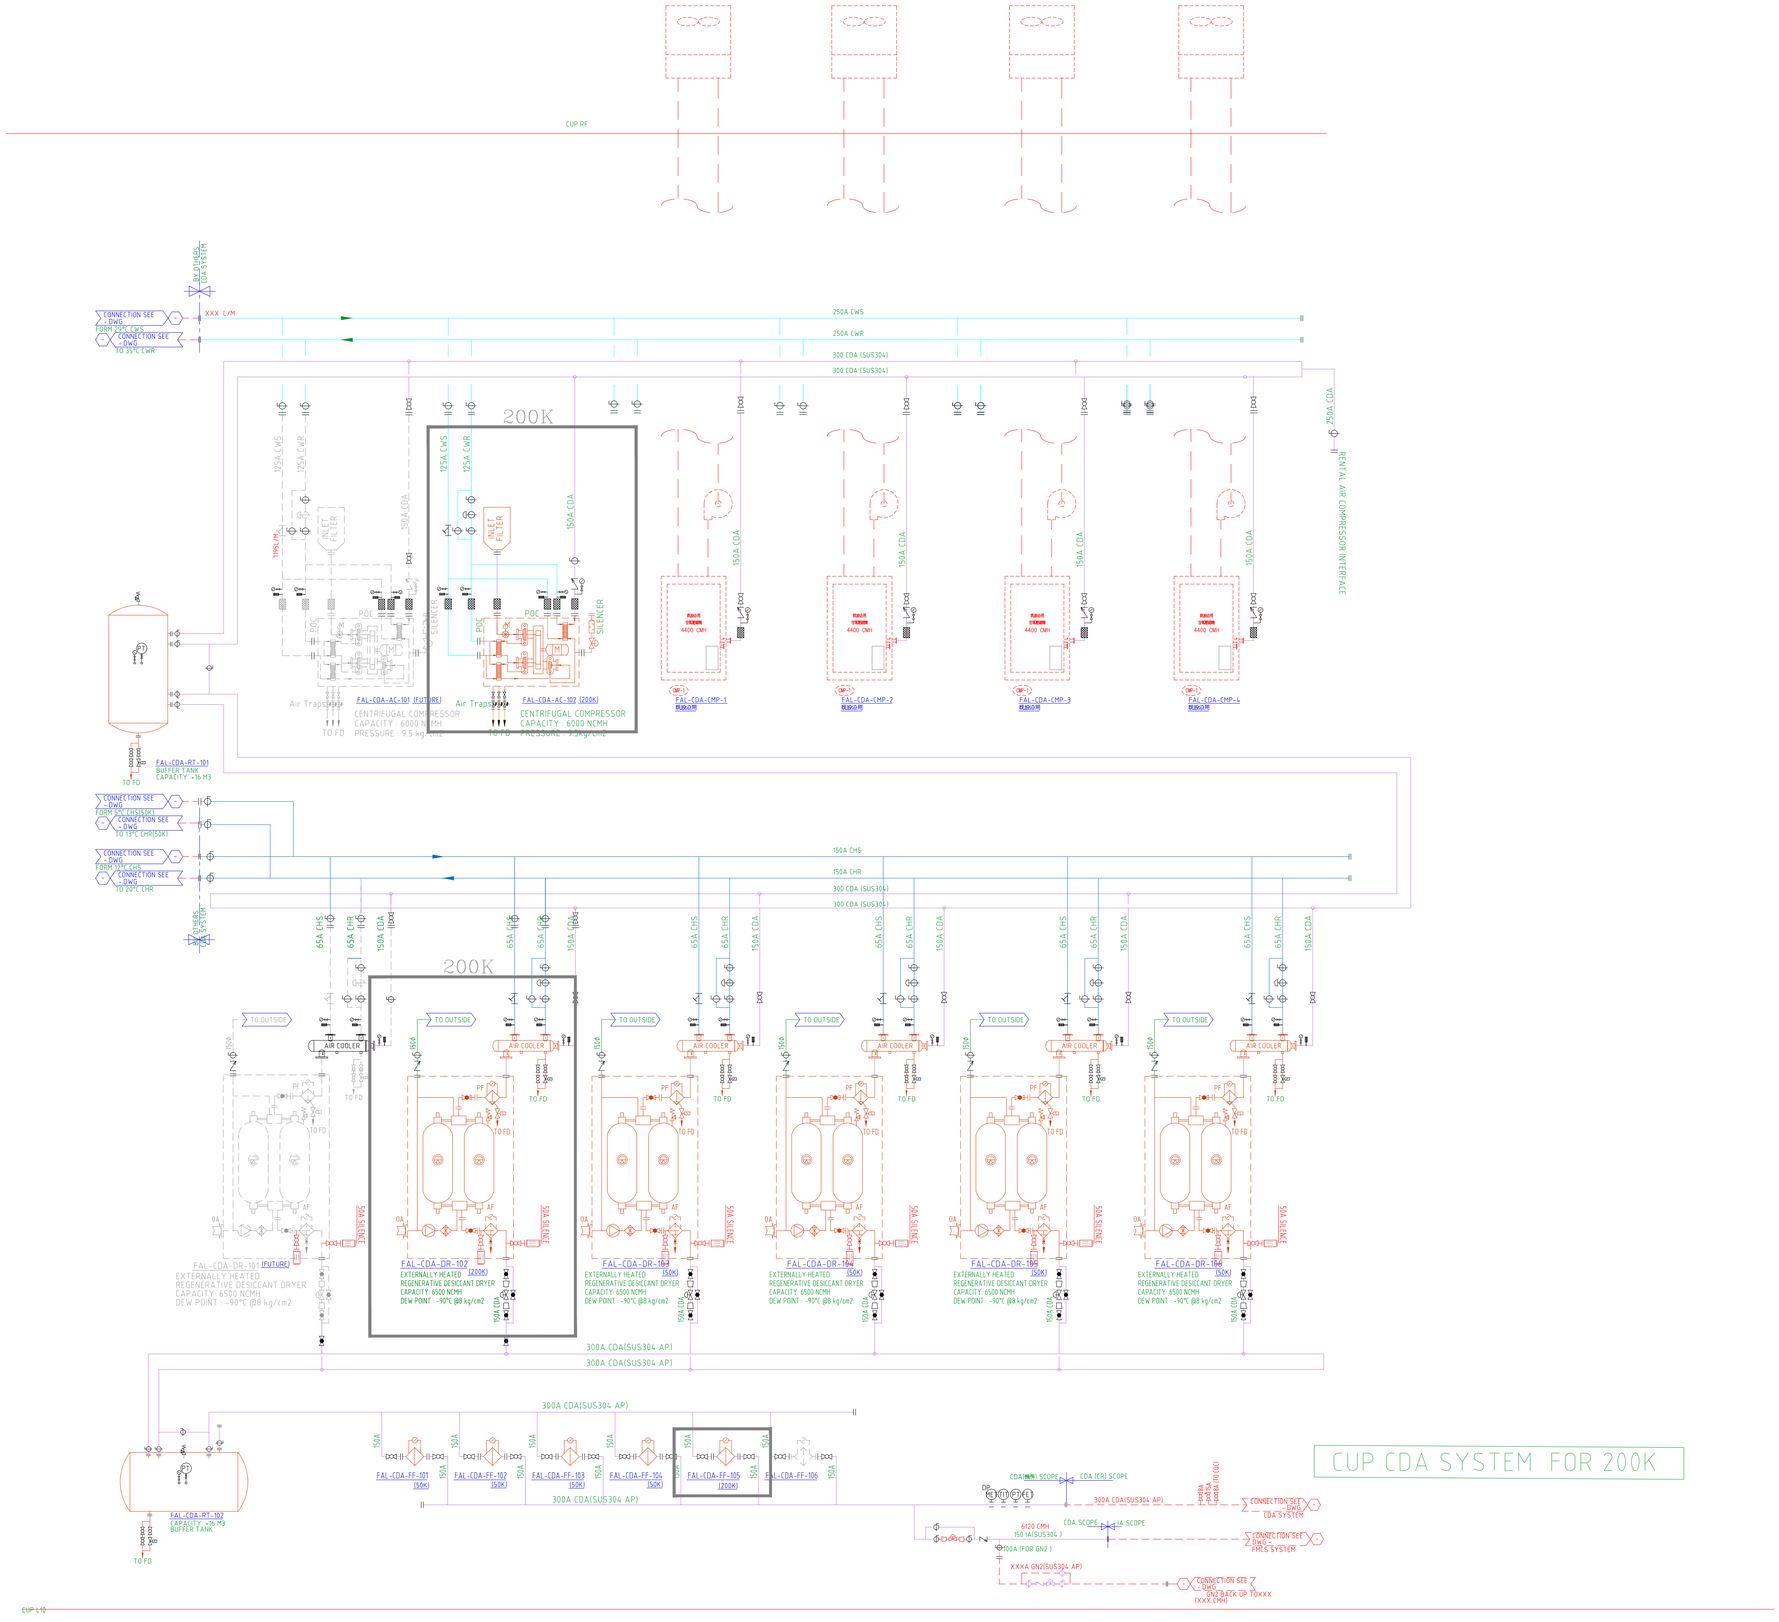

CUP CDA SYSTEM FOR 200K

說明:
離心式空壓機各台主管配合雙迴路配置主管,依現場配置基準.

OWNER / DEVELOPER

micron

ARCHITECTURAL CONSULTANT

JJP ARCHITECTS & PLANNERS 潘冀聯合建築師

CIVIL & STRUCTURAL CONSULTANT

TEAM 群策工程股份有限公司

MECHANICAL & ELECTRICAL CONSULTANT & CONTRACTOR

UIS United Integrated Services 漢唐集成股份有限公司

SUB-CONTRACTOR

PROJECT ADDRESS

KEY PLAN

REV	DATE	DESCRIPTION	ISSUED BY
A	2025/01/02	REVIEW Drawing	

Revisions

PROJECT TITLE

Micron Falcon A Project (200K)

PROJECT PHASE

Concept Design

DRAWING TITLE

SYSTEM DIAGRAM -
CDA SYSTEM
200K
-

DESIGNED : CHEN	DRAWN : CHEN	CHECKED : C.S.HU	
DATE : 2024/11/20	JOB NO. :	SCALE : N.T.S	

DRAWING NO. DE_F1_ALL_B0001_D_ACDA_6002-200K

REV 0

SHEET:

SIZE A1