


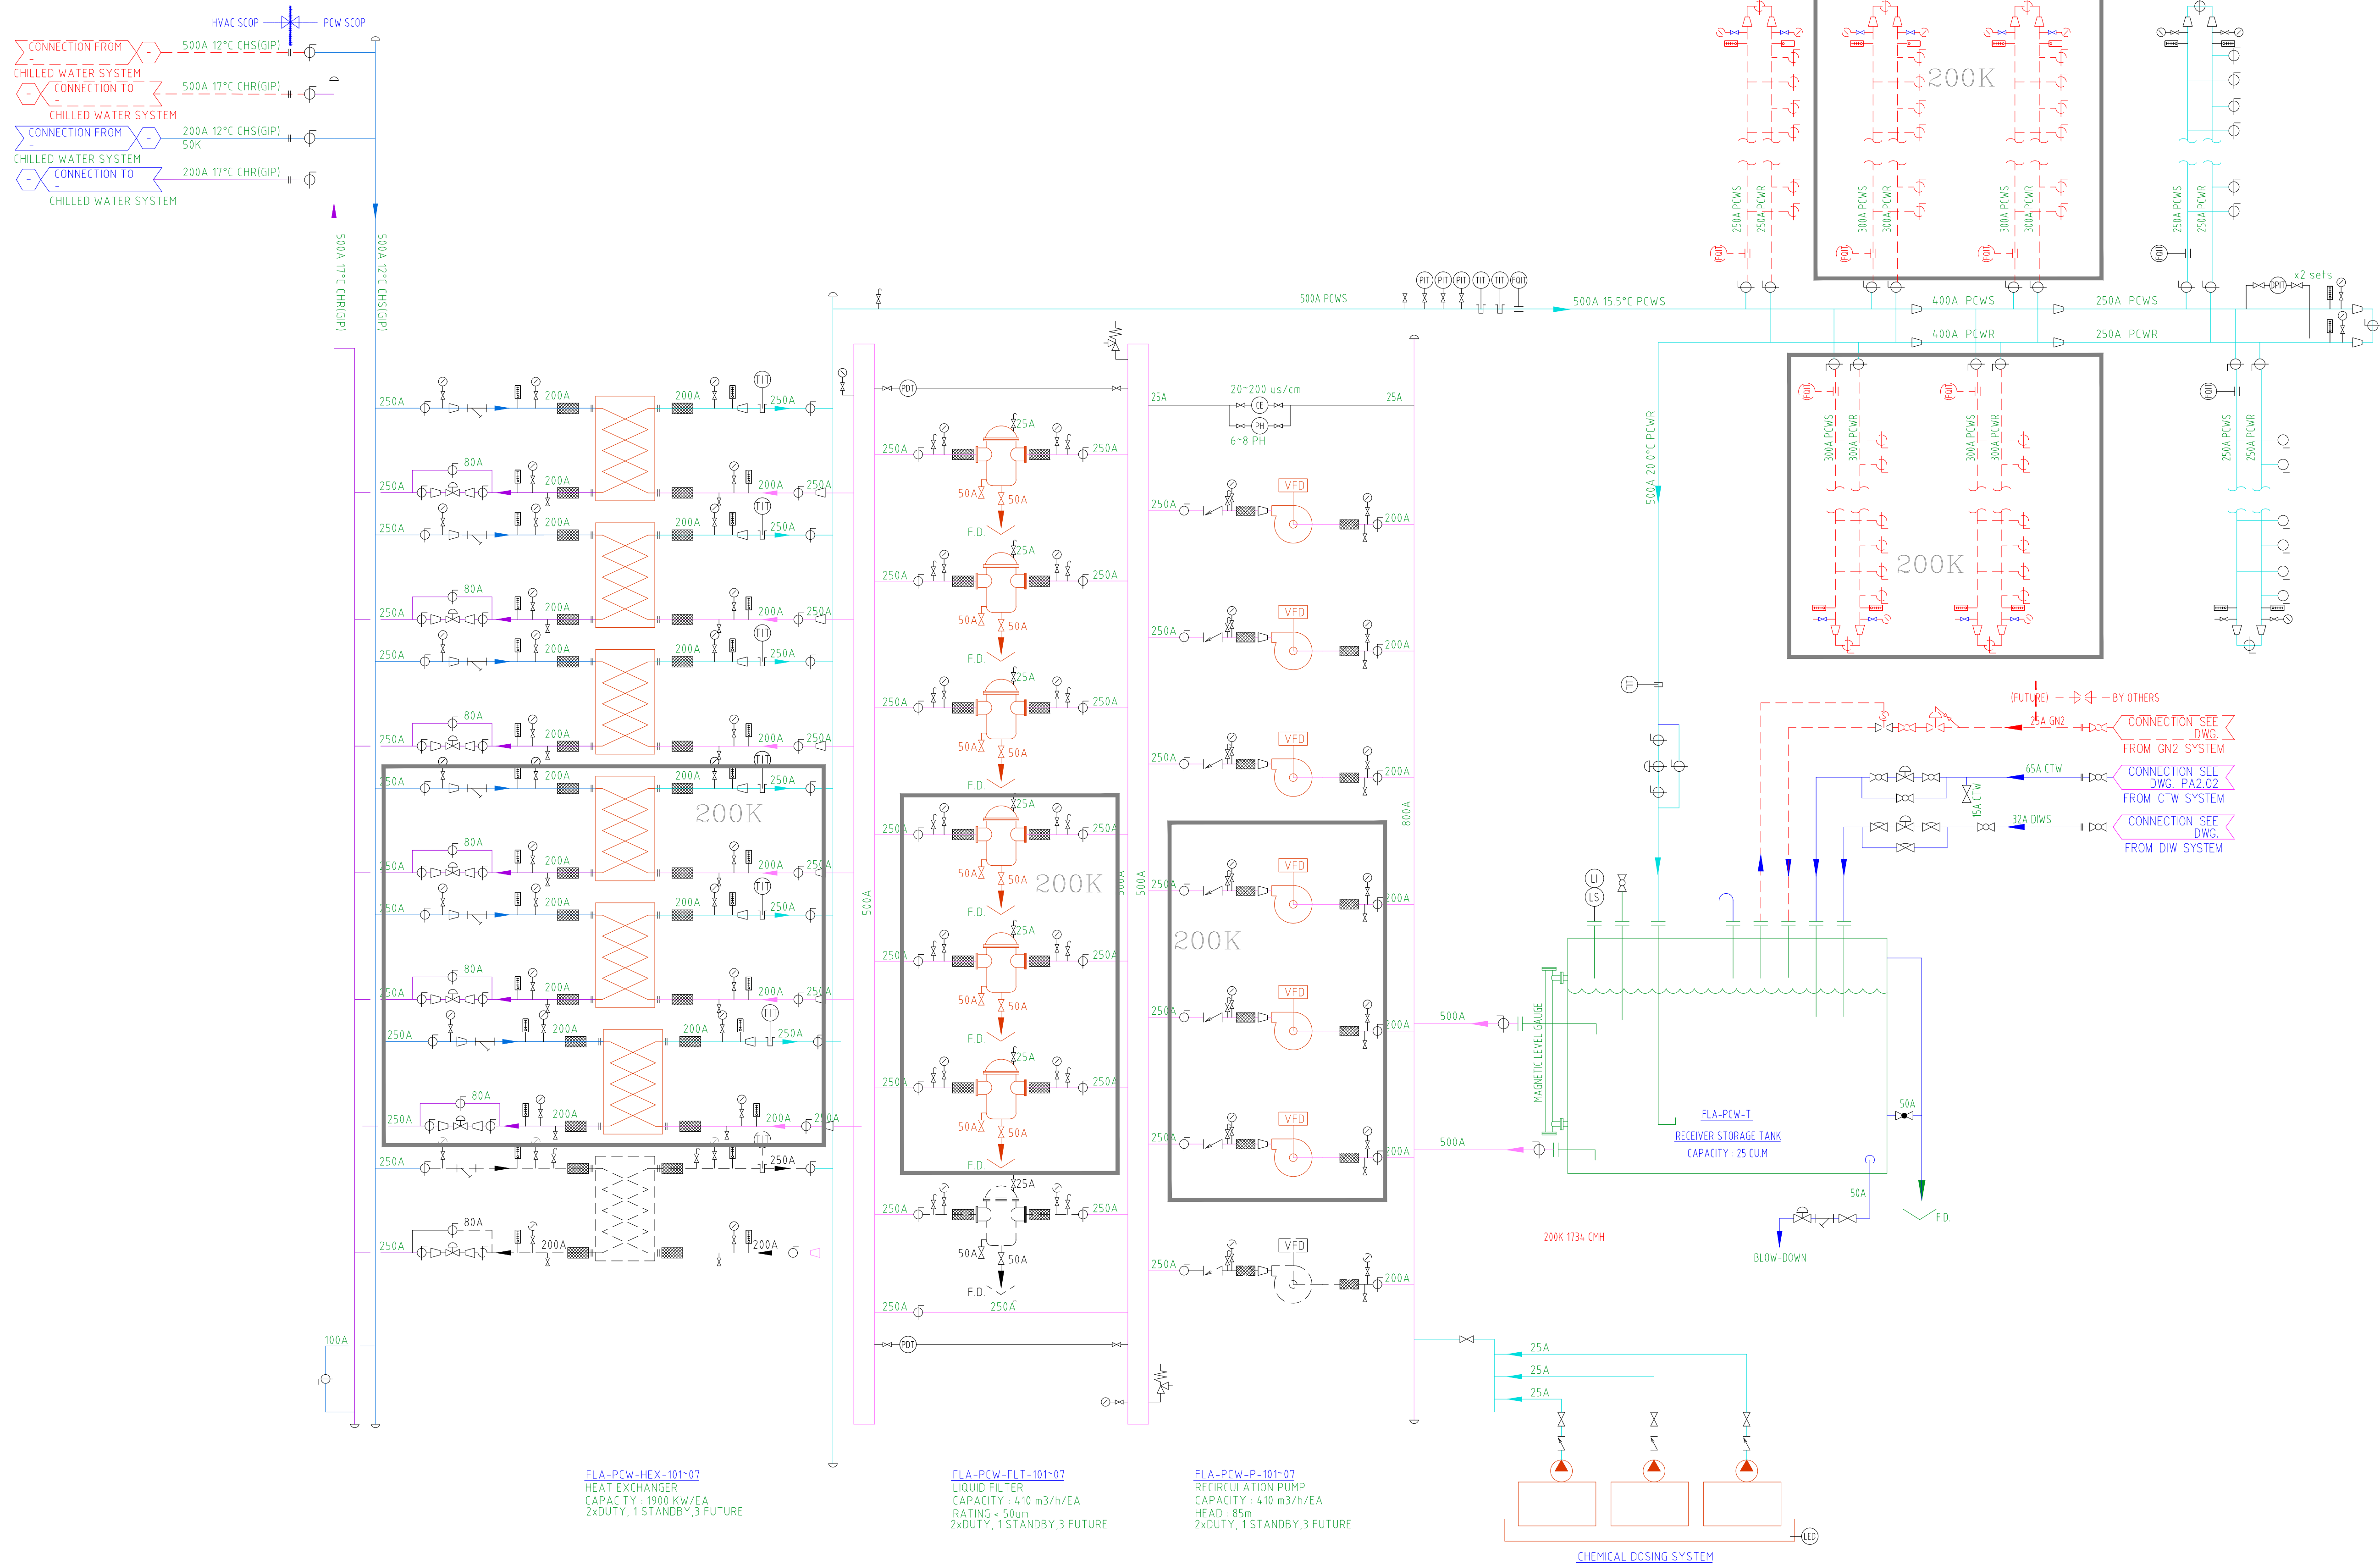

OWNER / DEVELOPER

micron.

ARCHITECTURAL CONSULTANT

JJP ARCHITECTS & PLANNERS 潘冀聯合建築師

CIVIL & STRUCTURAL CONSULTANT

TEAM 群策工程股份有限公司

MECHANICAL & ELECTRICAL CONSULTANT & CONTRACTOR

uis 漢唐集成股份有限公司

SUB-CONTRACTOR

PROJECT ADDRESS

KEY PLAN

PROJECT TITLE			
Micron Falcon A Project (200K)			
PROJECT PHASE			
Concept Design			
DRAWING TITLE			
SYSTEM DIAGRAM - PCW SYSTEM			
-			
-			
DESIGNED: CHEN	DRAWN: CHEN	CHECKED: C.S.HU	
DATE: 2024/11/20	JOB NO.:	SCALE: N.T.S	
DRAWING NO.	DE_F1_ALL_B0001_D_WPCW_6001-00		REV
			0
	SHEET:	SIZE A1	