


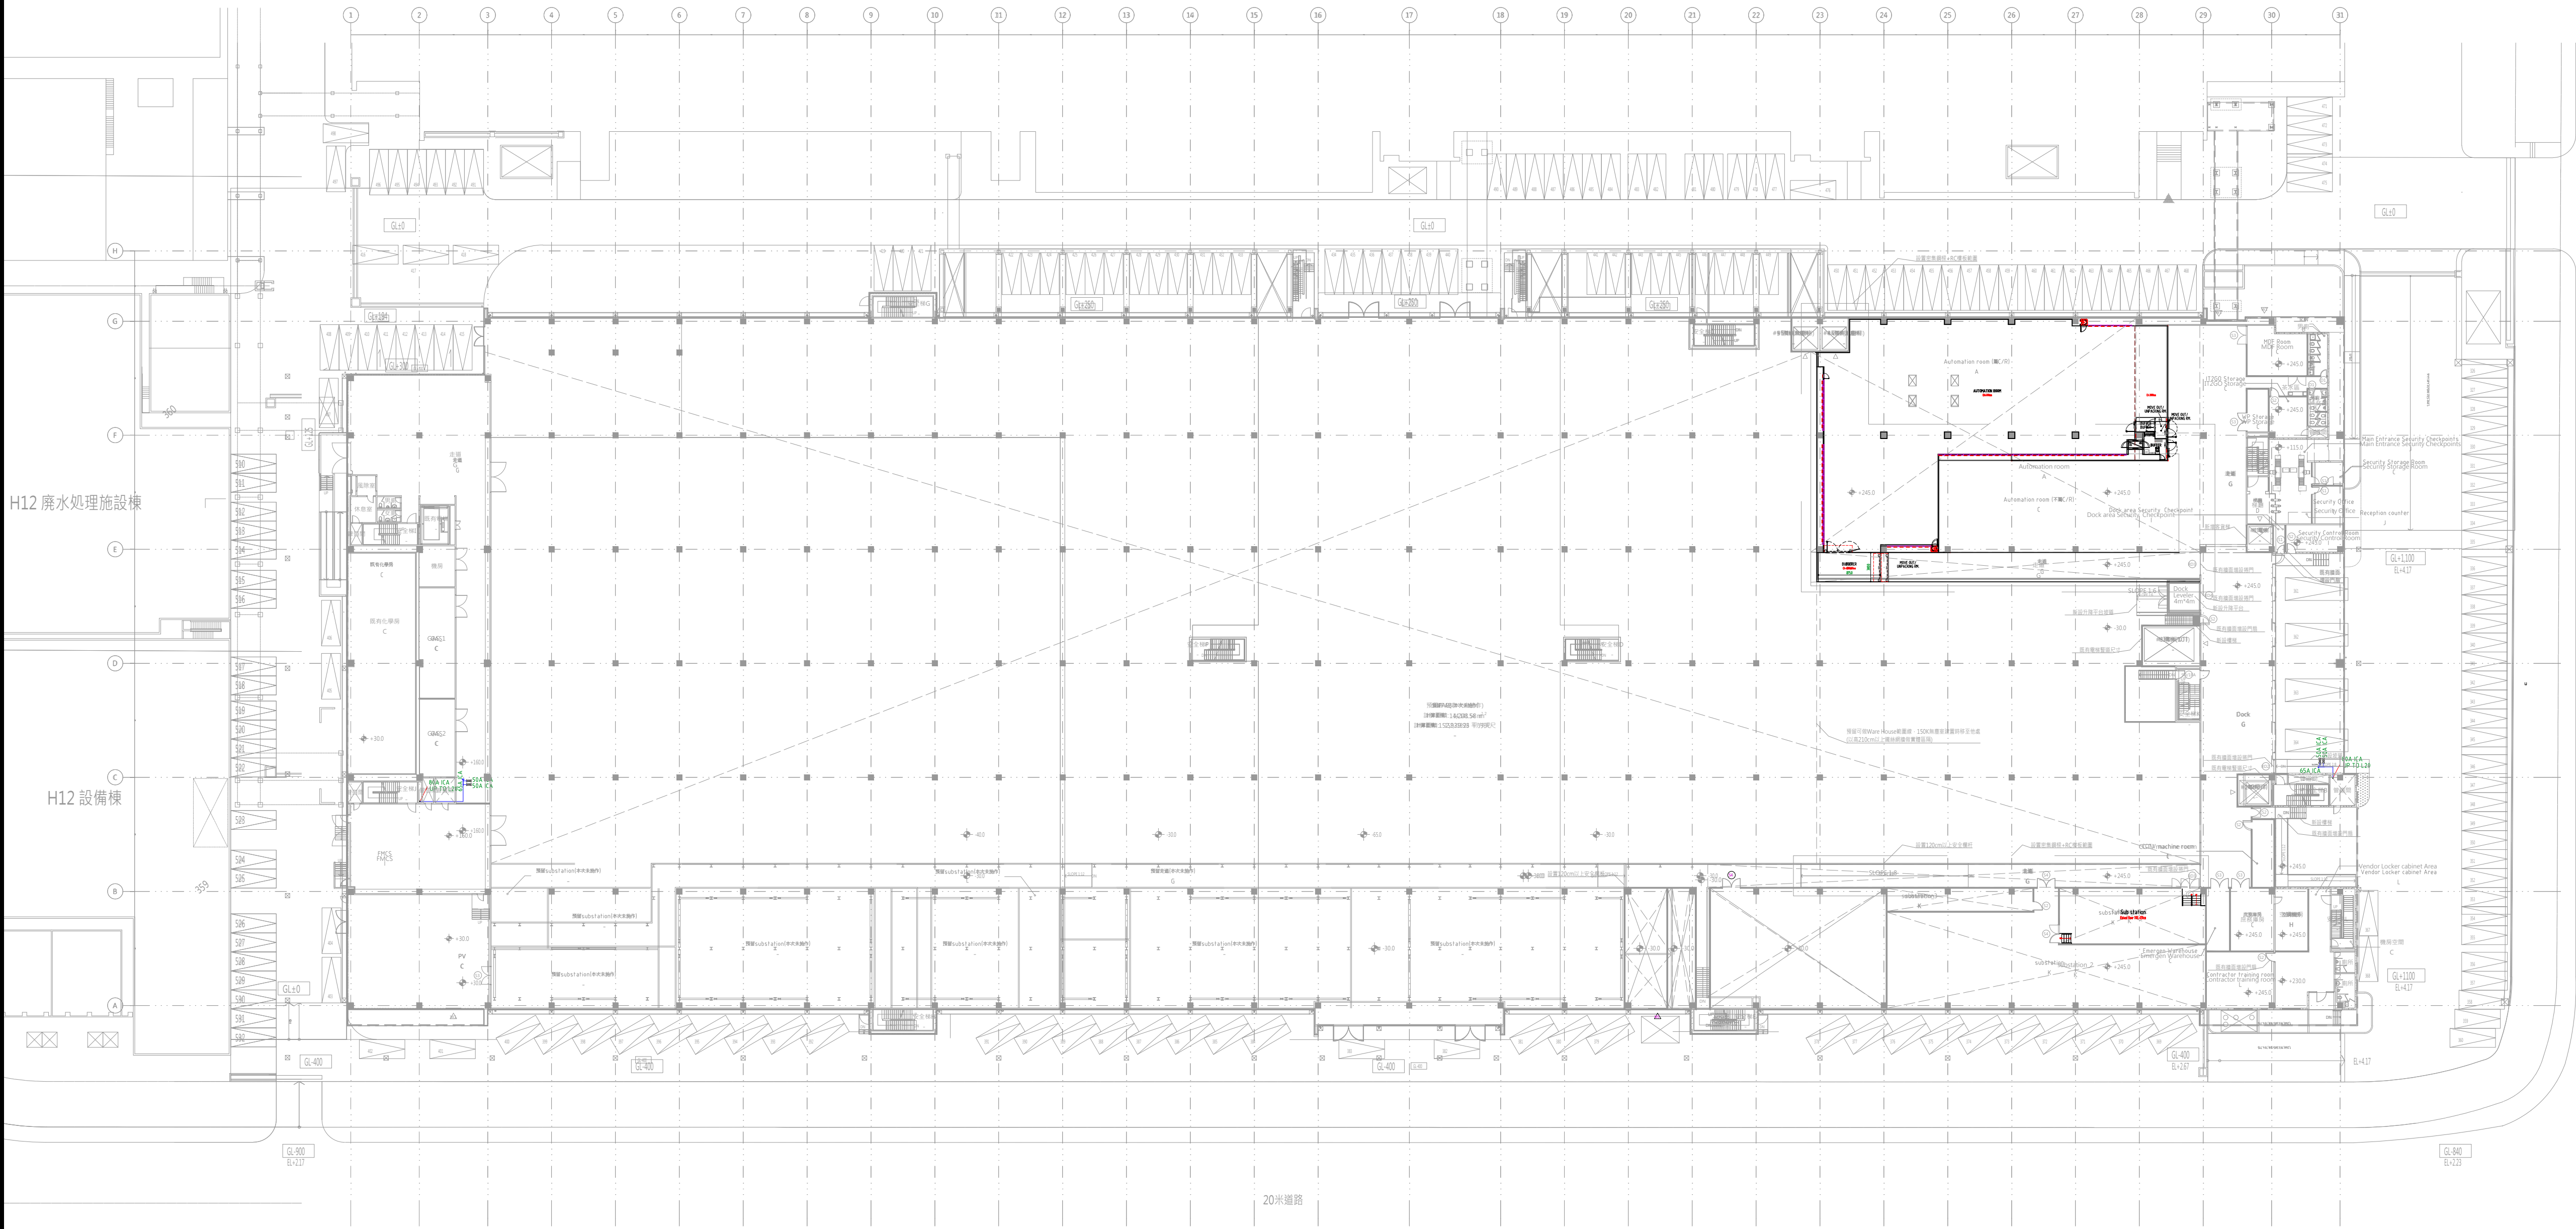

OWNER / DEVELOPER

micron

ARCHITECTURAL CONSULTANT

JJP ARCHITECTS & PLANNERS 潘冀聯合建築師

CIVIL & STRUCTURAL CONSULTANT


TEAM 群策工程股份有限公司

MECHANICAL & ELECTRICAL CONSULTANT & CONTRACTOR

uis 漢唐集成股份有限公司

SUB-CONTRACTOR

PROJECT ADDRESS

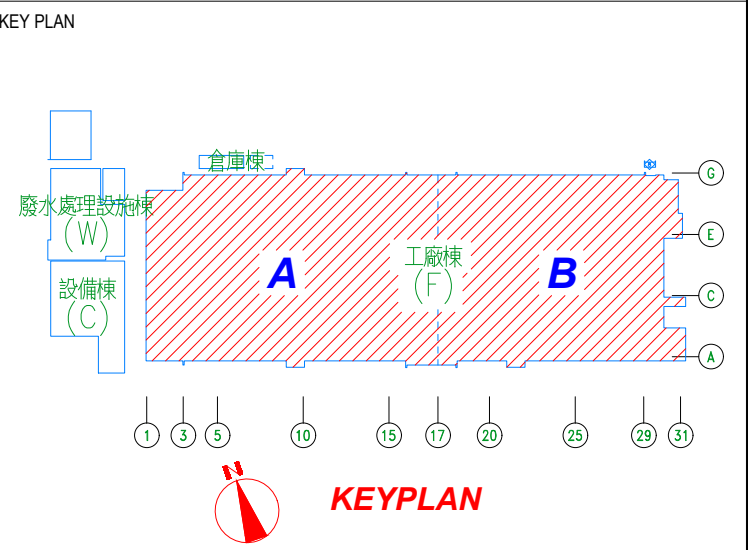

REV	DATE	DESCRIPTION	ISSUED BY
A	2025/01/02	REVIEW Drawing	

PROJECT TITLE

Micron Falcon A Project (200K)

PROJECT PHASE

Concept Design

DRAWING TITLE

**FLOOR PLAN -
ICA SYSTEM
FAB A LEVEL 10
(OVERALL)**

DESIGNED : DATE : DRAWING NO.	DESIGNED 2024/11/20 DE_F1_FAB_B0001_D_AICA_2L10-00	DRAWN : JOB NO.:	RACHEL	CHECKED : SCALE : SHEET:	C.S.HU 1:500 SIZE A1
-------------------------------------	--	---------------------	--------	--------------------------------	-------------------------------