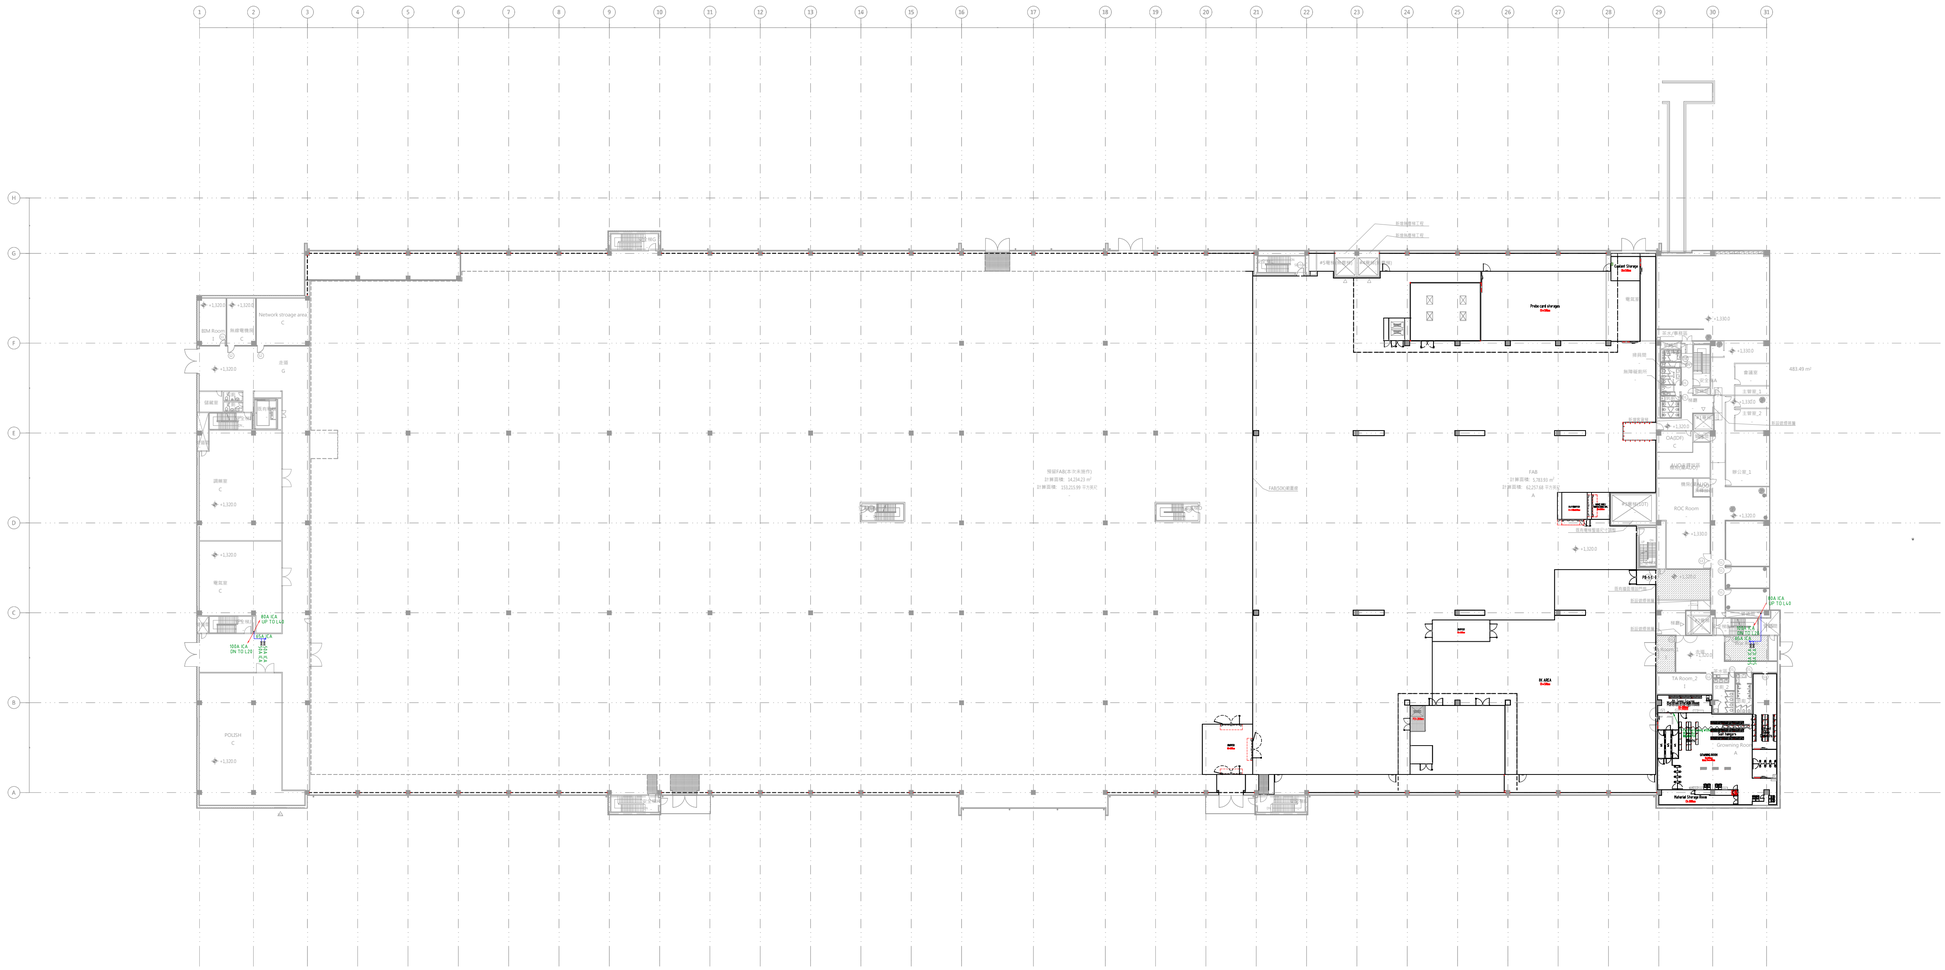


OWNER / DEVELOPER

micron

ARCHITECTURAL CONSULTANT

JJP ARCHITECTS & PLANNERS 潘冀聯合建築師

CIVIL & STRUCTURAL CONSULTANT

TEAM 群策工程股份有限公司

MECHANICAL & ELECTRICAL CONSULTANT & CONTRACTOR

UIS United Integrated Services 漢唐集成股份有限公司

SUB-CONTRACTOR

PROJECT ADDRESS

KEY PLAN




| REV | DATE | DESCRIPTION | ISSUED BY |
|---|---|---|---|
| A | 2025/01/02 | REVIEW Drawing | |

Revisions

PROJECT TITLE

Micron Falcon A Project (200K)

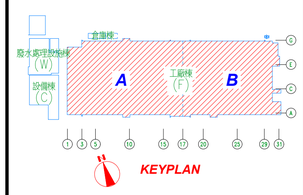PROJECT PHASE

Concept Design

DRAWING TITLE

FLOOR PLAN -
ICA SYSTEM
FAB A LEVEL 30
(OVERALL)

| | | | |
|---|---|---|---|
| DESIGNED : DESIGNED | DRAWN : RACHEL | CHECKED : C.S.HU | |
| DATE : 2024/11/20 | JOB NO. : | SCALE : 1:500 | |
| DRAWING NO. DE_F1_FAB_B0001_D_AICA_2L30-00 | | | REV 0 |
| | | SHEET: | SIZE A1 |