
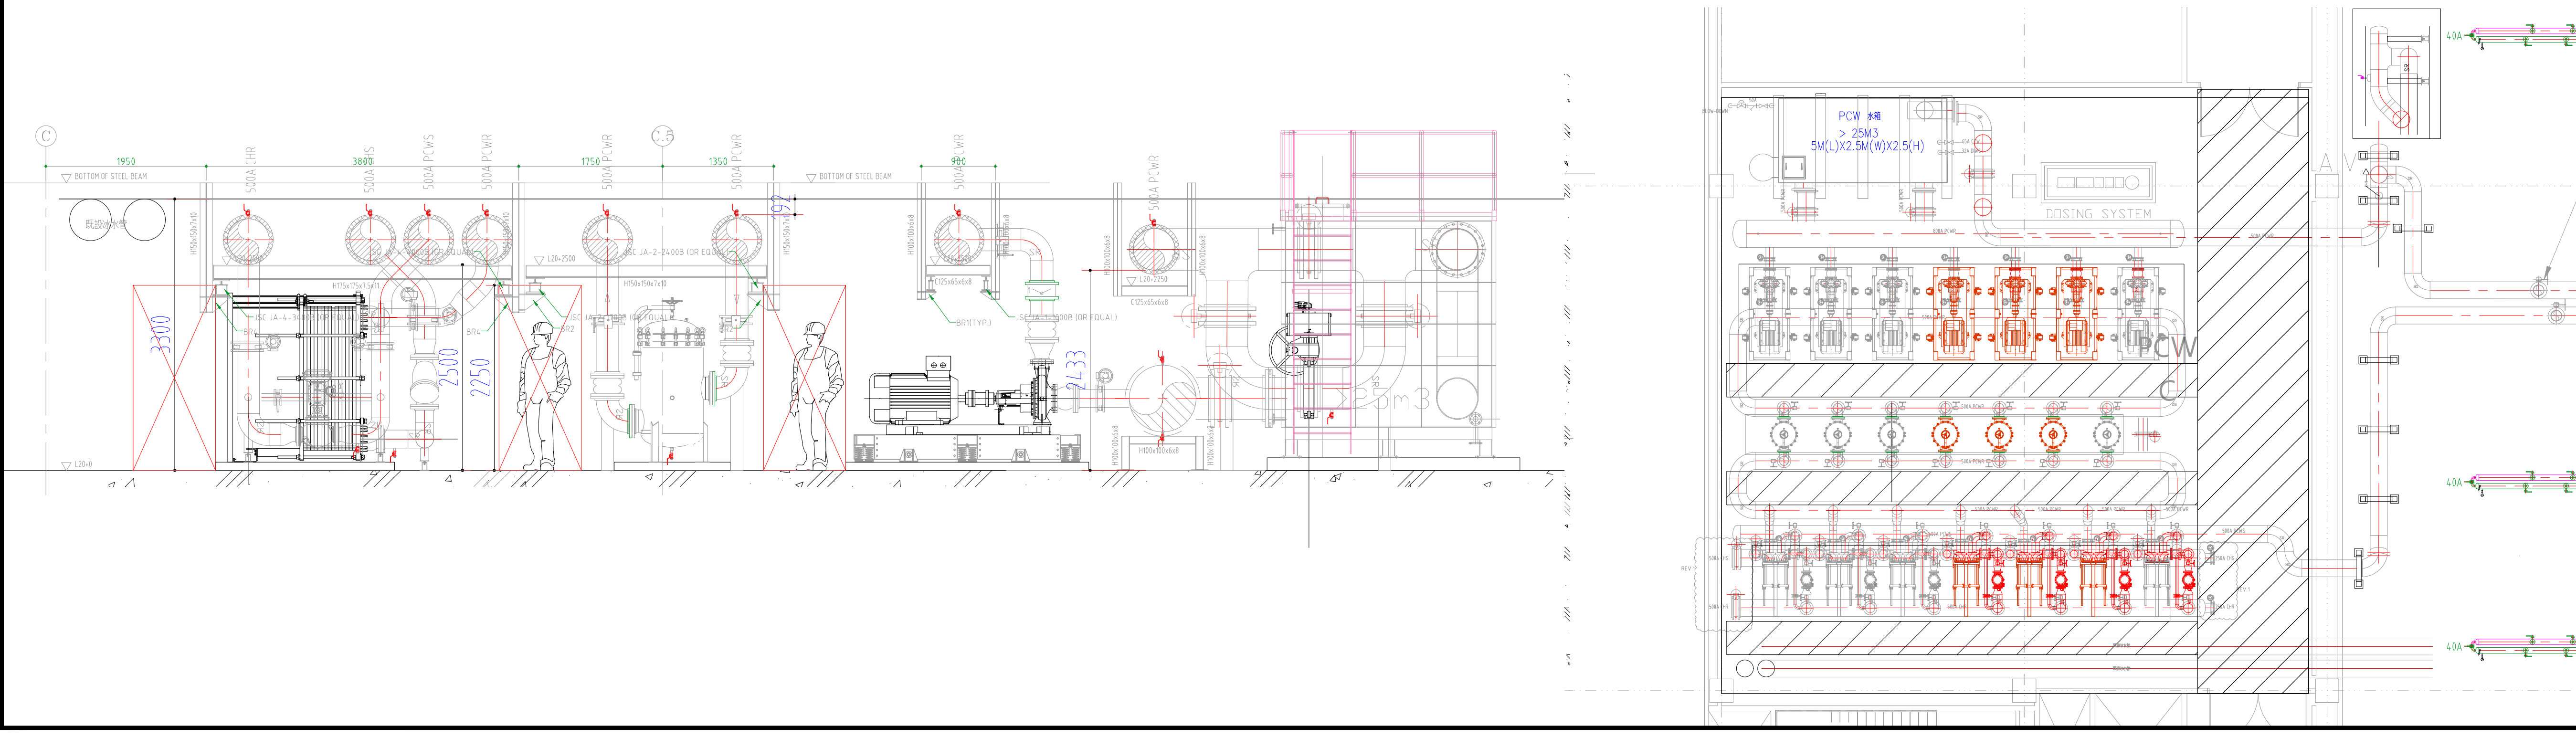


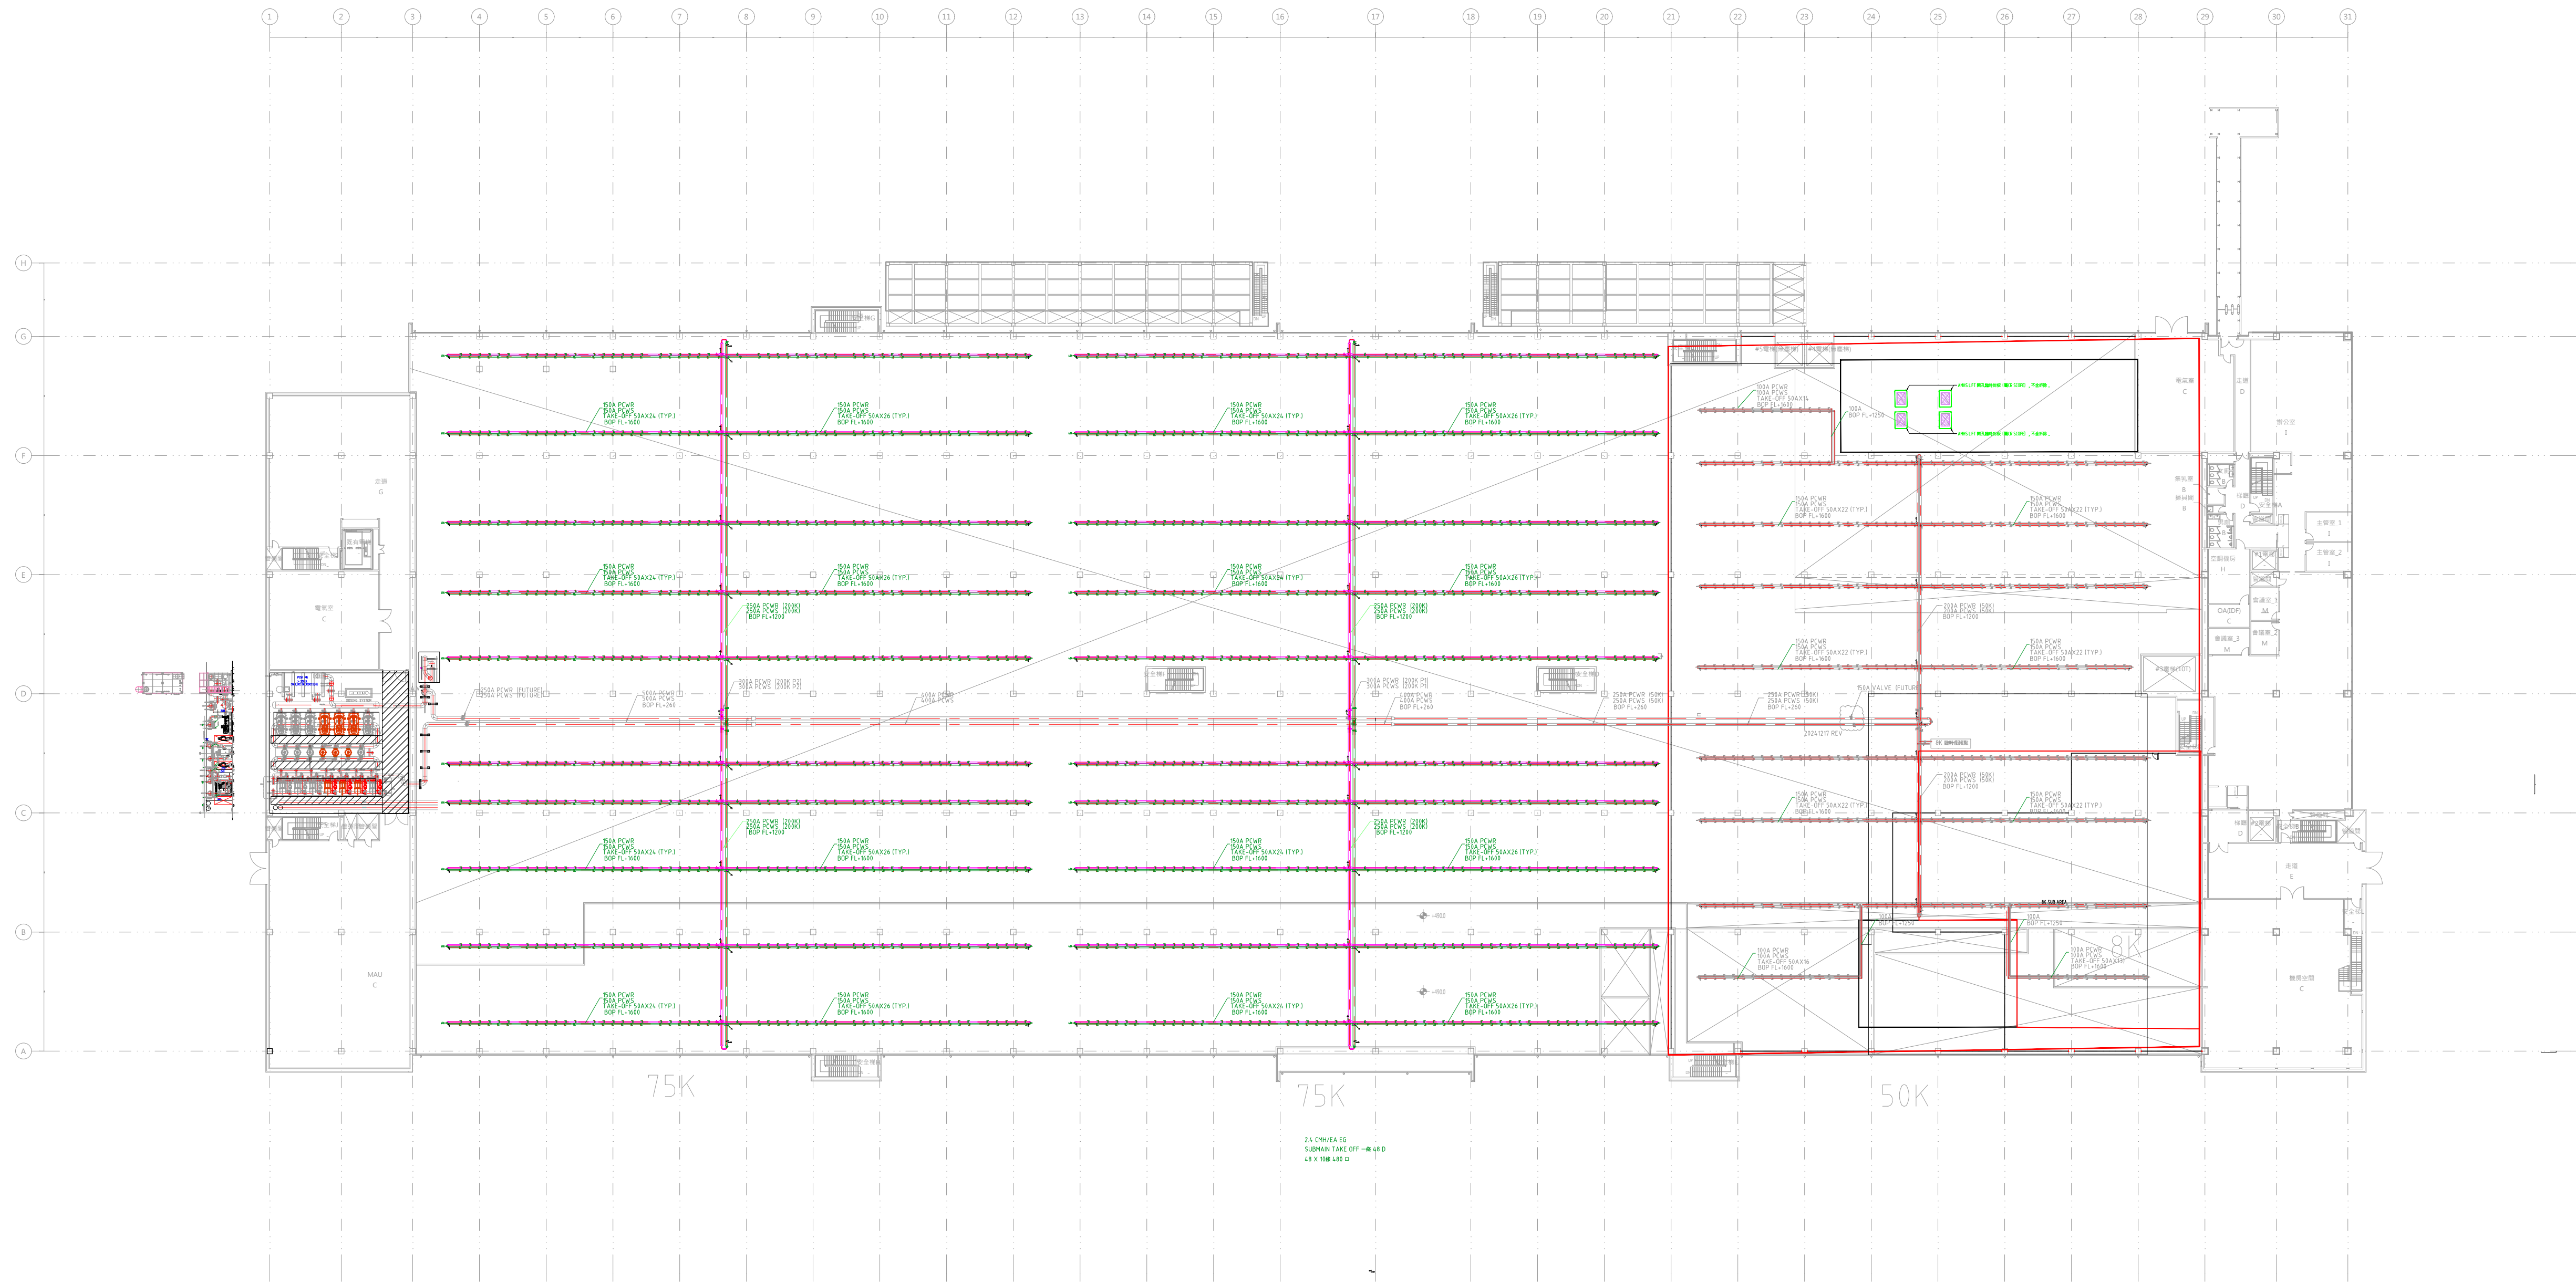

OWNER / DEVELOPER

micron

ARCHITECTURAL CONSULTANT

JJP ARCHITECTS & PLANNERS

潘冀聯合建築師

CIVIL & STRUCTURAL CONSULTANT

TEAM

群策工程股份有限公司

MECHANICAL & ELECTRICAL CONSULTANT & CONTRACTOR

uis 漢唐集成股份有限公司

SUB-CONTRACTOR

PROJECT ADDRESS

KEY PLAN

REV	DATE	DESCRIPTION	ISSUED BY
A	2025/01/02	REVIEW Drawing	

PROJECT TITLE

Micron Falcon A Project (200K)

PROJECT PHASE

Concept Design

DRAWING TITLE

FLOOR PLAN -
PCW SYSTEM
FAB A LEVEL 20
(OVERALL)

DESIGNED : DESIGNED

DATE : 2024/11/20

DRAWN : RACHEL

JOB NO. :

CHECKED : C.S.HU

SCALE : 1:--

DRAWING NO.

DE_F1_FAB_B0001_D_WPCW_2L20-00

REV

0

SHEET:

SIZE

A1