CONFIDENTIALITY NOTICE: THE CONTENT OF THIS DOCUMENT IS SENSITIVE INFORMATION MADE AND OWNED BY MICRON CORPORATION AND IS PROTECTED BY COPYRIGHT LAWS AND RELEVANT LAWS/REGULATIONS. ONLY EMPLOYEES OF MICRON ARE ALLOWED TO ACCESS AND USE THIS SENSITIVE INFORMATION WITHIN THE WORK SCOPE UNDER THEIR SPECIFIC AND RESPECTIVE DUTIES AND OBLIGATIONS REQUIRED BY AGREEMENT WHICH IS NOT ALLOWED TO COPY, REPRODUCE, DISTRIBUTE PUBLICLY OR DISCLOSE IN WHOLE OR IN PART TO ANY OTHER PARTY WITHOUT CTCI'S PRIOR AND WRITTEN CONSENT.

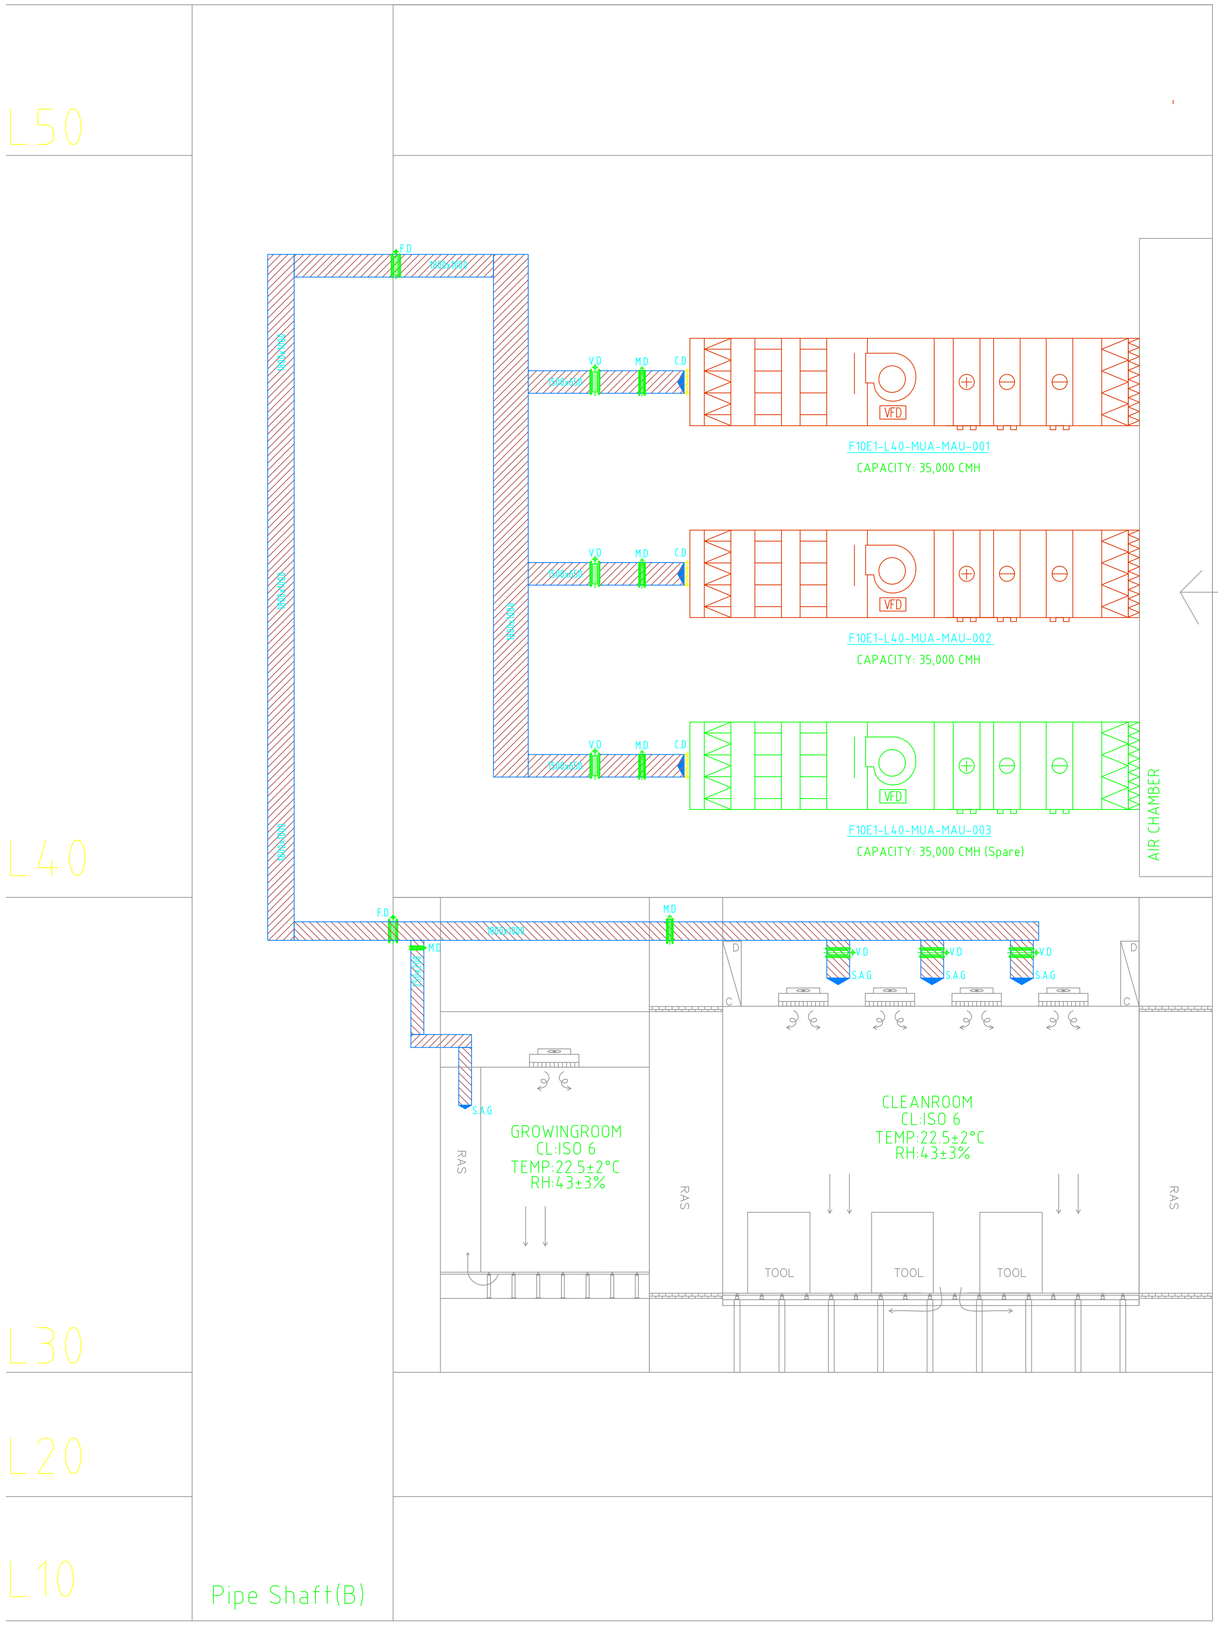

OWNER / DEVELOPER

micron

ARCHITECTURAL CONSULTANT

CIVIL & STRUCTURAL CONSULTANT

MECHANICAL & ELECTRICAL CONSULTANT

DESIGN MANAGER

CTCI Singapore Pte. Ltd.

PROJECT ADDRESS

North Coast Drive, Singapore

KEY PLAN

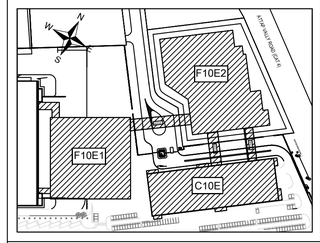

Secret
R3
Level

SHEET PURPOSE

REV.	DATE	DESCRIPTION	ISSUED BY

Revisions

PROJECT TITLE

Project FAB 10 Expansion Phase 2 A&E Services

PROJECT PHASE

A&E

DRAWING TITLE

Flow Diagram_
MAU DUCT SYSTEM F10E1

DESIGNED : 設計者		DRAWN : 作者		CHECKED : 審圖員	
DATE : 02/12/26		JOB NO. :		SCALE :	
Micron DRAWING NO.	F01-F10E-PFD-F10E1-00-K-102				REV 0A
CTCI DRAWING NO.					
Reference Model					
CTCI			SHEET: 1 OF 1		SIZE A1