

CONFIDENTIALITY NOTICE: THE CONTENT OF THIS DOCUMENT IS SENSITIVE INFORMATION MADE AND OWNED BY MICRON CORPORATION AND IS PROTECTED BY COPYRIGHT LAWS AND RELEVANT LAWS/REGULATIONS. ONLY EMPLOYEES OF MICRON ARE ALLOWED TO ACCESS AND USE THIS SENSITIVE INFORMATION WITHIN THE WORK SCOPE UNDER THEIR SPECIFIC AND RESPECTIVE DUTIES AND OBLIGATIONS REQUIRED BY AGREEMENT WHICH ISN'T ALLOWED TO COPY, REPRODUCE, DISTRIBUTE PUBLICLY OR DISCLOSE IN WHOLE OR IN PART TO ANY OTHER PARTY WITHOUT CTCI'S PRIOR AND WRITTEN CONSENT.

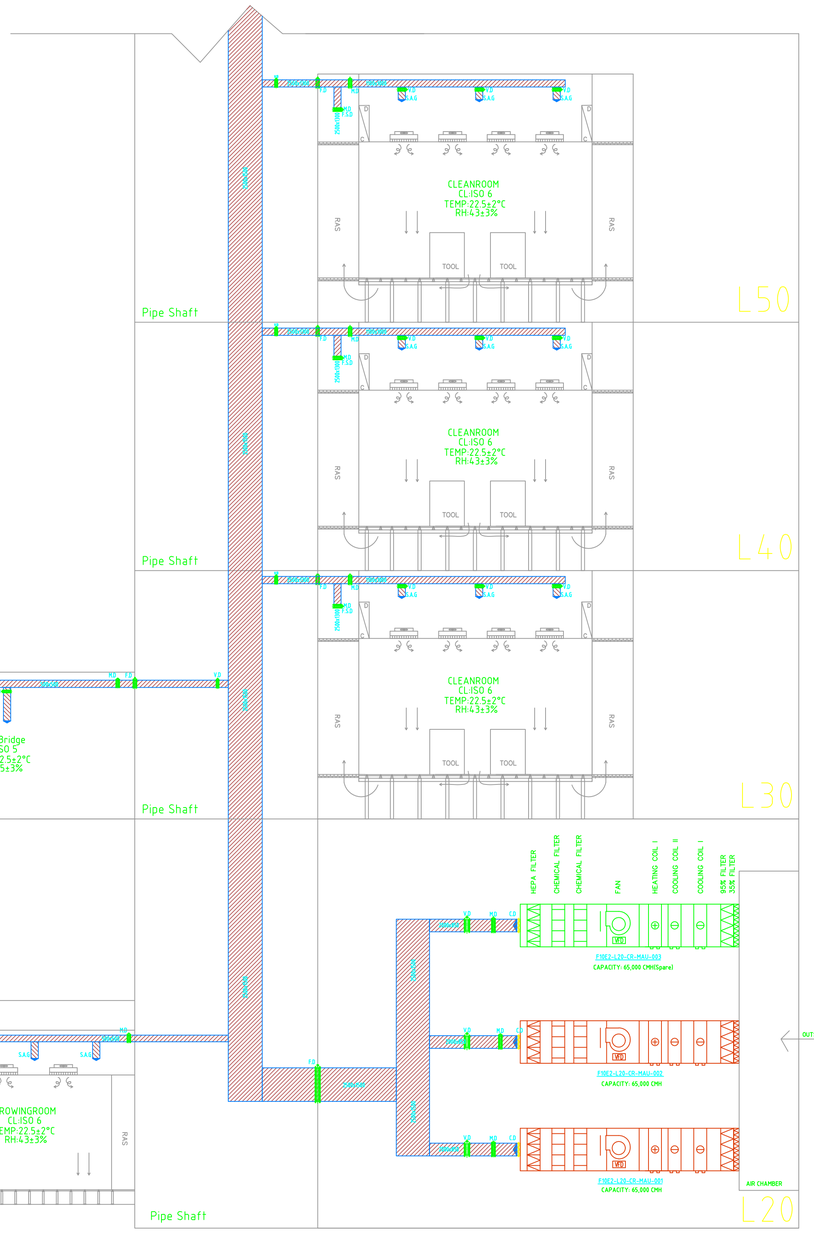

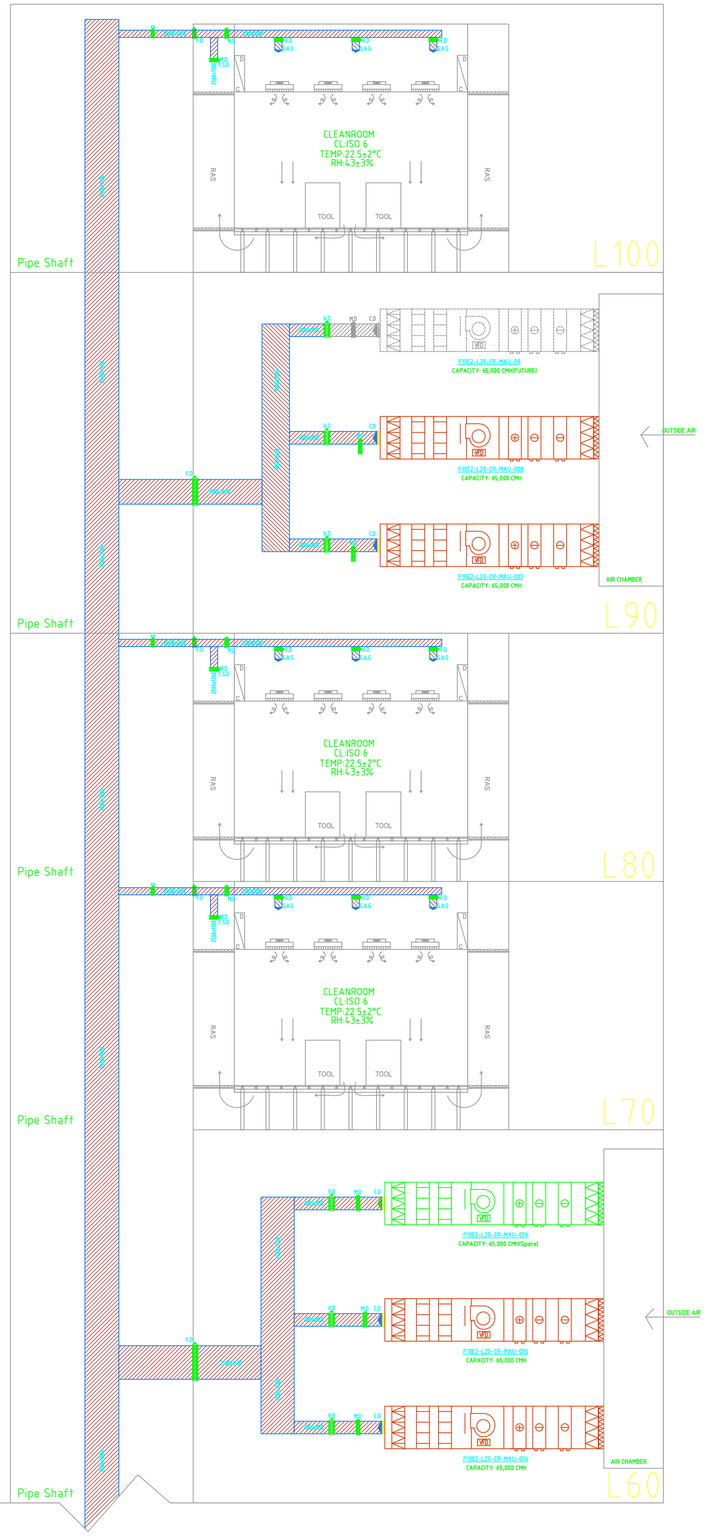

OWNER / DEVELOPER

micron™

ARCHITECTURAL CONSULTANT

CIVIL & STRUCTURAL CONSULTANT

MECHANICAL & ELECTRICAL CONSULTANT


DESIGN MANAGER

CTCI Singapore Pte. Ltd.

PROJECT ADDRESS

North Coast Drive, Singapore

KEY PLAN

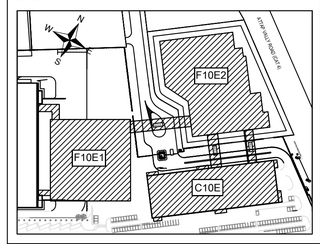

Secret
R3
Level

FOR REVIEW

REV	DATE	DESCRIPTION	ISSUED BY

Revisions

PROJECT TITLE

Micron F10E Probe Project

PROJECT PHASE

A&E

DRAWING TITLE

Flow Diagram_
MAU DUCT SYSTEM F10E2

DESIGNED :	設計者	DRAWN :	作者	CHECKED :	審圖員
DATE :	02/12/26	JOB NO. :		SCALE :	

Micron DRAWING NO.	F10-F10E-PFD-F10E2-00-K-102	REV
CTCI DRAWING NO.		0A
Reference Model		

CTCI	SHEET: 1 OF 1	SIZE A1	