


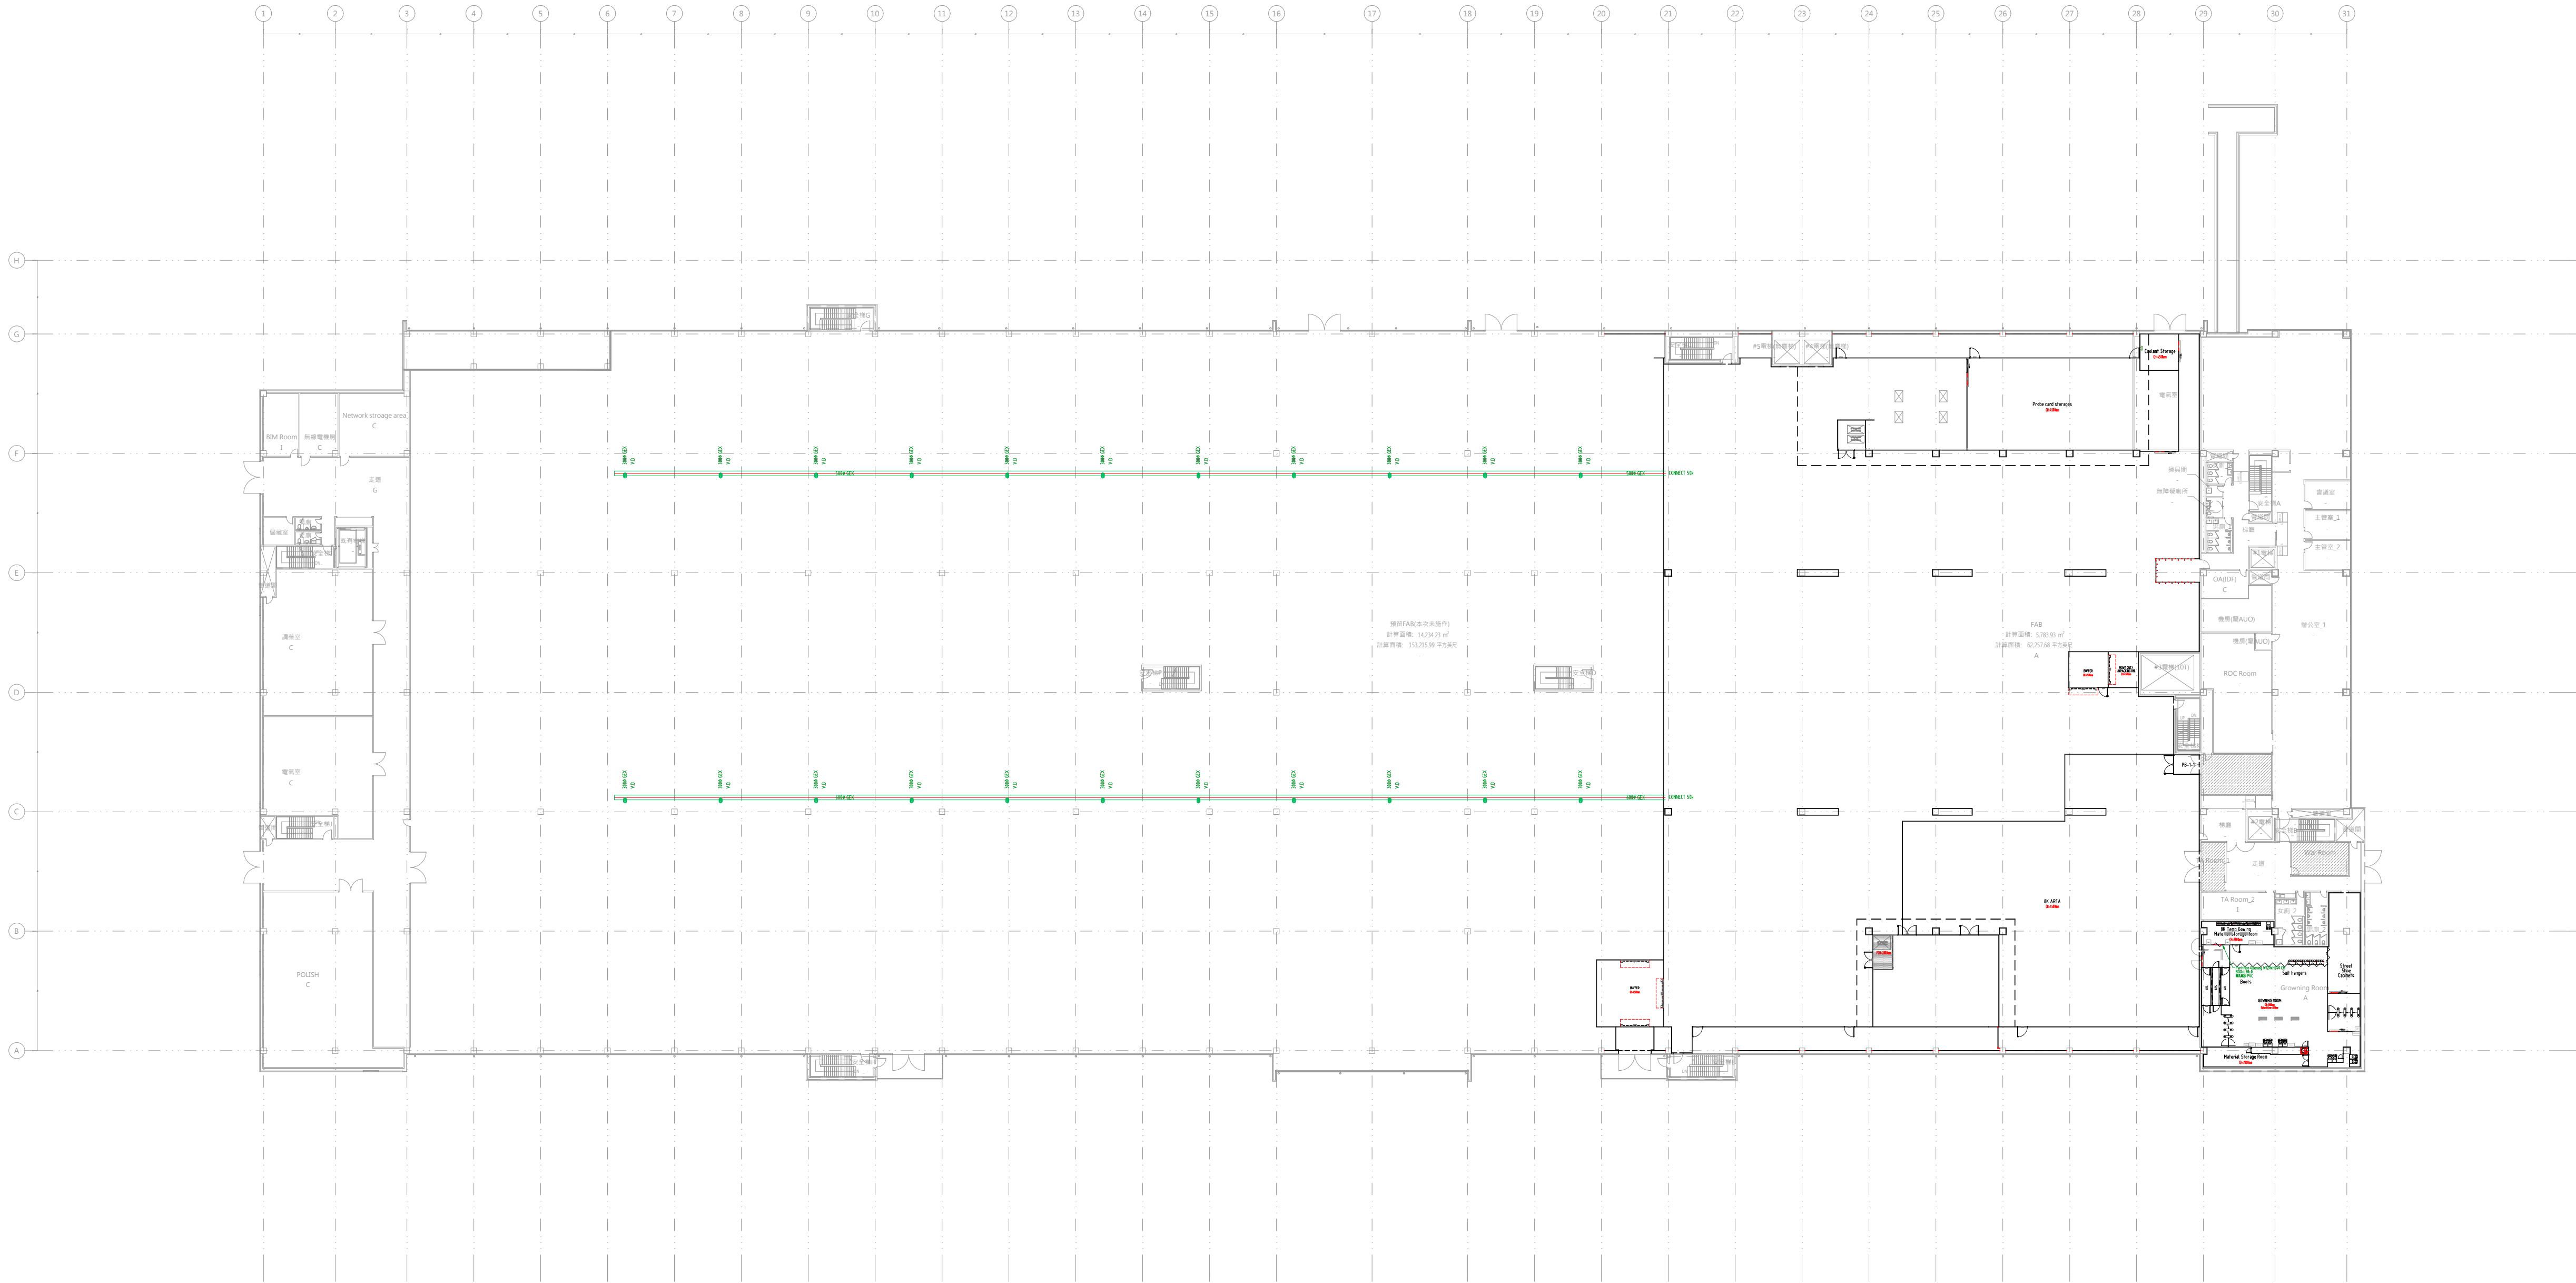

OWNER / DEVELOPER

micron

ARCHITECTURAL CONSULTANT

JJP ARCHITECTS & PLANNERS

潘冀聯合建築師

CIVIL & STRUCTURAL CONSULTANT

TEAM

群策工程股份有限公司

MECHANICAL & ELECTRICAL CONSULTANT & CONTRACTOR

uis 漢唐集成股份有限公司

SUB-CONTRACTOR

PROJECT ADDRESS

KEY PLAN

儲水及淨水設備 (W)

設備樁 (C)

工廠樁 (F)

倉庫樁

A

B

1

3

5

7

9

11

13

15

17

19

21

23

25

27

29

31

KEYPLAN

1	2025/01/09	REVIEW Drawing	
0	2024/11/20	REVIEW Drawing	
REV	DATE	DESCRIPTION	ISSUED BY
		Revisions	

PROJECT TITLE

Micron Falcon A Project

PROJECT PHASE

Construction

DRAWING TITLE

FLOOR PLAN -
GEX SYSTEM
FAB A LEVEL 30
(OVERALL)

DESIGNED: ELLIS	DRAWN: ELLIS	CHECKED: C.S.HU
DATE: 2025/01/09	JOB NO.:	SCALE: 1:500
DRAWING NO.	REV	
DE_F1_FAB_B001_D_EGEX_2L30-00	1	
	SHEET:	SIZE A1