


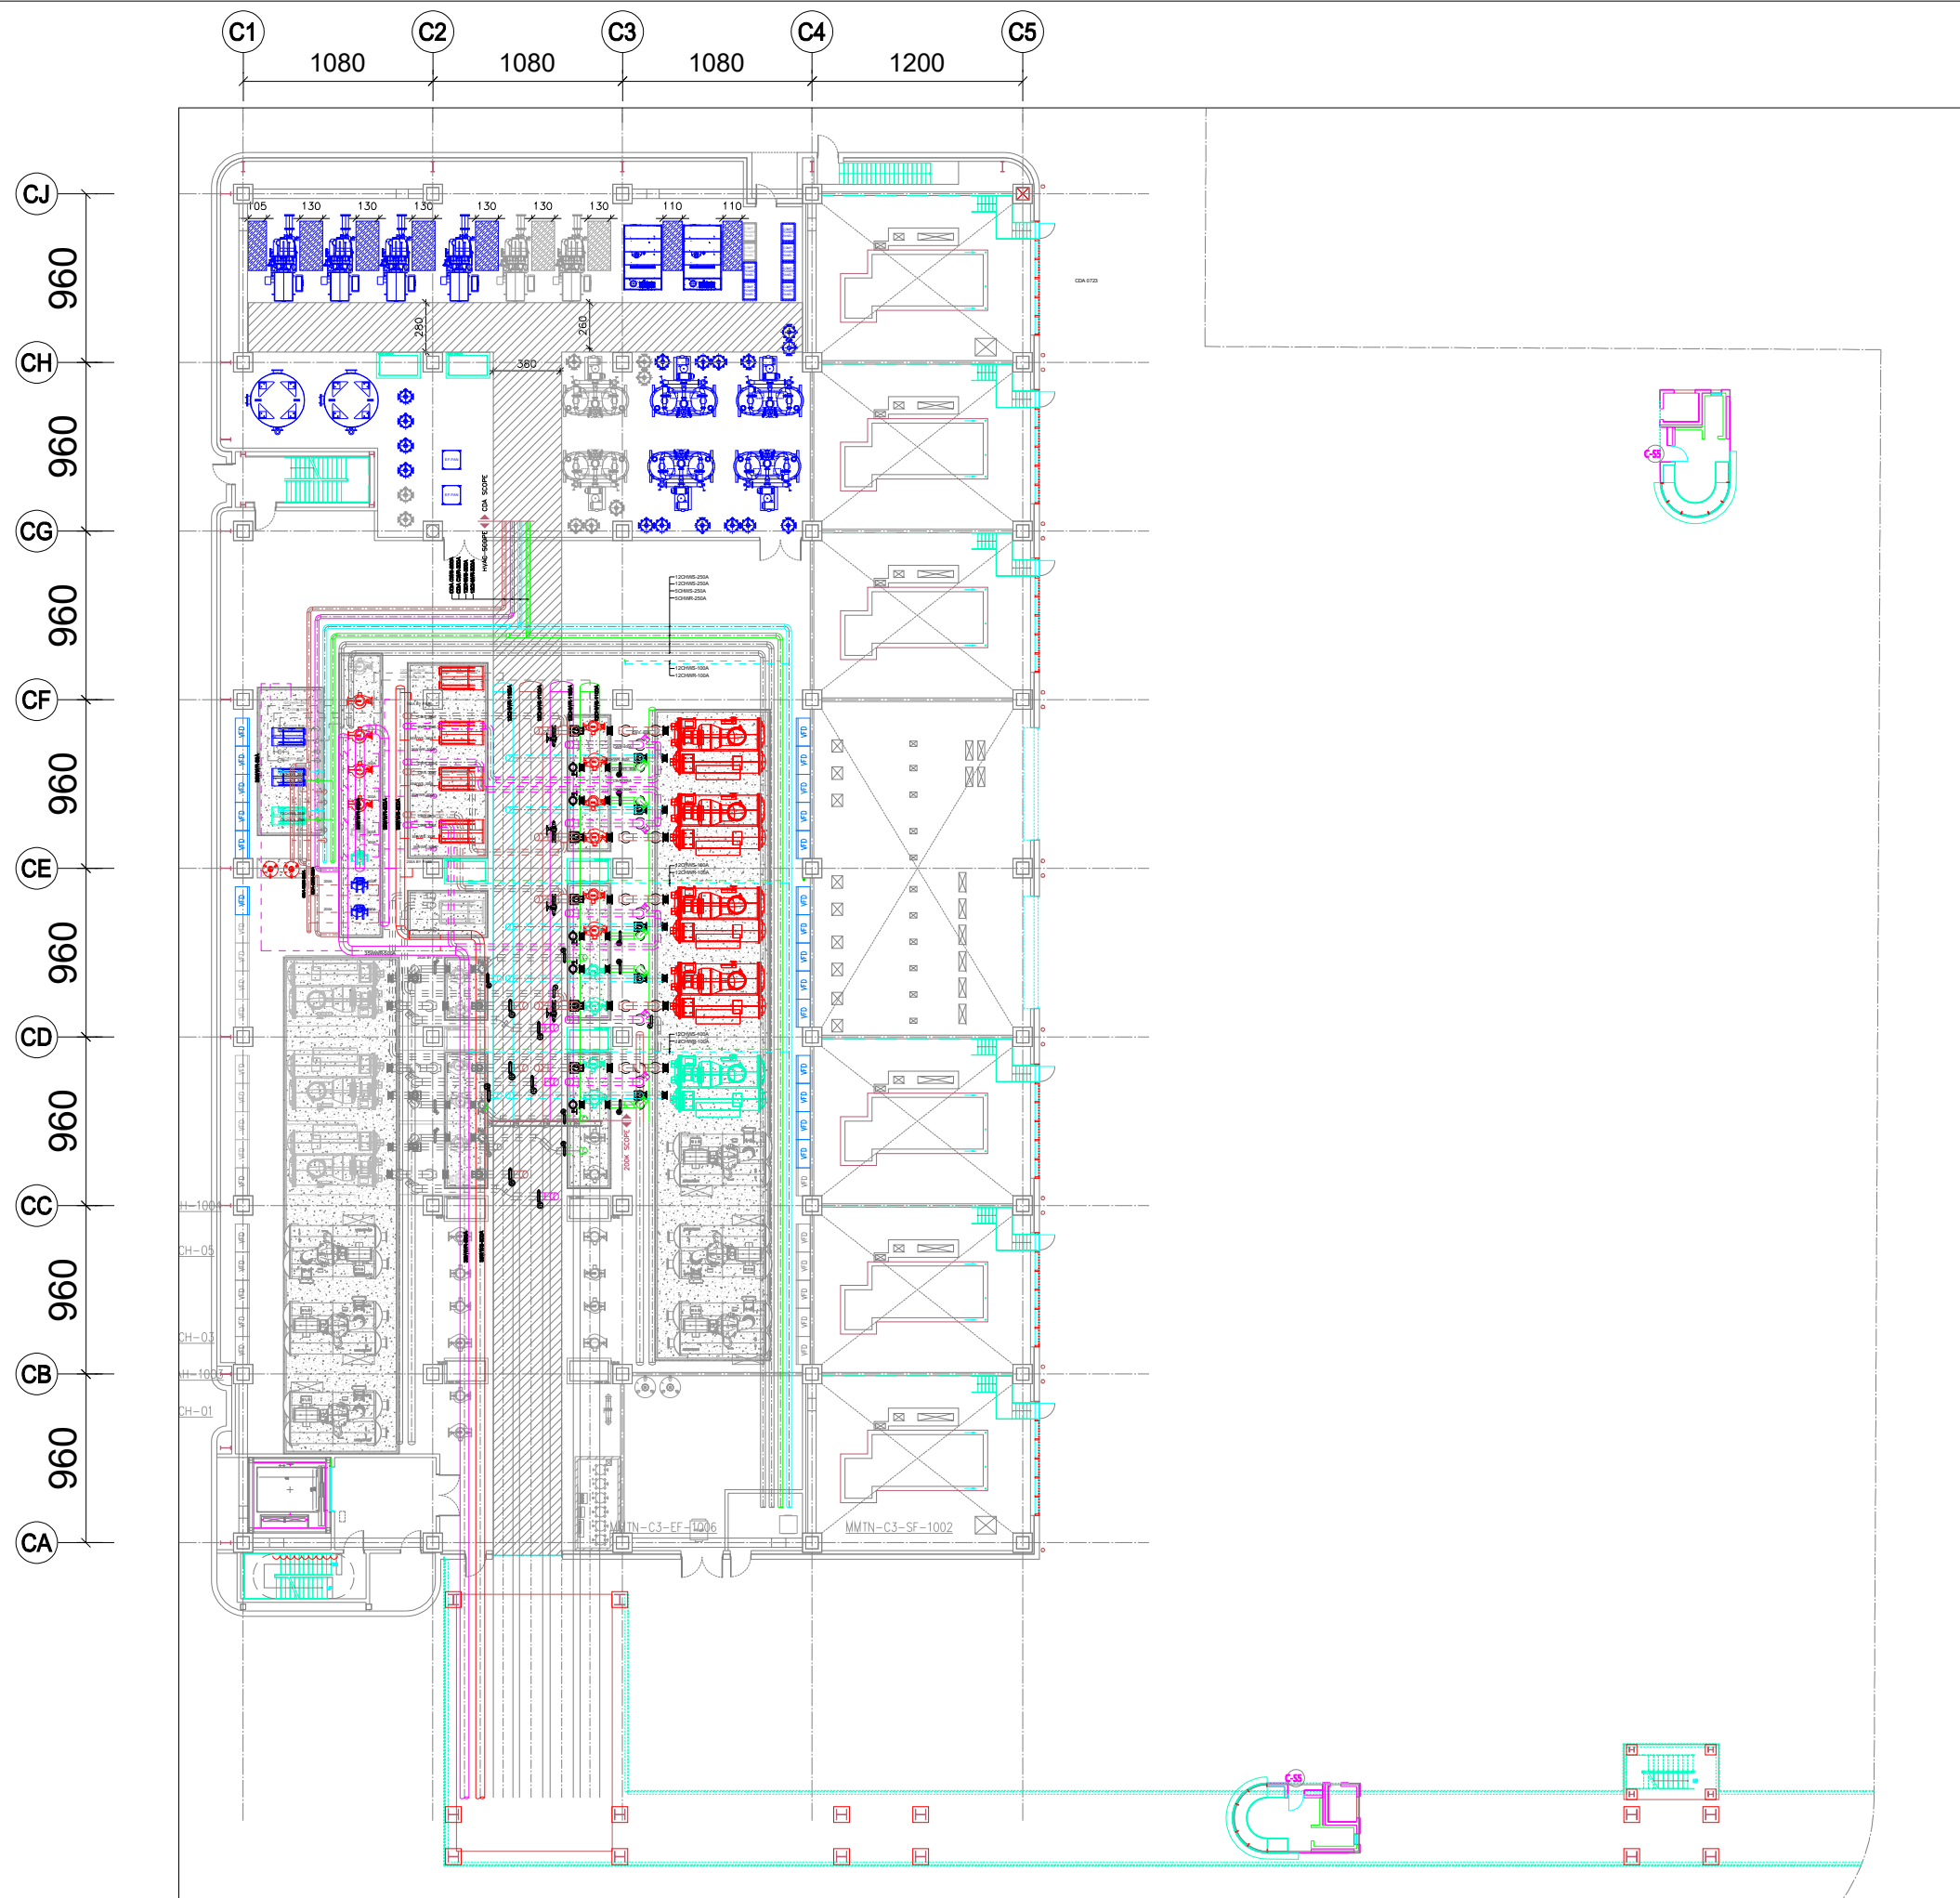

OWNER / DEVELOPER

micron

ARCHITECTURAL CONSULTANT

QUO 陳昆豐建築師事務所

CIVIL & STRUCTURAL CONSULTANT

禾森 禾森工程顧問有限公司

MECHANICAL & ELECTRICAL CONSULTANT & CONTRACTOR

 洋基工程股份有限公司
YANKEY Engineering Co., Ltd

SUB-CONTRACTOR

PROJECT ADDRESS:

KEY PLAN

[illegible]

PROJECT TITLE

PROJECT TITLE
美光台南廠188K增建工程

PROJECT PHASE

Concept Design

DRAFTING TITLE

DE MMTN C3 B002 M CHWT 2L10

CUB 3 L10 空調(中溫冰水)設備管路平面配置圖

CUB3.1

CUB3-L10 MECHICAL EQUIPMENT&PIPE LAYOUT

DESIGNED : DRAWN : CHECKED :

DATE: 2025/08/17 JOB NO.: SCALE: 1/40 @A3 size

DRAWING NO. **DE MMTN C3 B003 M CHWT 31 10** RE **5**

DE_MMTN_C3_B002_M_CHWT_2L10 A

[SHEET PURPOSE] SHEET: 1 SIZE: 11x17