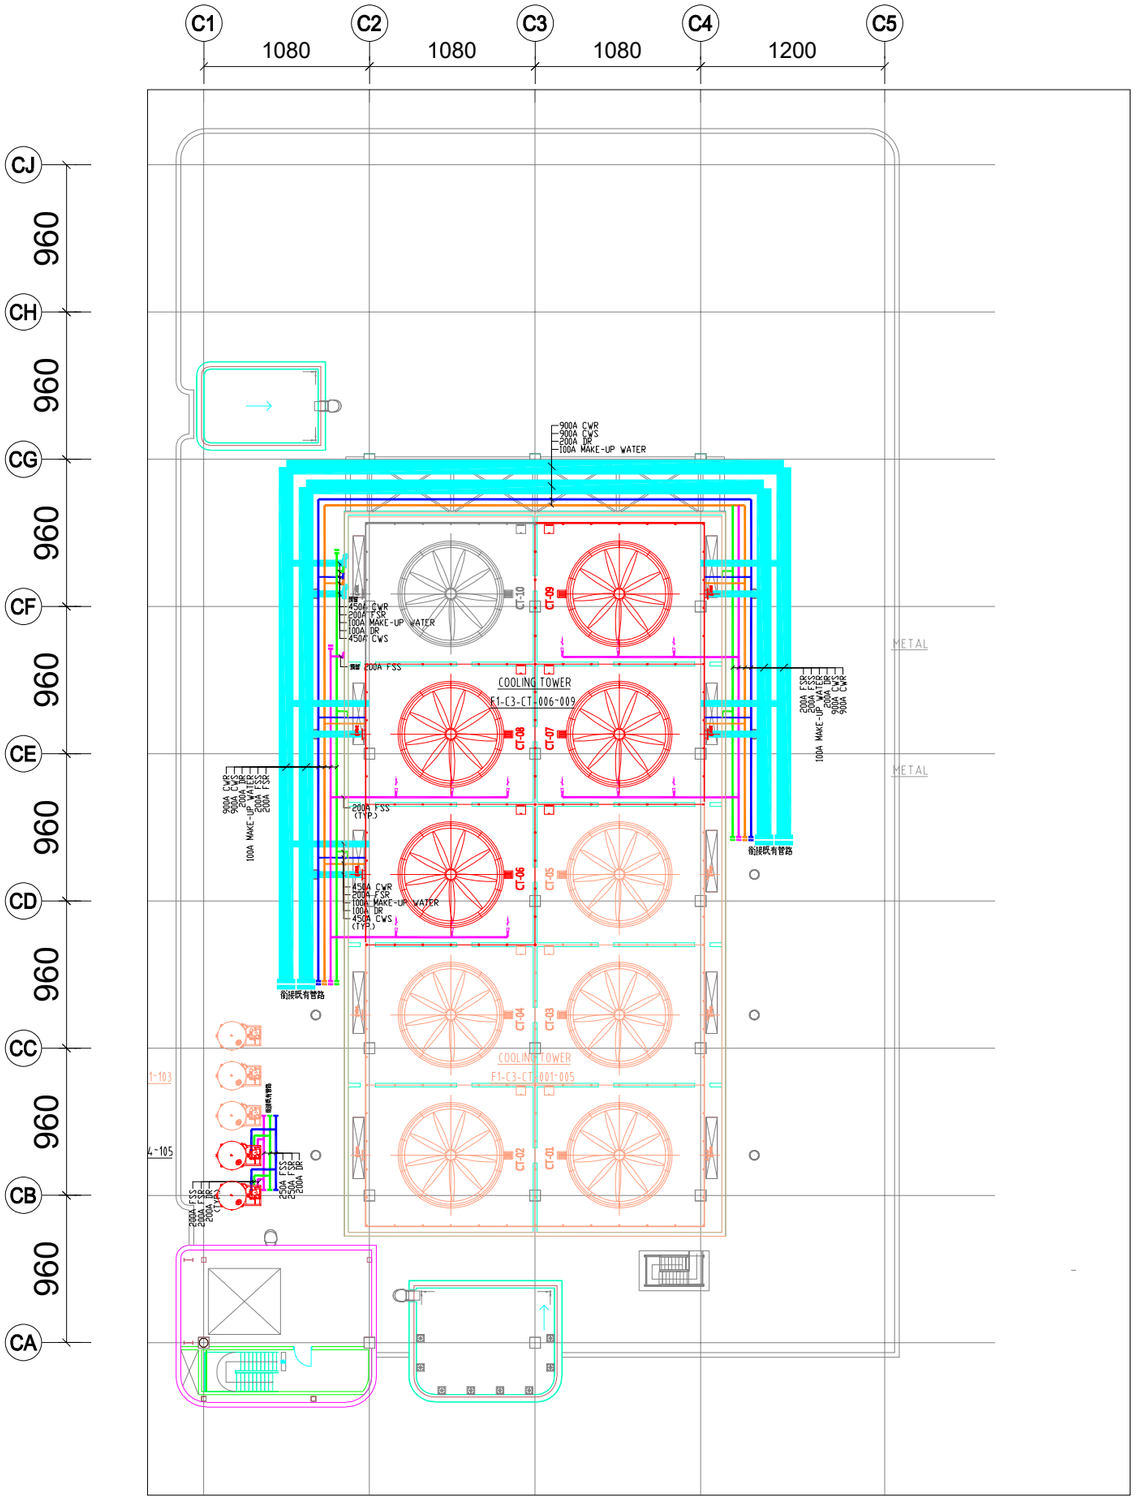



OWNER / DEVELOPER

micron

ARCHITECTURAL CONSULTANT

QUO 陳昆豐建築師事務所

CIVIL & STRUCTURAL CONSULTANT

禾森工程顧問有限公司

MECHANICAL & ELECTRICAL CONSULTANT & CONTRACTOR

YKE 洋基工程股份有限公司 YANKEY Engineering Co.,Ltd

SUB-CONTRACTOR

PROJECT ADDRESS

KEY PLAN

| REV | DATE | DESCRIPTION | ISSUED BY |
|---|---|---|---|
| | | | |

Revisions

PROJECT TITLE

美光台南廠188K增建工程

MECH

PROJECT PHASE

Concept Design

DRAWING TITLE

**DE_MMTN_C3_B002_M_CHWT_2LR2**

**CUB RF 沙濾管路平面圖**

**LR2 MECHICAL FLOW DIAGRAM-COOLING TOWER FILTRATION LAYOUT**

| DESIGNED : | DRAWN : | CHECKED : |
|---|---|---|
| DATE : 2025/08/17 | JOB NO. : | SCALE : |

DRAWING NO. **DE_MMTN_C3_B002_M_CHWT_2LR2** REV **A**

SHEET: SIZE

[SHEET PURPOSE]