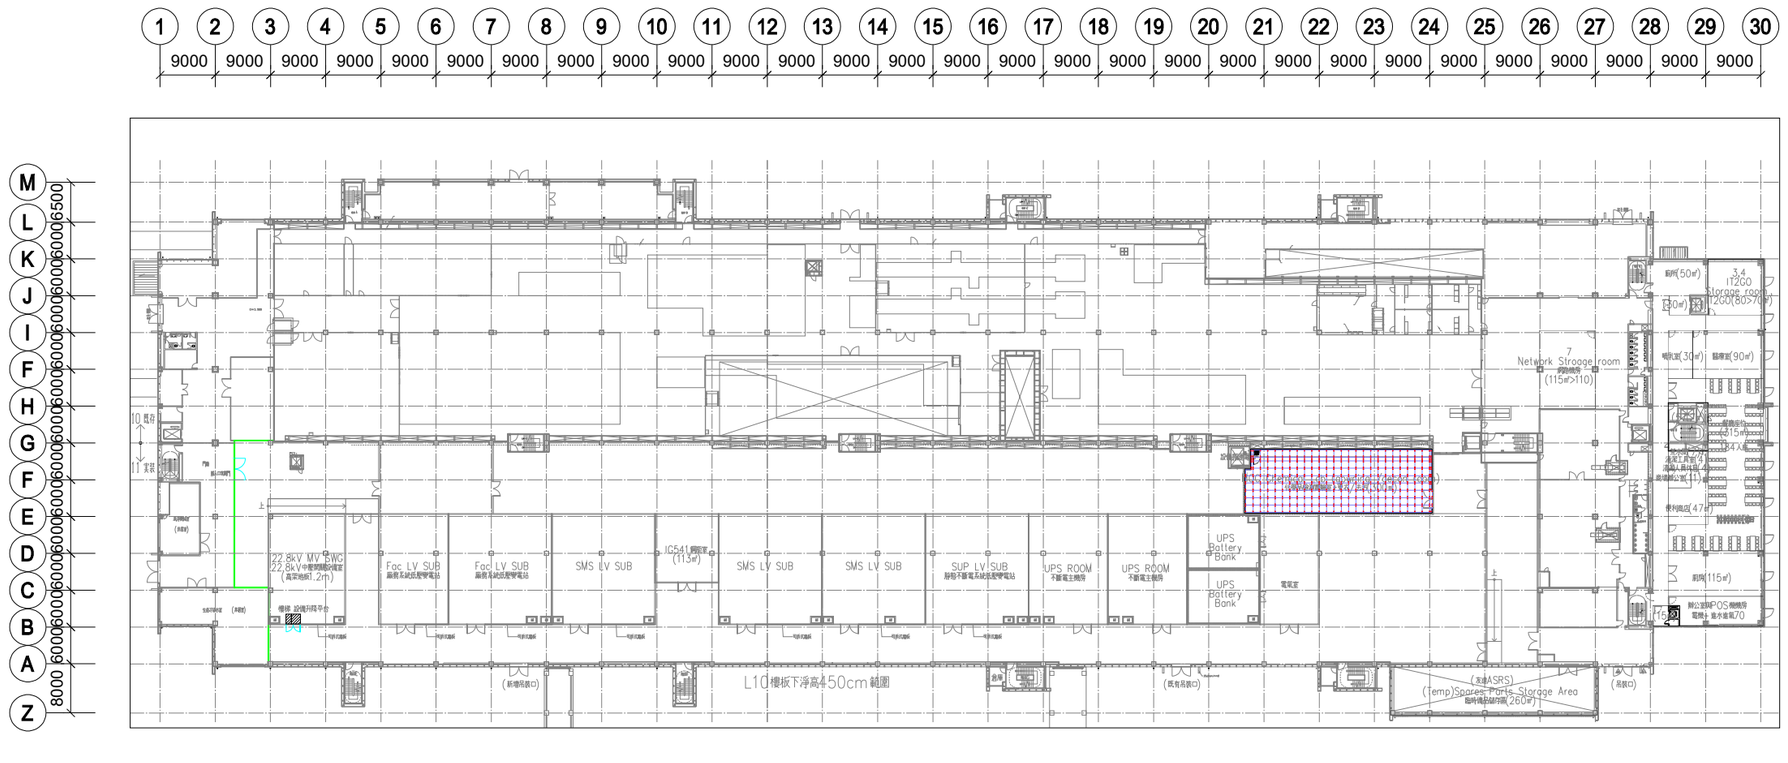


SYMBOL	DESCRIPTION
	CEILING GRID 天花板 1200mm x 1200mm CH=4200mm
⊗	天花板吊點(離天花板中心 150mm)

OWNER / DEVELOPER

micron

ARCHITECTURAL CONSULTANT

QUO 陳昆豐建築師事務所

CIVIL & STRUCTURAL CONSULTANT

禾森工程顧問有限公司

MECHANICAL & ELECTRICAL CONSULTANT & CONTRACTOR

YKE 洋基工程股份有限公司 YANKEY Engineering Co.,Ltd

SUB-CONTRACTOR

PROJECT ADDRESS

KEY PLAN

REV	DATE	DESCRIPTION	ISSUED BY

Revisions

PROJECT TITLE

美光台南廠188K增建工程

MECH

PROJECT PHASE

Concept Design

DRAWING TITLE

DE_MMTN_F1_B002_B_CEIL_2L20

F1 L20 天花板平面配置圖

N-Fab L20 CEIL LAYOUT

DESIGNED : DRAWN : CHECKED :

DATE : 2025/08/22 JOB NO. : SCALE : **A3:1/1000**

DRAWING NO. REV

DE_MMTN_F1_B002_B_CEIL_2L20 **A**

[SHEET PURPOSE] SHEET: SIZE