
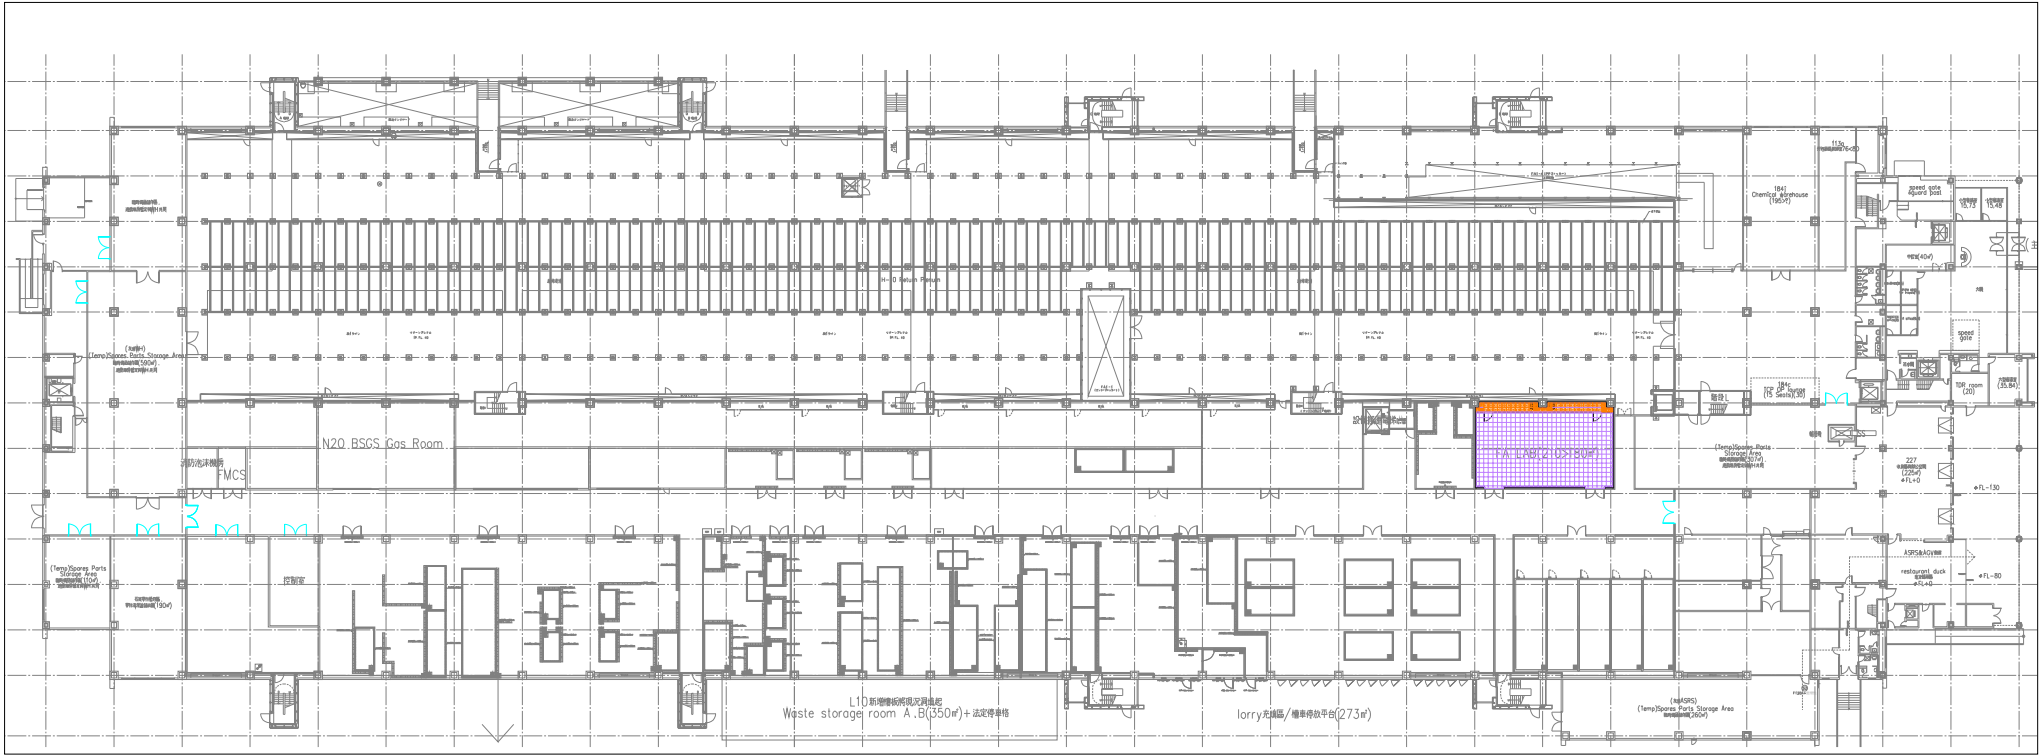
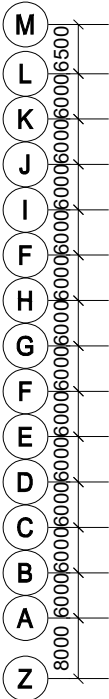


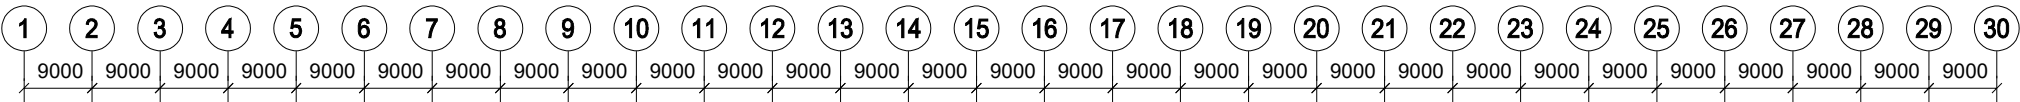

| 圖 示 | 說 明                          |
|-----|------------------------------|
|     | 600×600 高架地板 H=550mm (1500型) |
|     | 600×600 17% 蜂巢板全面積 45%       |
|     | 600×600 格柵板 H=550mm (1500型)  |

OWNER / DEVELOPER  
**micron**™

ARCHITECTURAL CONSULTANT  
**QUO** 陳昆豐建築師事務所

CIVIL & STRUCTURAL CONSULTANT  
 禾森工程顧問有限公司

MECHANICAL & ELECTRICAL CONSULTANT & CONTRACTOR  
 洋基工程股份有限公司  
YANKEY Engineering Co.,Ltd

SUB-CONTRACTOR

PROJECT ADDRESS

KEY PLAN

|     |      |                          |           |
|-----|------|--------------------------|-----------|
|     |      |                          |           |
|     |      |                          |           |
| REV | DATE | DESCRIPTION<br>Revisions | ISSUED BY |

PROJECT TITLE  
**美光台南廠188K增建工程**  
**MECH**

PROJECT PHASE  
Concept Design

DRAWING TITLE  
**DE\_MMTN\_F1\_B002\_B\_RAFL\_2L10**  
**F1 L10 高架地板平面配置圖**  
**N-Fab L10 RF LAYOUT**

DESIGNED:      DRAWN:      CHECKED:      DATE: 2025/08/22      JOB NO.:      SCALE: **A3:1/1000**

DRAWING NO. **DE\_MMTN\_F1\_B002\_B\_RAFL\_2L10** REV **A**

[SHEET PURPOSE] SHEET: SIZE