



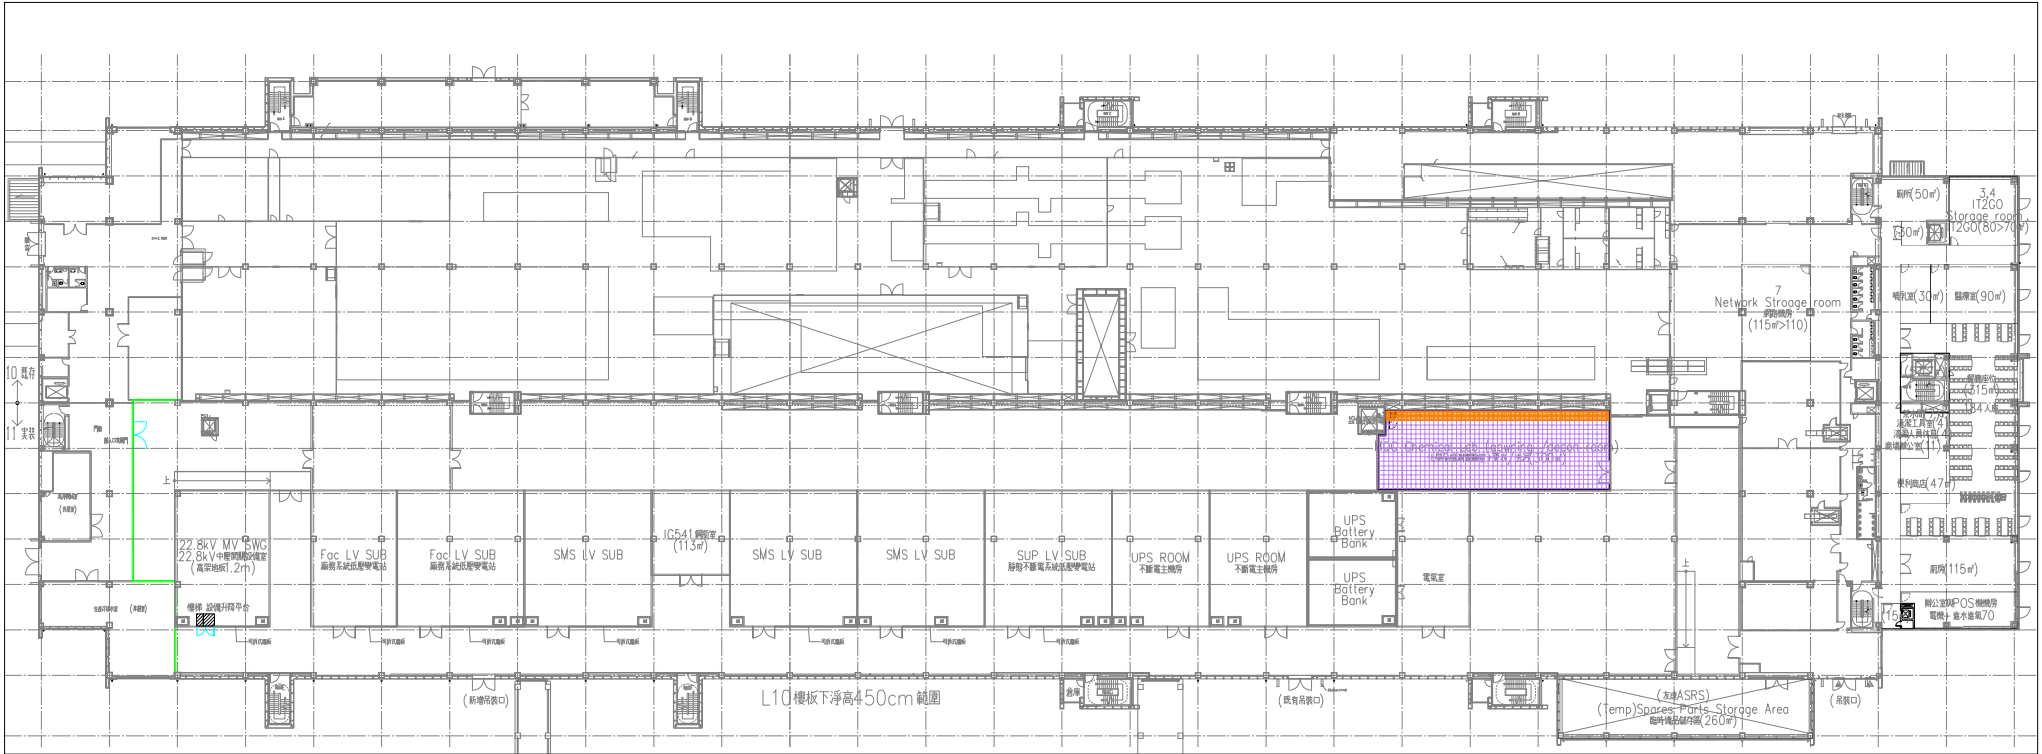


圖 示	說 明
	600×600 高架地板 H=550mm (1500型)
	600×600 17% 蜂巢板全面積 45%
	600×600 格柵板 H=550mm (1500型)

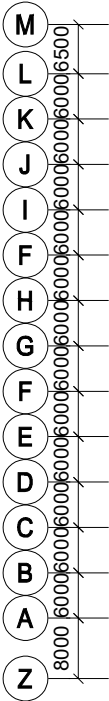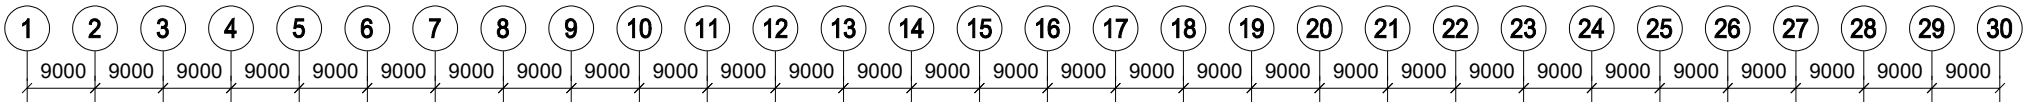

ARCHITECTURAL CONSULTANT
QUO 陳昆豐建築師事務所

CIVIL & STRUCTURAL CONSULTANT
禾森工程顧問有限公司

MECHANICAL & ELECTRICAL CONSULTANT & CONTRACTOR
YKE 洋基工程股份有限公司
YANKEY Engineering Co.,Ltd

SUB-CONTRACTOR

PROJECT ADDRESS

KEY PLAN

REV	DATE	DESCRIPTION Revisions	ISSUED BY

PROJECT TITLE
美光台南廠188K增建工程
MECH

PROJECT PHASE
Concept Design

DRAWING TITLE
DE_MMTN_F1_B002_B_RAFL_2L20
F1 L20 高架地板平面配置圖
N-Fab L20 RF LAYOUT

DESIGNED: DRAWN: CHECKED: DATE: 2025/08/22 JOB NO.: SCALE: A3:1/1000

DRAWING NO. DE_MMTN_F1_B002_B_RAFL_2L20 REV A

[SHEET PURPOSE] SHEET: SIZE