
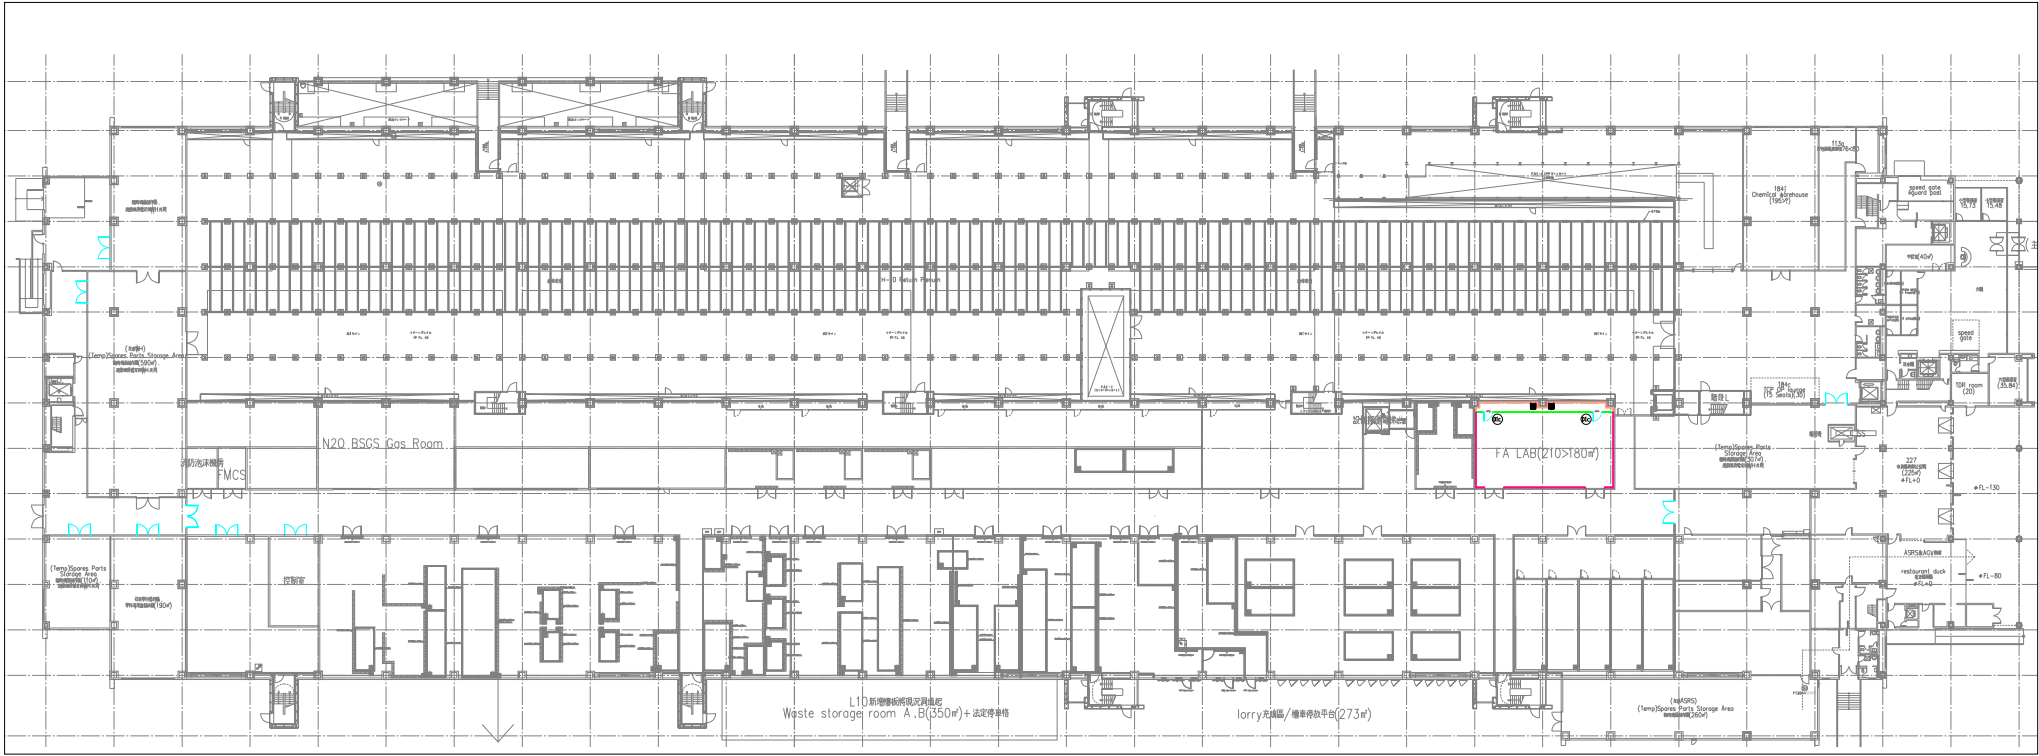
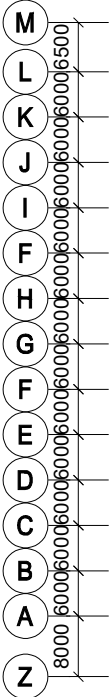


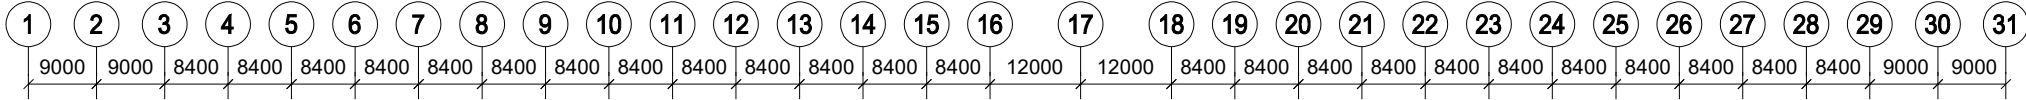

| MATERIAL                                | SYMBOL |
|-----------------------------------------|--------|
| 鋁蜂窩庫板隔間 (t=50mm)<br>單面抗靜電 H=3000mm      |        |
| 防火二小時岩棉庫板隔間 (t=100mm)<br>單面抗靜電 H=5000mm |        |
| 註: RF 高架地板完整面起算,<br>庫板寬度為1200mm.        |        |

| DOOR SYMBOL & LEGEND |        |                               |
|----------------------|--------|-------------------------------|
| 編號                   | SYMBOL | DESCRIPTION (含門框尺寸)           |
| ①1C                  |        | 單開庫板門 1200W x 2400H 把手型 圓形拉環鎖 |

| EQUIPMENT SYMBOL & LEGEND |                     |         |
|---------------------------|---------------------|---------|
| SYMBOL                    | DESCRIPTION單位: mm   | REMARKS |
|                           | 爬梯(STAINLESS STEEL) | LAD     |

OWNER / DEVELOPER  
**micron**™

ARCHITECTURAL CONSULTANT  
**QUO** 陳昆豐建築師事務所

CIVIL & STRUCTURAL CONSULTANT  
 禾森工程顧問有限公司

MECHANICAL & ELECTRICAL CONSULTANT & CONTRACTOR  
 洋基工程股份有限公司  
YANKEY Engineering Co.,Ltd

SUB-CONTRACTOR

PROJECT ADDRESS

KEY PLAN

| REV | DATE | DESCRIPTION<br>Revisions | ISSUED BY |
|-----|------|--------------------------|-----------|
|     |      |                          |           |
|     |      |                          |           |
PROJECT TITLE  
**美光台南廠188K增建工程**

PROJECT PHASE  
**MECH**  
Concept Design

DRAWING TITLE  
**DE\_MMTN\_F1\_B002\_D\_PRTN\_2L10**  
**F1 L10 隔間平面配置圖**  
**N-Fab L10 PA LAYOUT**

DESIGNED:      DRAWN:      CHECKED:      DATE: 2025/08/22      JOB NO.:      SCALE: **A3:1/1000**

DRAWING NO. **DE\_MMTN\_F1\_B002\_D\_PRTN\_2L10** REV **A**

[SHEET PURPOSE]      SHEET:      SIZE