
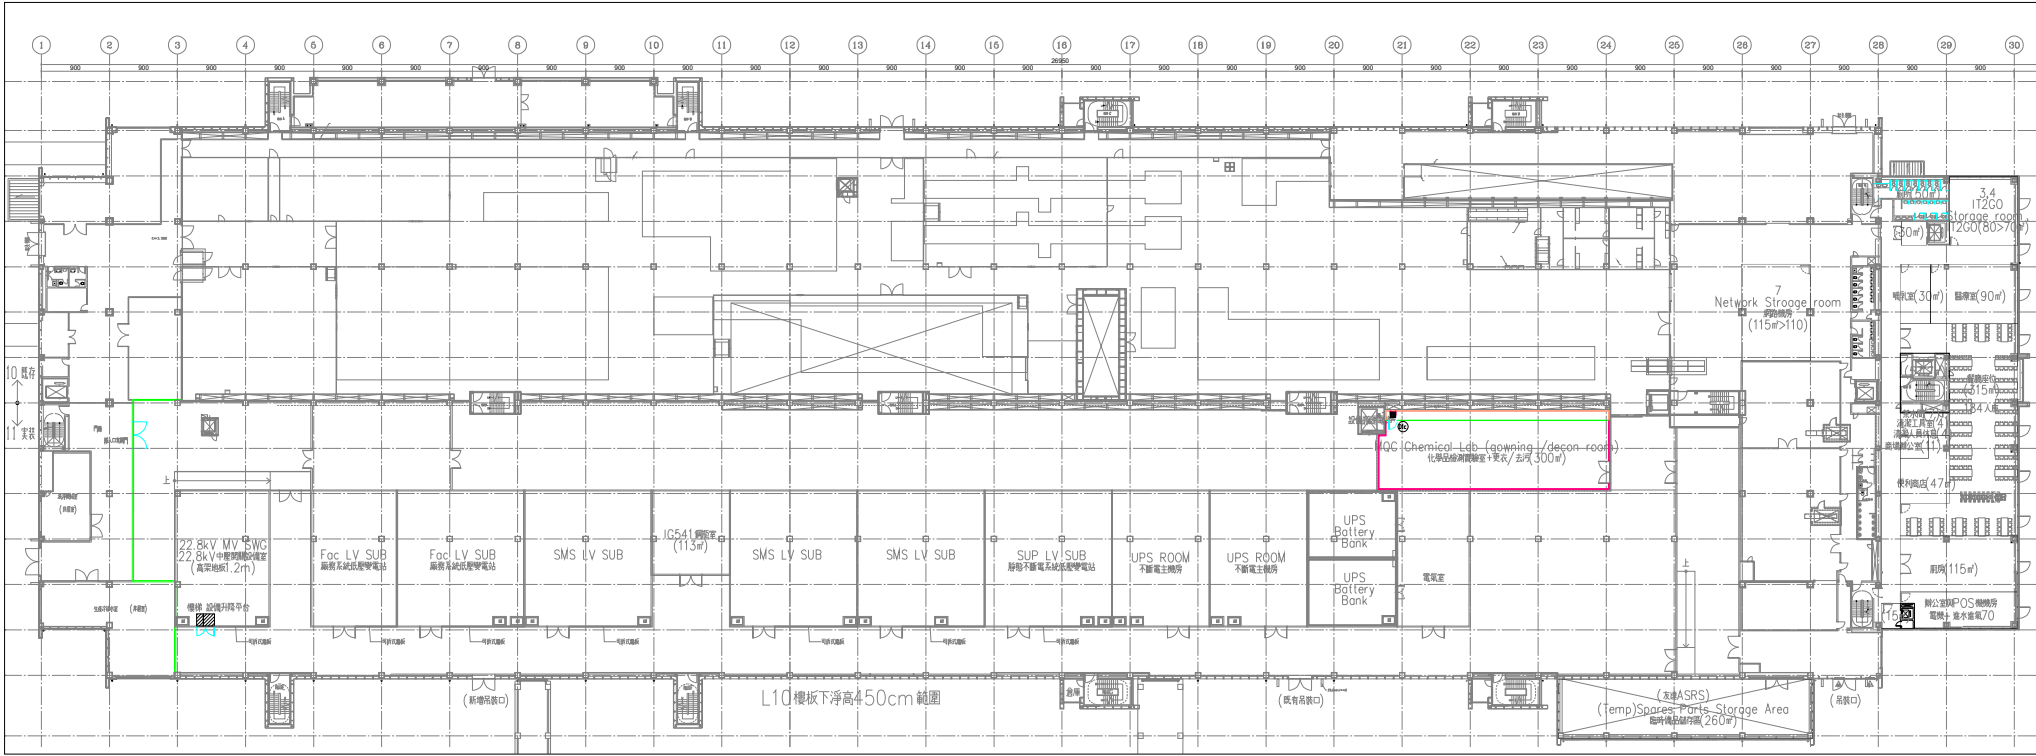
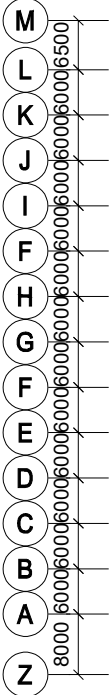


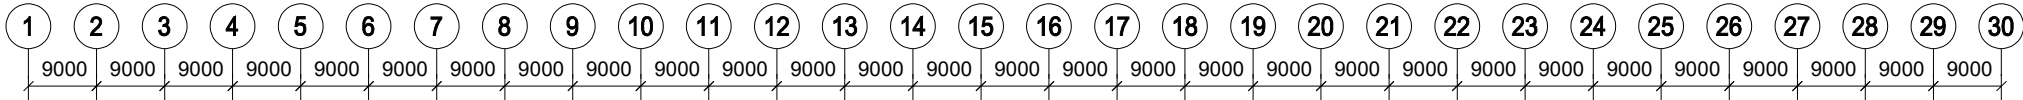

MATERIAL	SYMBOL
鋁蜂窩庫板隔間 (t=50mm) 單面抗靜電 H=3000mm	
防火二小時岩棉庫板隔間 (t=100mm) 單面抗靜電 H=5000mm	
註: RF 高架地板完整面起算, 庫板寬度為1200mm.	

DOOR SYMBOL & LEGEND		
編號	SYMBOL	DESCRIPTION (含門框尺寸)
DIC		單開庫板門 1200W x 2400H 把手型 圓形拉環鎖

EQUIPMENT SYMBOL & LEGEND		
SYMBOL	DESCRIPTION單位:mm	REMARKS
	爬梯<STAINLESS STEEL>	LAD

OWNER / DEVELOPER
micron™

ARCHITECTURAL CONSULTANT
QUO 陳昆豐建築師事務所

CIVIL & STRUCTURAL CONSULTANT
森 禾森工程顧問有限公司

MECHANICAL & ELECTRICAL CONSULTANT & CONTRACTOR
YKE 洋基工程股份有限公司
YANKEY Engineering Co.,Ltd

SUB-CONTRACTOR

PROJECT ADDRESS

KEY PLAN

REV	DATE	DESCRIPTION Revisions	ISSUED BY

PROJECT TITLE
美光台南廠188K增建工程
MECH

PROJECT PHASE
Concept Design

DRAWING TITLE
DE_MMTN_F1_B002_D_PRTN_2L20
F1 L20 隔間平面配置圖
N-Fab L20 PA LAYOUT

DESIGNED: DRAWN: CHECKED: DATE: 2025/08/22 JOB NO.: SCALE: **A3:1/1000**

DRAWING NO. **DE_MMTN_F1_B002_D_PRTN_2L20** REV **A**

[SHEET PURPOSE] SHEET: SIZE