


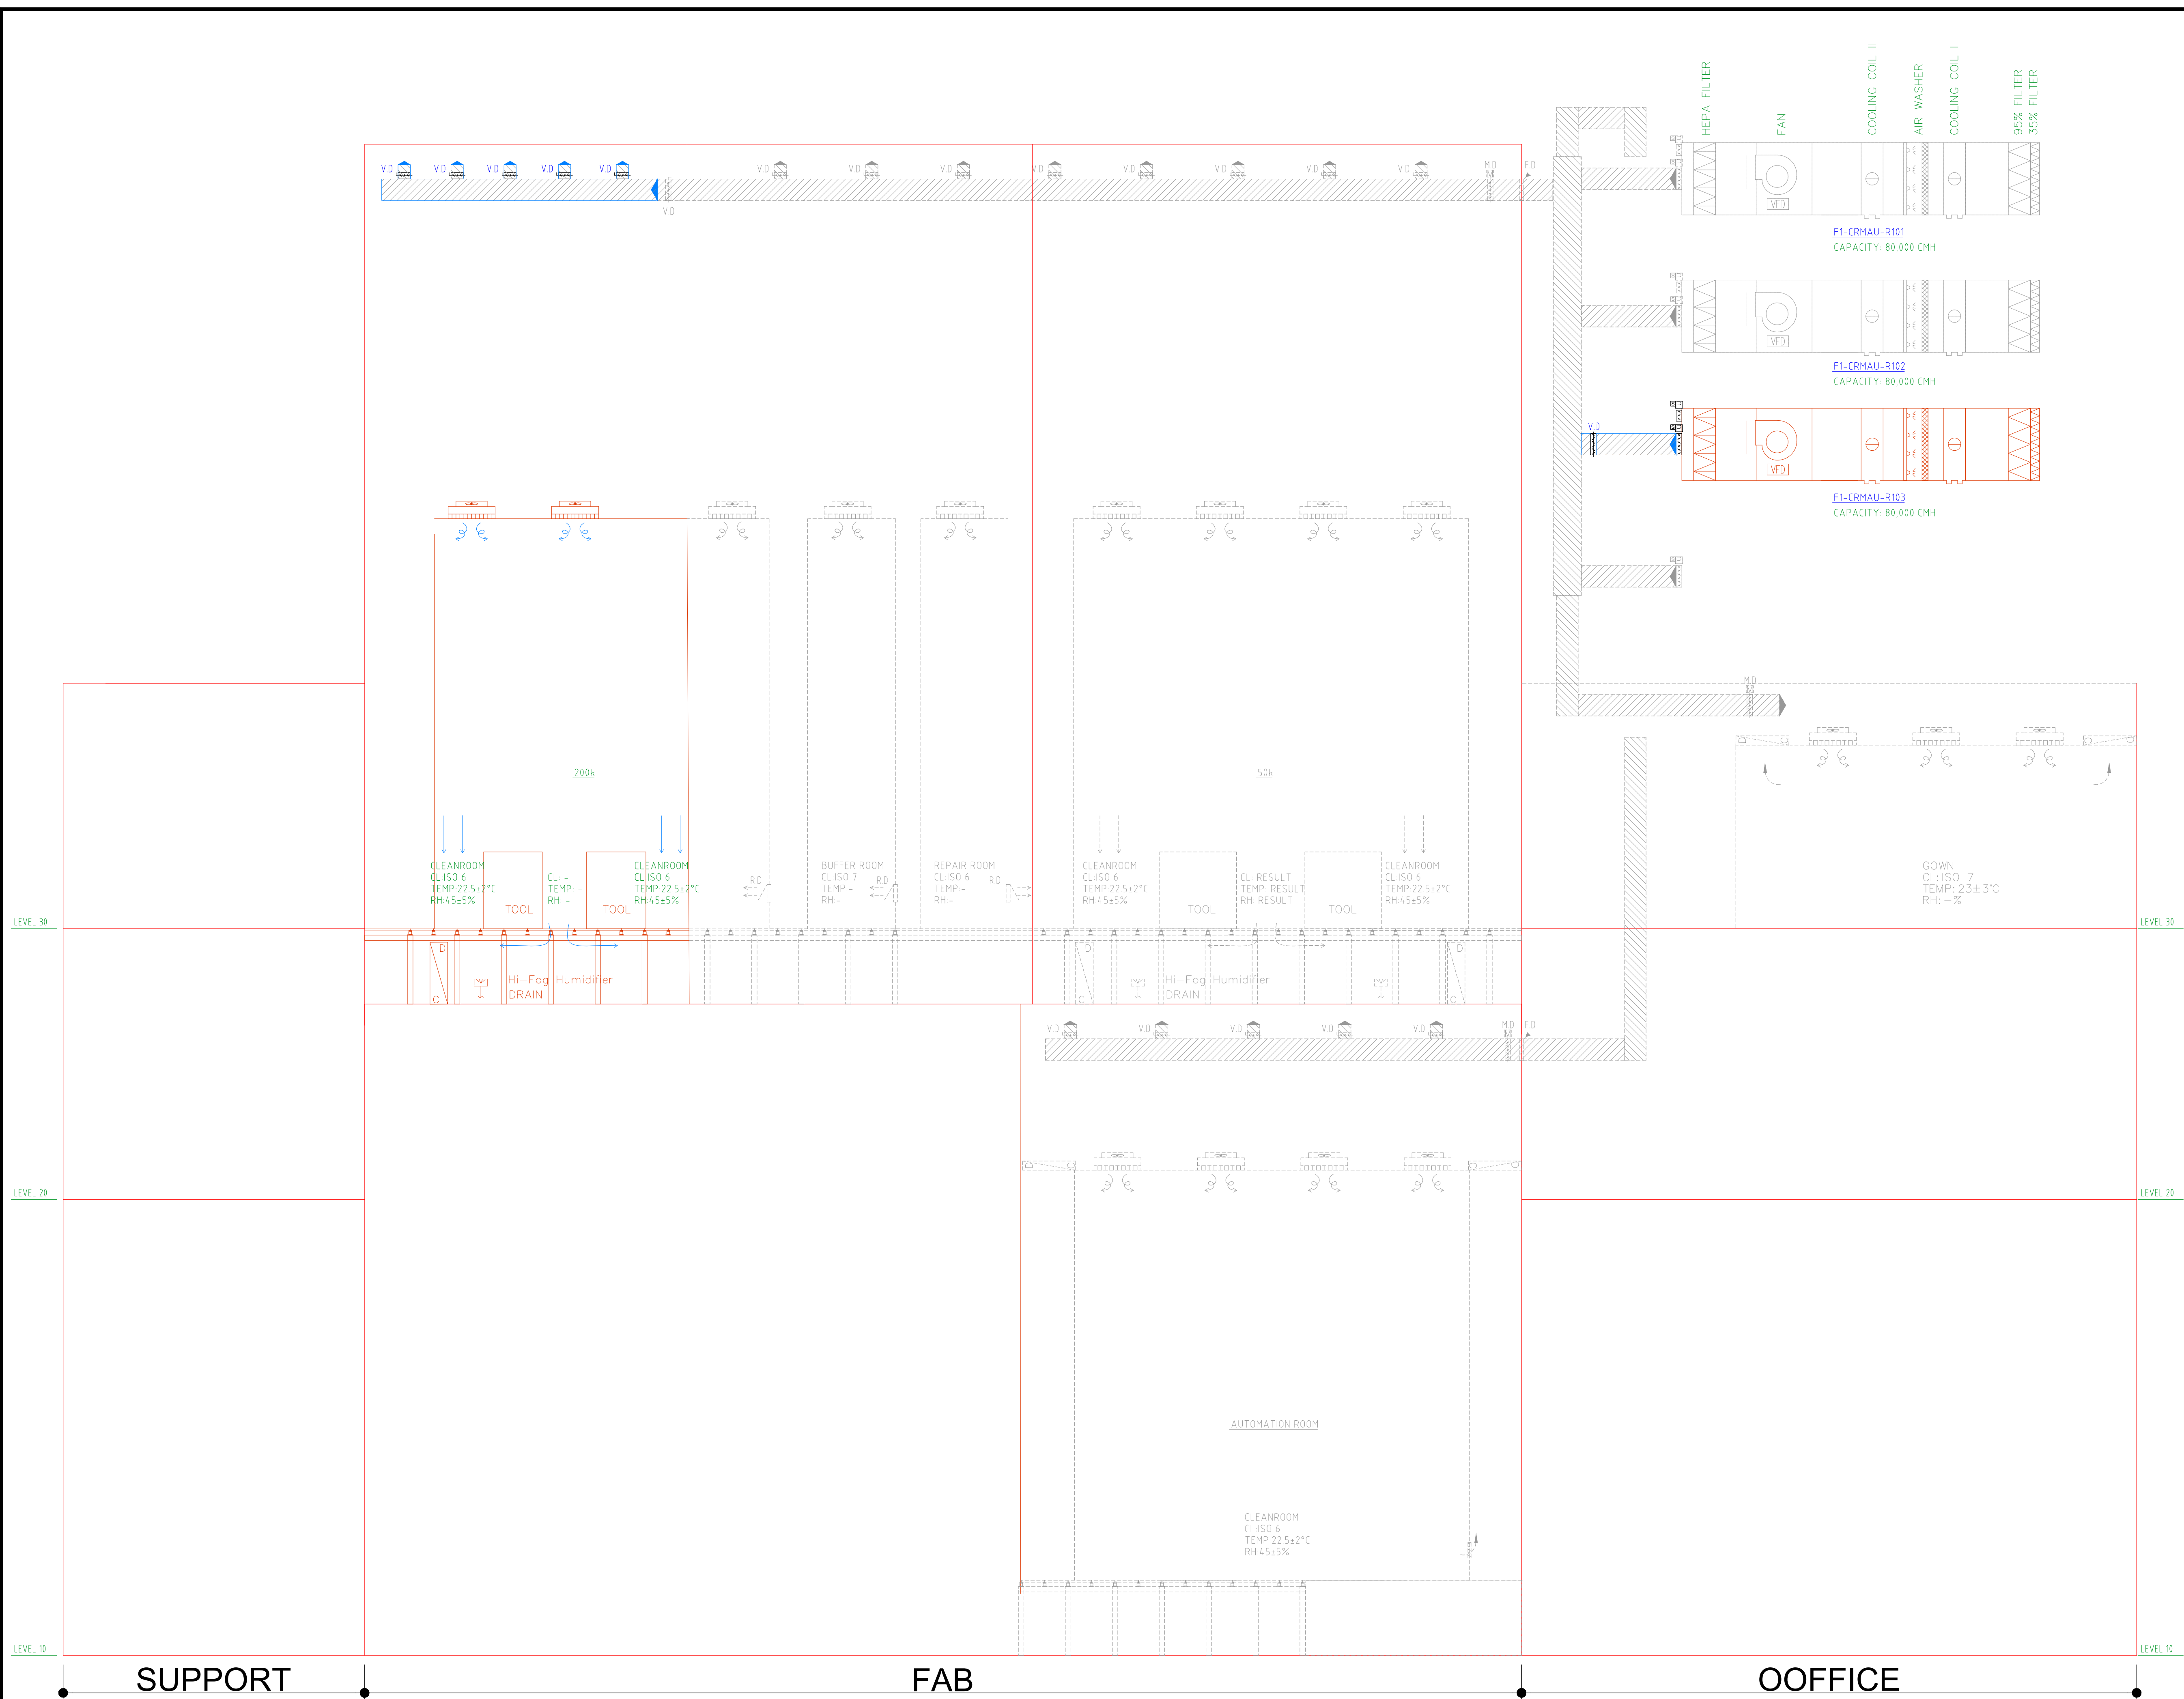

OWNER / DEVELOPER			
ARCHITECTS & PLANNERS 潘冀聯合建築師			
ARCHITECTURAL CONSULTANT			
CIVIL & STRUCTURAL CONSULTANT			
TEAM 群策工程股份有限公司			
MECHANICAL & ELECTRICAL CONSULTANT & CONTRACTOR			
 United Integrated Services 漢唐集成股份有限公司			
SUB-CONTRACTOR			
PROJECT ADDRESS			
KEY PLAN			
A	2025/01/02	REVIEW Drawing	
REV	DATE	DESCRIPTION	ISSUED BY
Revisions			
PROJECT TITLE			
Micron Falcon A Project (200K)			
PROJECT PHASE			
Concept Design			
DRAWING TITLE			
SYSTEM DIAGRAM - CR DUCTING SYSTEM - -			
DESIGNED : ELLIS		DRAWN : ELLIS	CHECKED : C.S.HU
DATE : 2024/11/20		JOB NO. :	SCALE : N.T.S
DRAWING NO.			
DE_F1_ALL_B001_MB_MECH_1001-00			
SHEET:			REV
			0
			SIZE A1