

OWNER / DEVELOPER

micron.

ARCHITECTURAL CONSULTANT

JJP ARCHITECTS
& PLANNERS **潘冀聯合建築師**

CIVIL & STRUCTURAL CONSULTANT

TEAM 群策工程股份有限公司


MECHANICAL & ELECTRICAL CONSULTANT & CONTRACTOR

uis 漢唐集成股份有限公司
United Integrated Services

SUB-CONTRACTOR

PROJECT ADDRESS

KEY PLAN

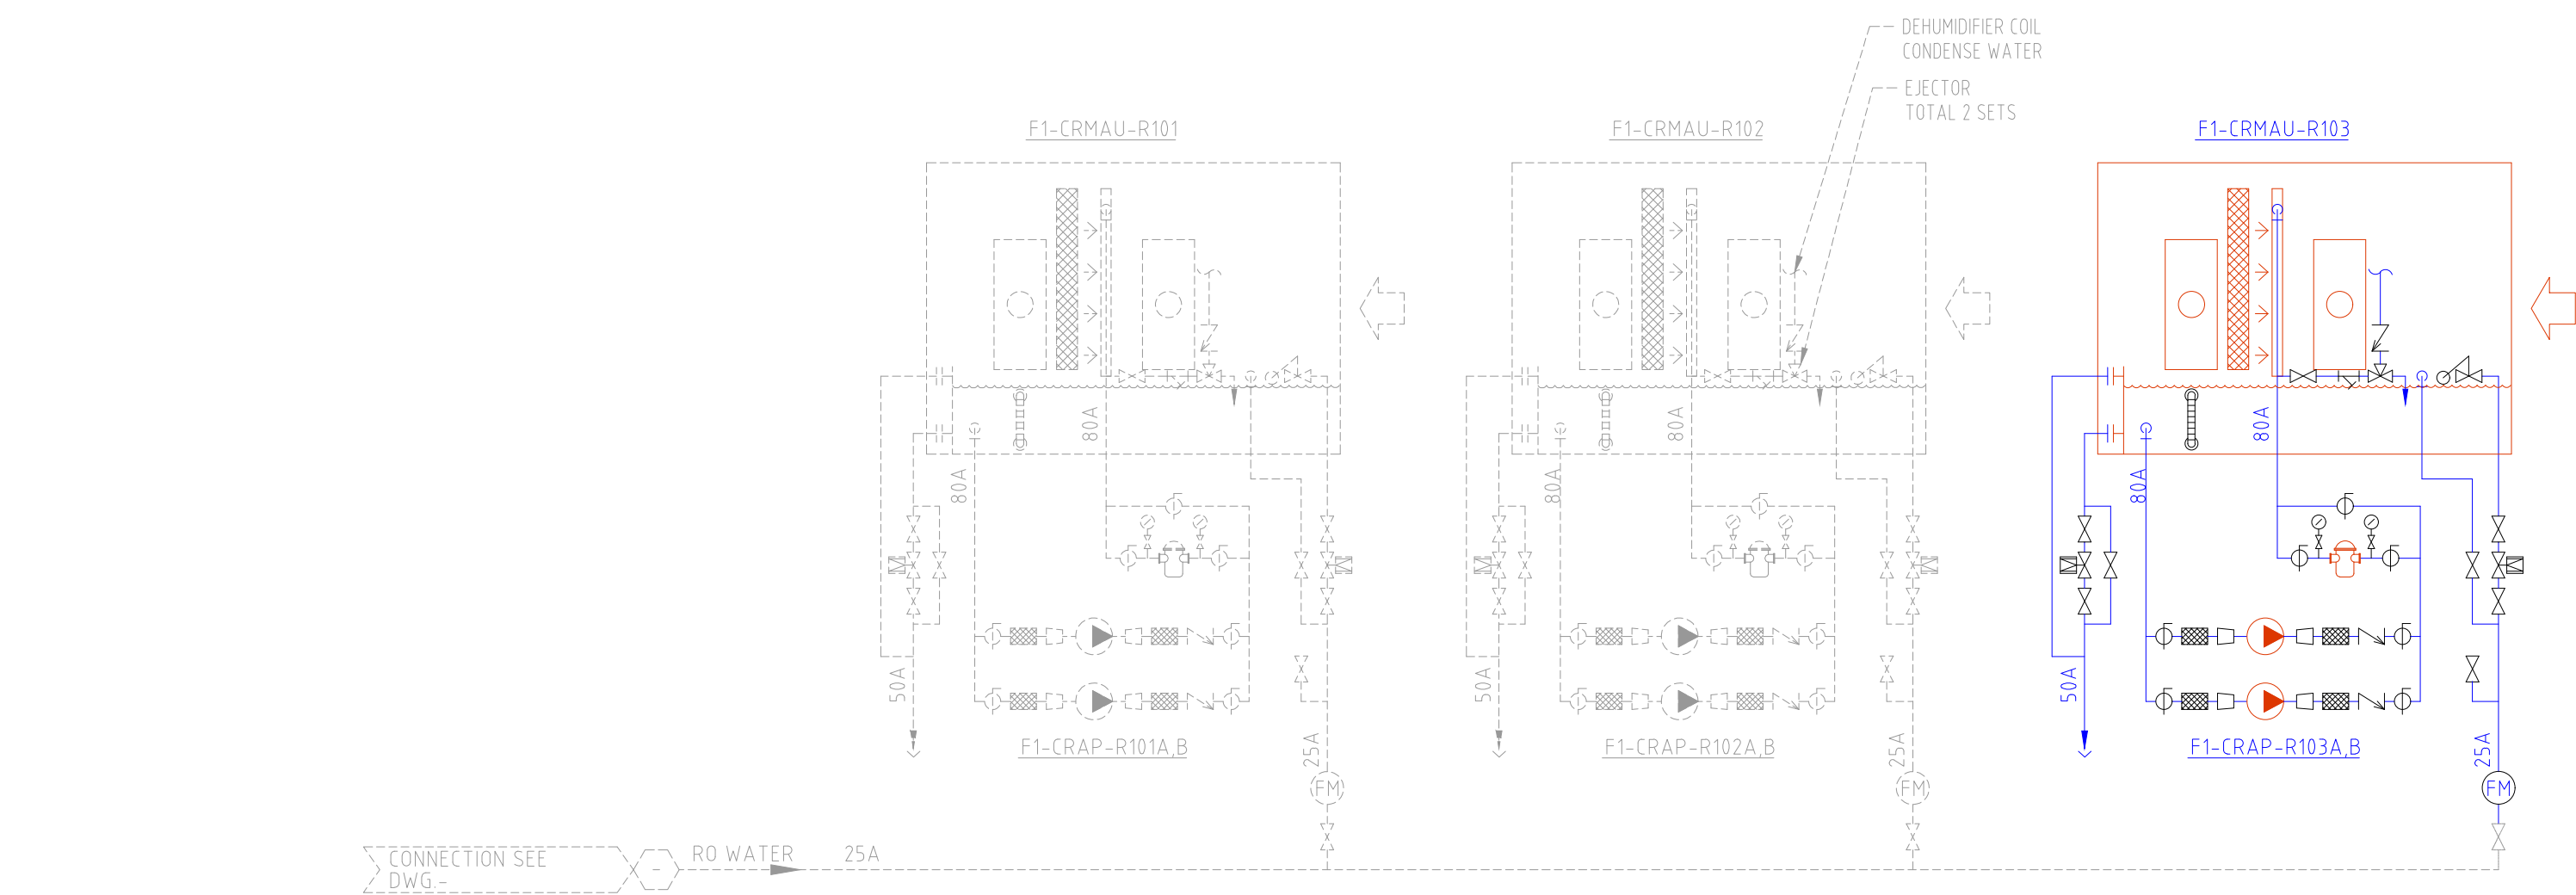

OFFICE 40

OFFICE 30

OFFICE 10

OFFICE

A	2025/01/02	REVIEW Drawing	
REV	DATE	DESCRIPTION	ISSUED BY
Revisions			

PROJECT TITLE

Micron Falcon A Project (200K)

PROJECT PHASE

Concept Design

DRAWING TITLE

SYSTEM DIAGRAM -
AMC AIR WASHER PIPING SYSTEM

DESIGNED : ELLIS

DRAWN :	ELLIS	CHECKED :	C.S.HU
---------	-------	-----------	--------

DATE : 2024/11/20

JOB NO. :	SCALE : N.T.S
-----------	---------------

DRAWING NO.

DE_F1_ALL_B001_MB_MECH_1004-00

				0
--	--	--	--	---

SHEET:	SIZE
	A1