
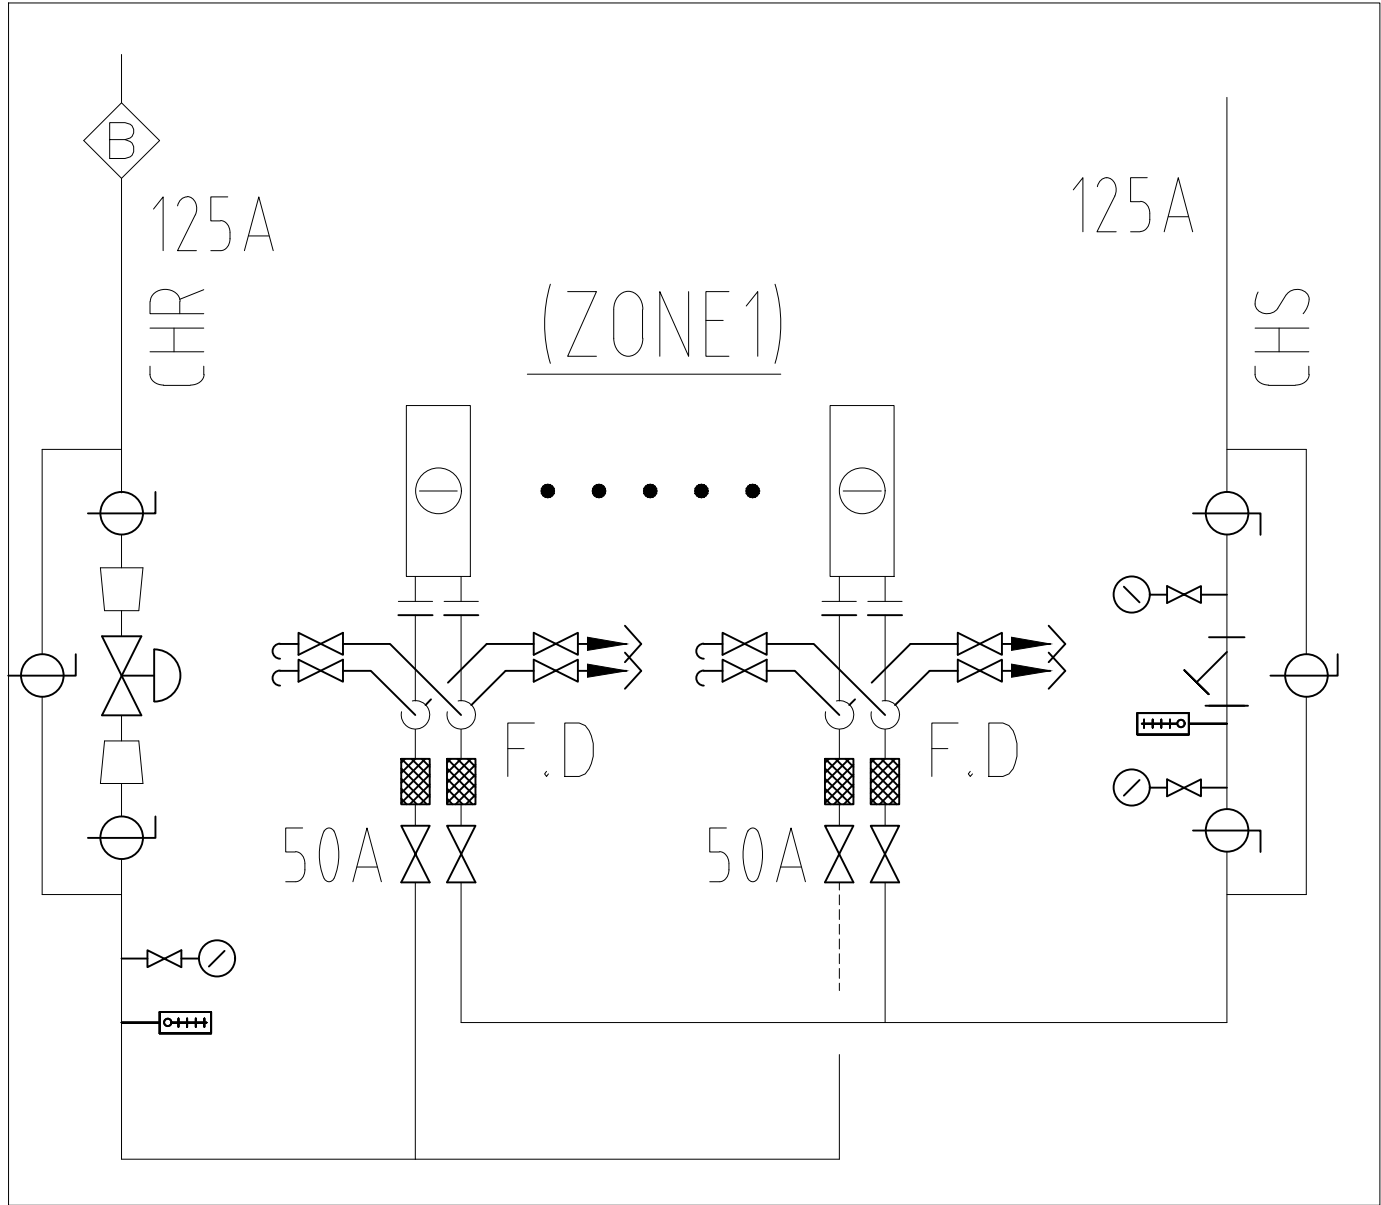


INFORMATION NOTICE: THE CONTENT OF THIS DOCUMENT IS SUBJECT TO INFORMATION AND OWNED BY MICRON CORPORATION AND IS PROTECTED BY COPYRIGHT LAWS AND RELATED LAWS. NO PART OF THIS DOCUMENT IS TO BE REPRODUCED, COPIED, OR TRANSMITTED IN ANY FORM OR BY ANY MEANS, WITHOUT THE WRITTEN PERMISSION OF MICRON CORPORATION. ANY VIOLATION OF THIS NOTICE SHALL BE SUBJECT TO LEGAL ACTION.

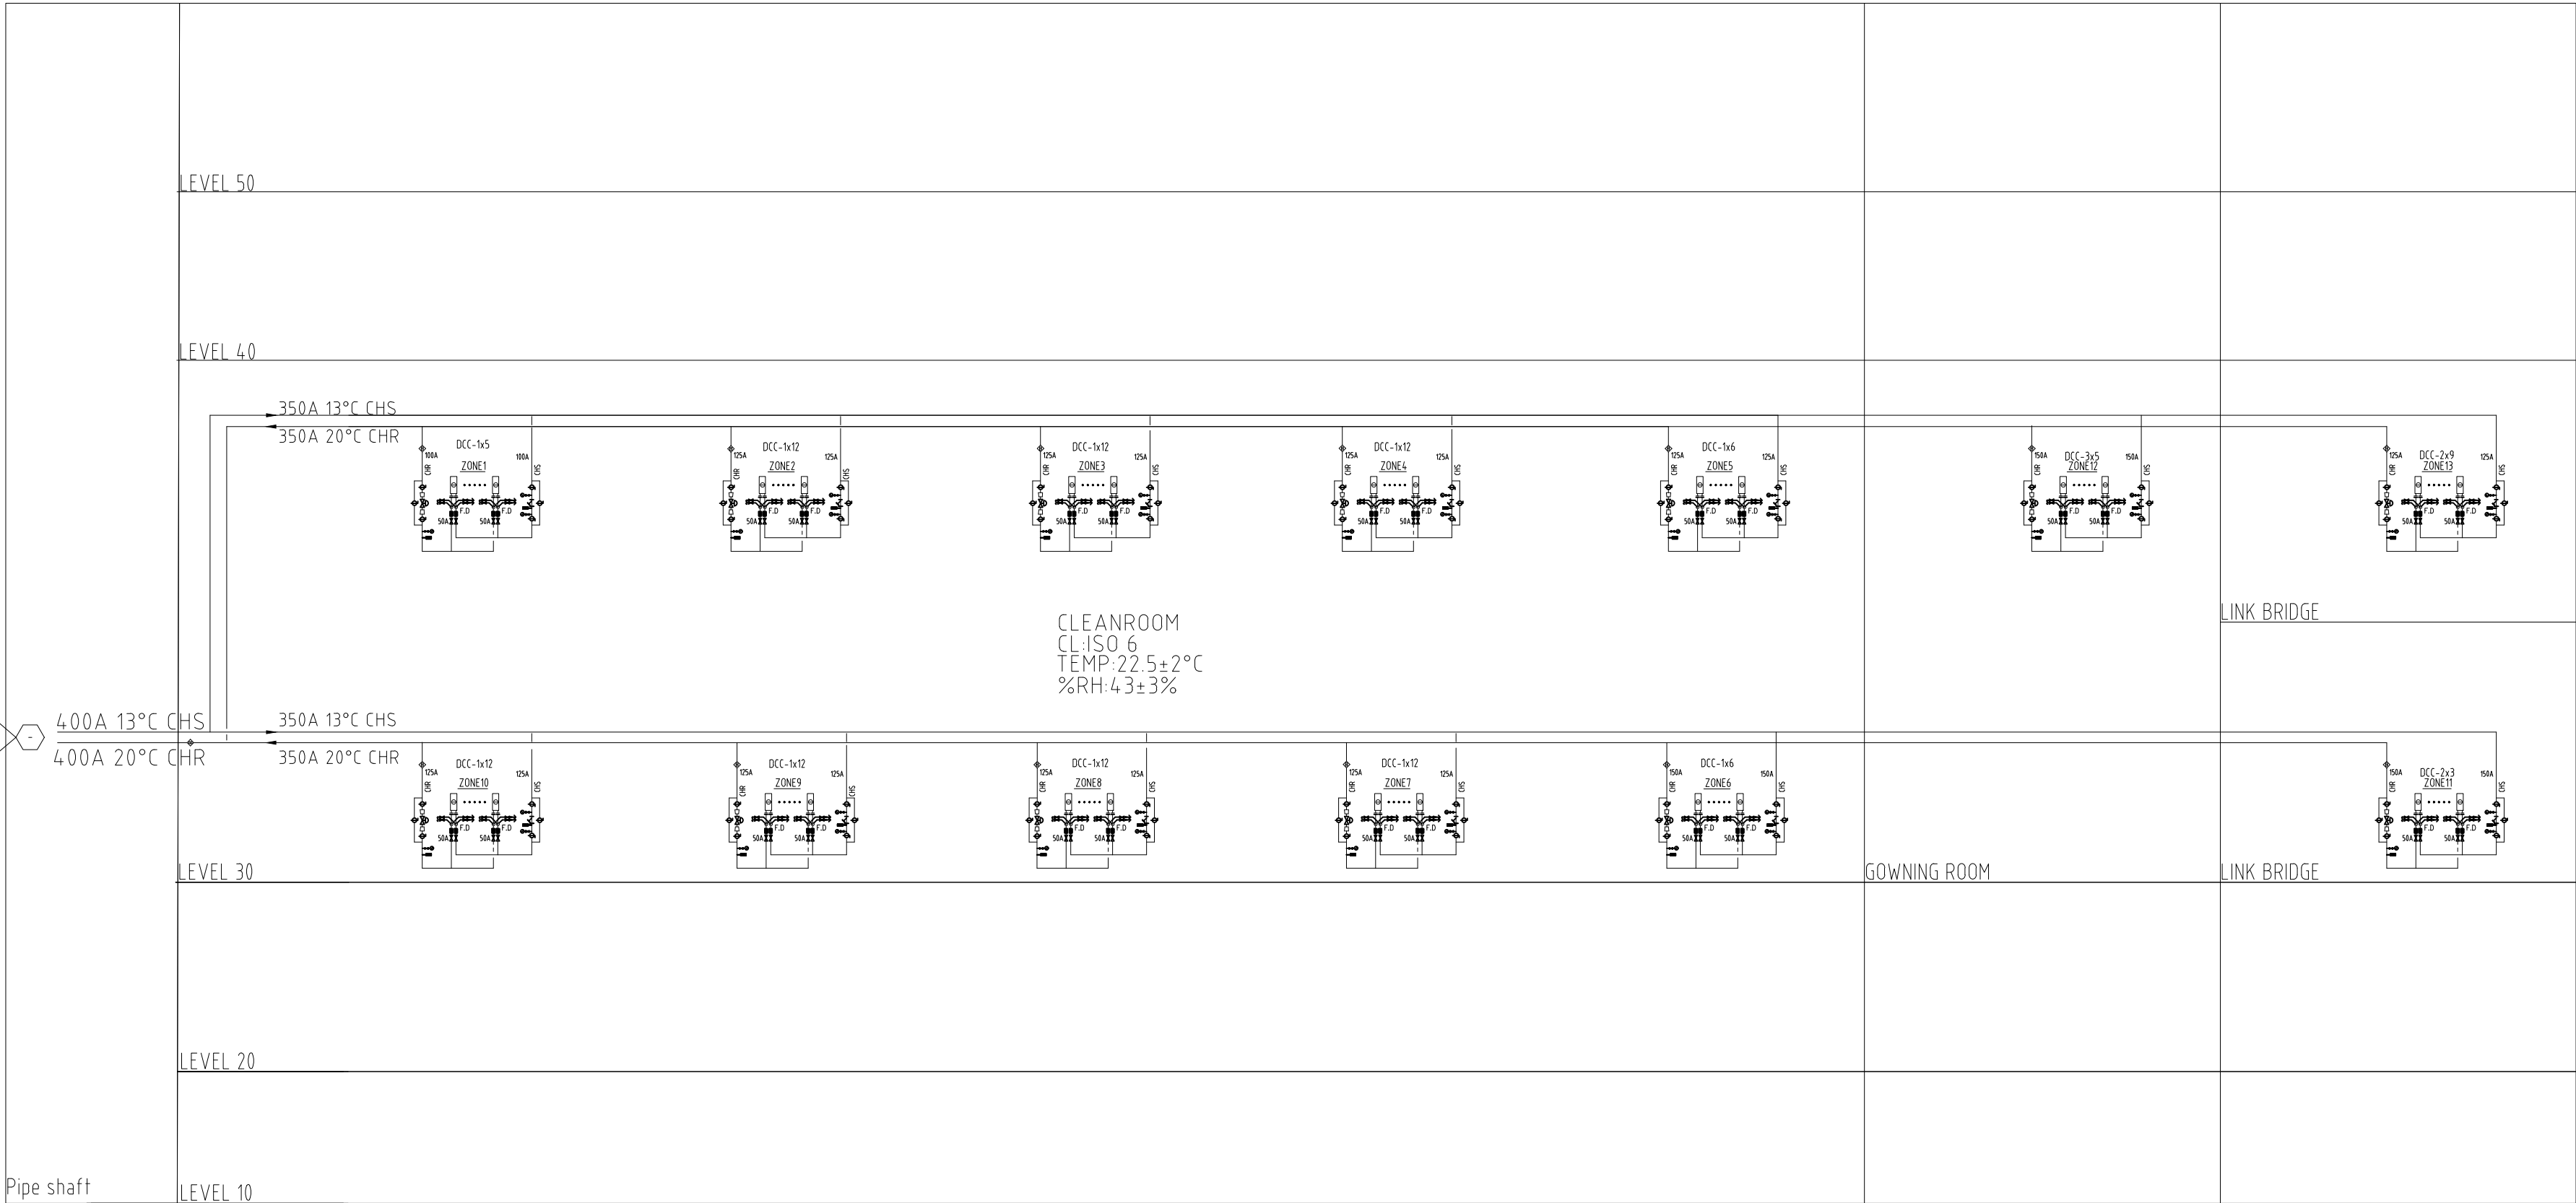

OWNER / DEVELOPER

ARCHITECTURAL CONSULTANT

CIVIL & STRUCTURAL CONSULTANT

MECHANICAL & ELECTRICAL CONSULTANT

DESIGN MANAGER

CTCI Singapore Pte. Ltd.

PROJECT ADDRESS

North Coast Drive, Singapore

KEY PLAN

Secret
R3
Level

FOR REVIEW

REV	DATE	DESCRIPTION	ISSUED BY
Revisions			

PROJECT TITLE

Micron F10E Probe Project

PROJECT PHASE

A&E

DRAWING TITLE

Flow Diagram_
DCC PIPING System F10E1

DESIGNED :	設計者	DRAWN :	作者	CHECKED :	審圖員	
DATE :	01/14/26	JOB NO. :		SCALE :		
Micron DRAWING NO.	F01-F10E-PFD-F10E1-00-K-103				REV B	
CTCI DRAWING NO.						
Reference Model						
A0~A999 or Vendor					SHEET: 1 OF 1	SIZE A1