
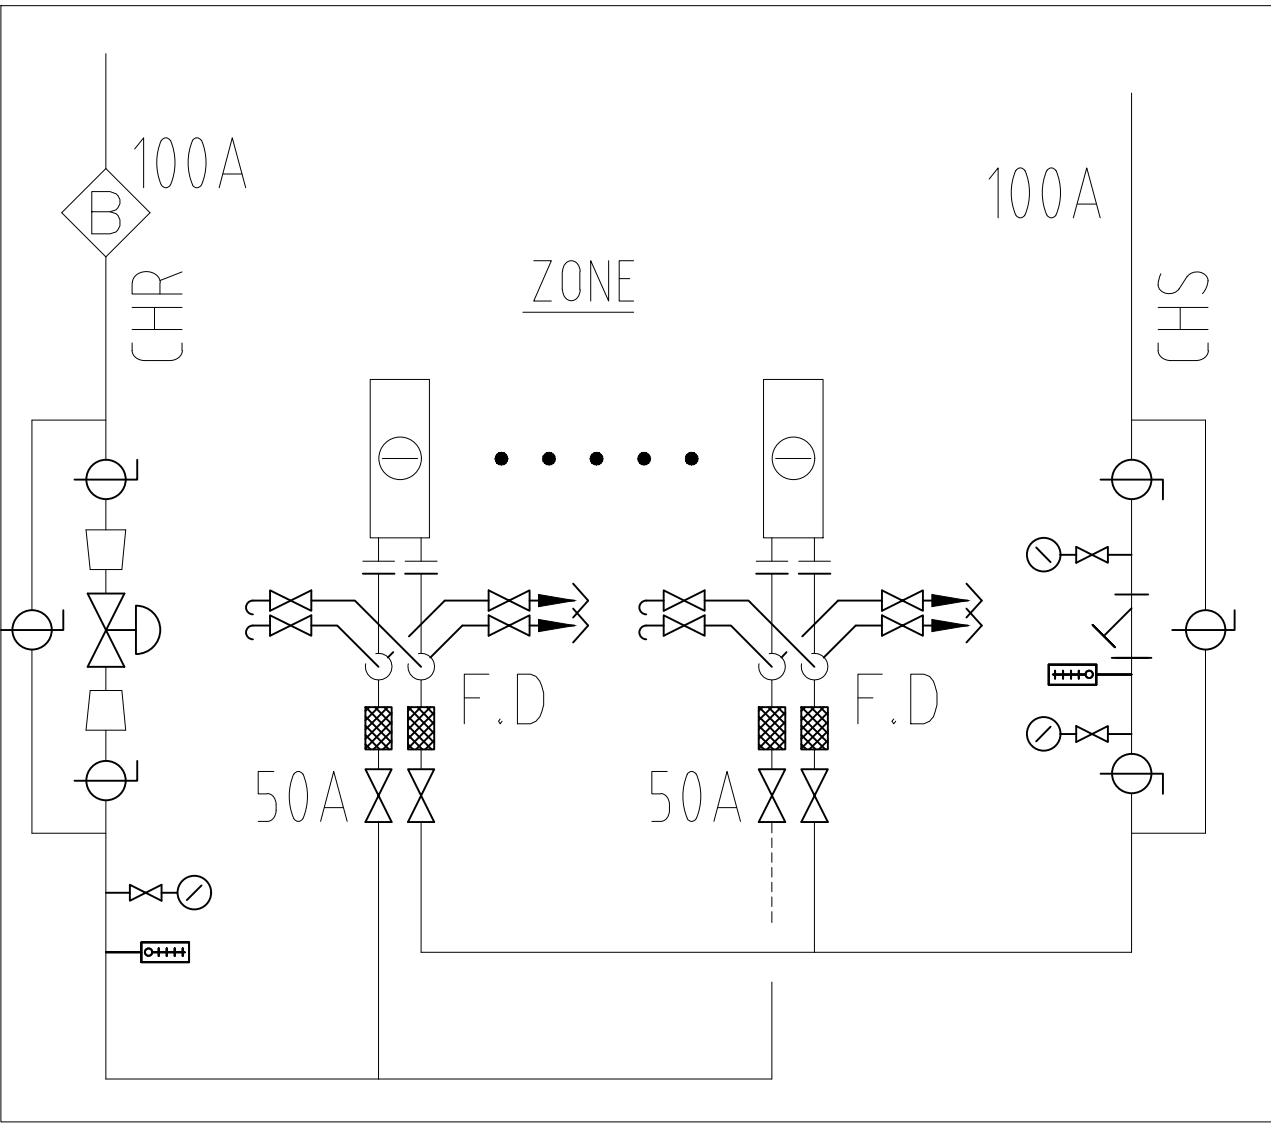


INFORMATION NOTICE: THE CONTENT OF THIS DOCUMENT IS SUBJECT TO CHANGE AND OWNED BY MICRON CORPORATION AND IS PROTECTED BY COPYRIGHT LAWS AND RELEVANT LAWS/REGULATIONS. ONLY EMPLOYEES OF MICRON ARE ALLOWED TO ACCESS AND USE THIS SENSITIVE INFORMATION WITHIN THE WORK SCOPE. UNLESS THEIR BEHAVIOR AND RESPECTIVE DUTIES AND OBLIGATIONS REQUIRED BY AGREEMENT WHICH IS NOT ALLOWED TO COPY, REPRODUCE, DISTRIBUTE, PUBLISH OR DISCLOSE IN WHOLE OR IN PART TO ANY OTHER PARTY WITHOUT MICRON'S PRIOR AND WRITTEN CONSENT.

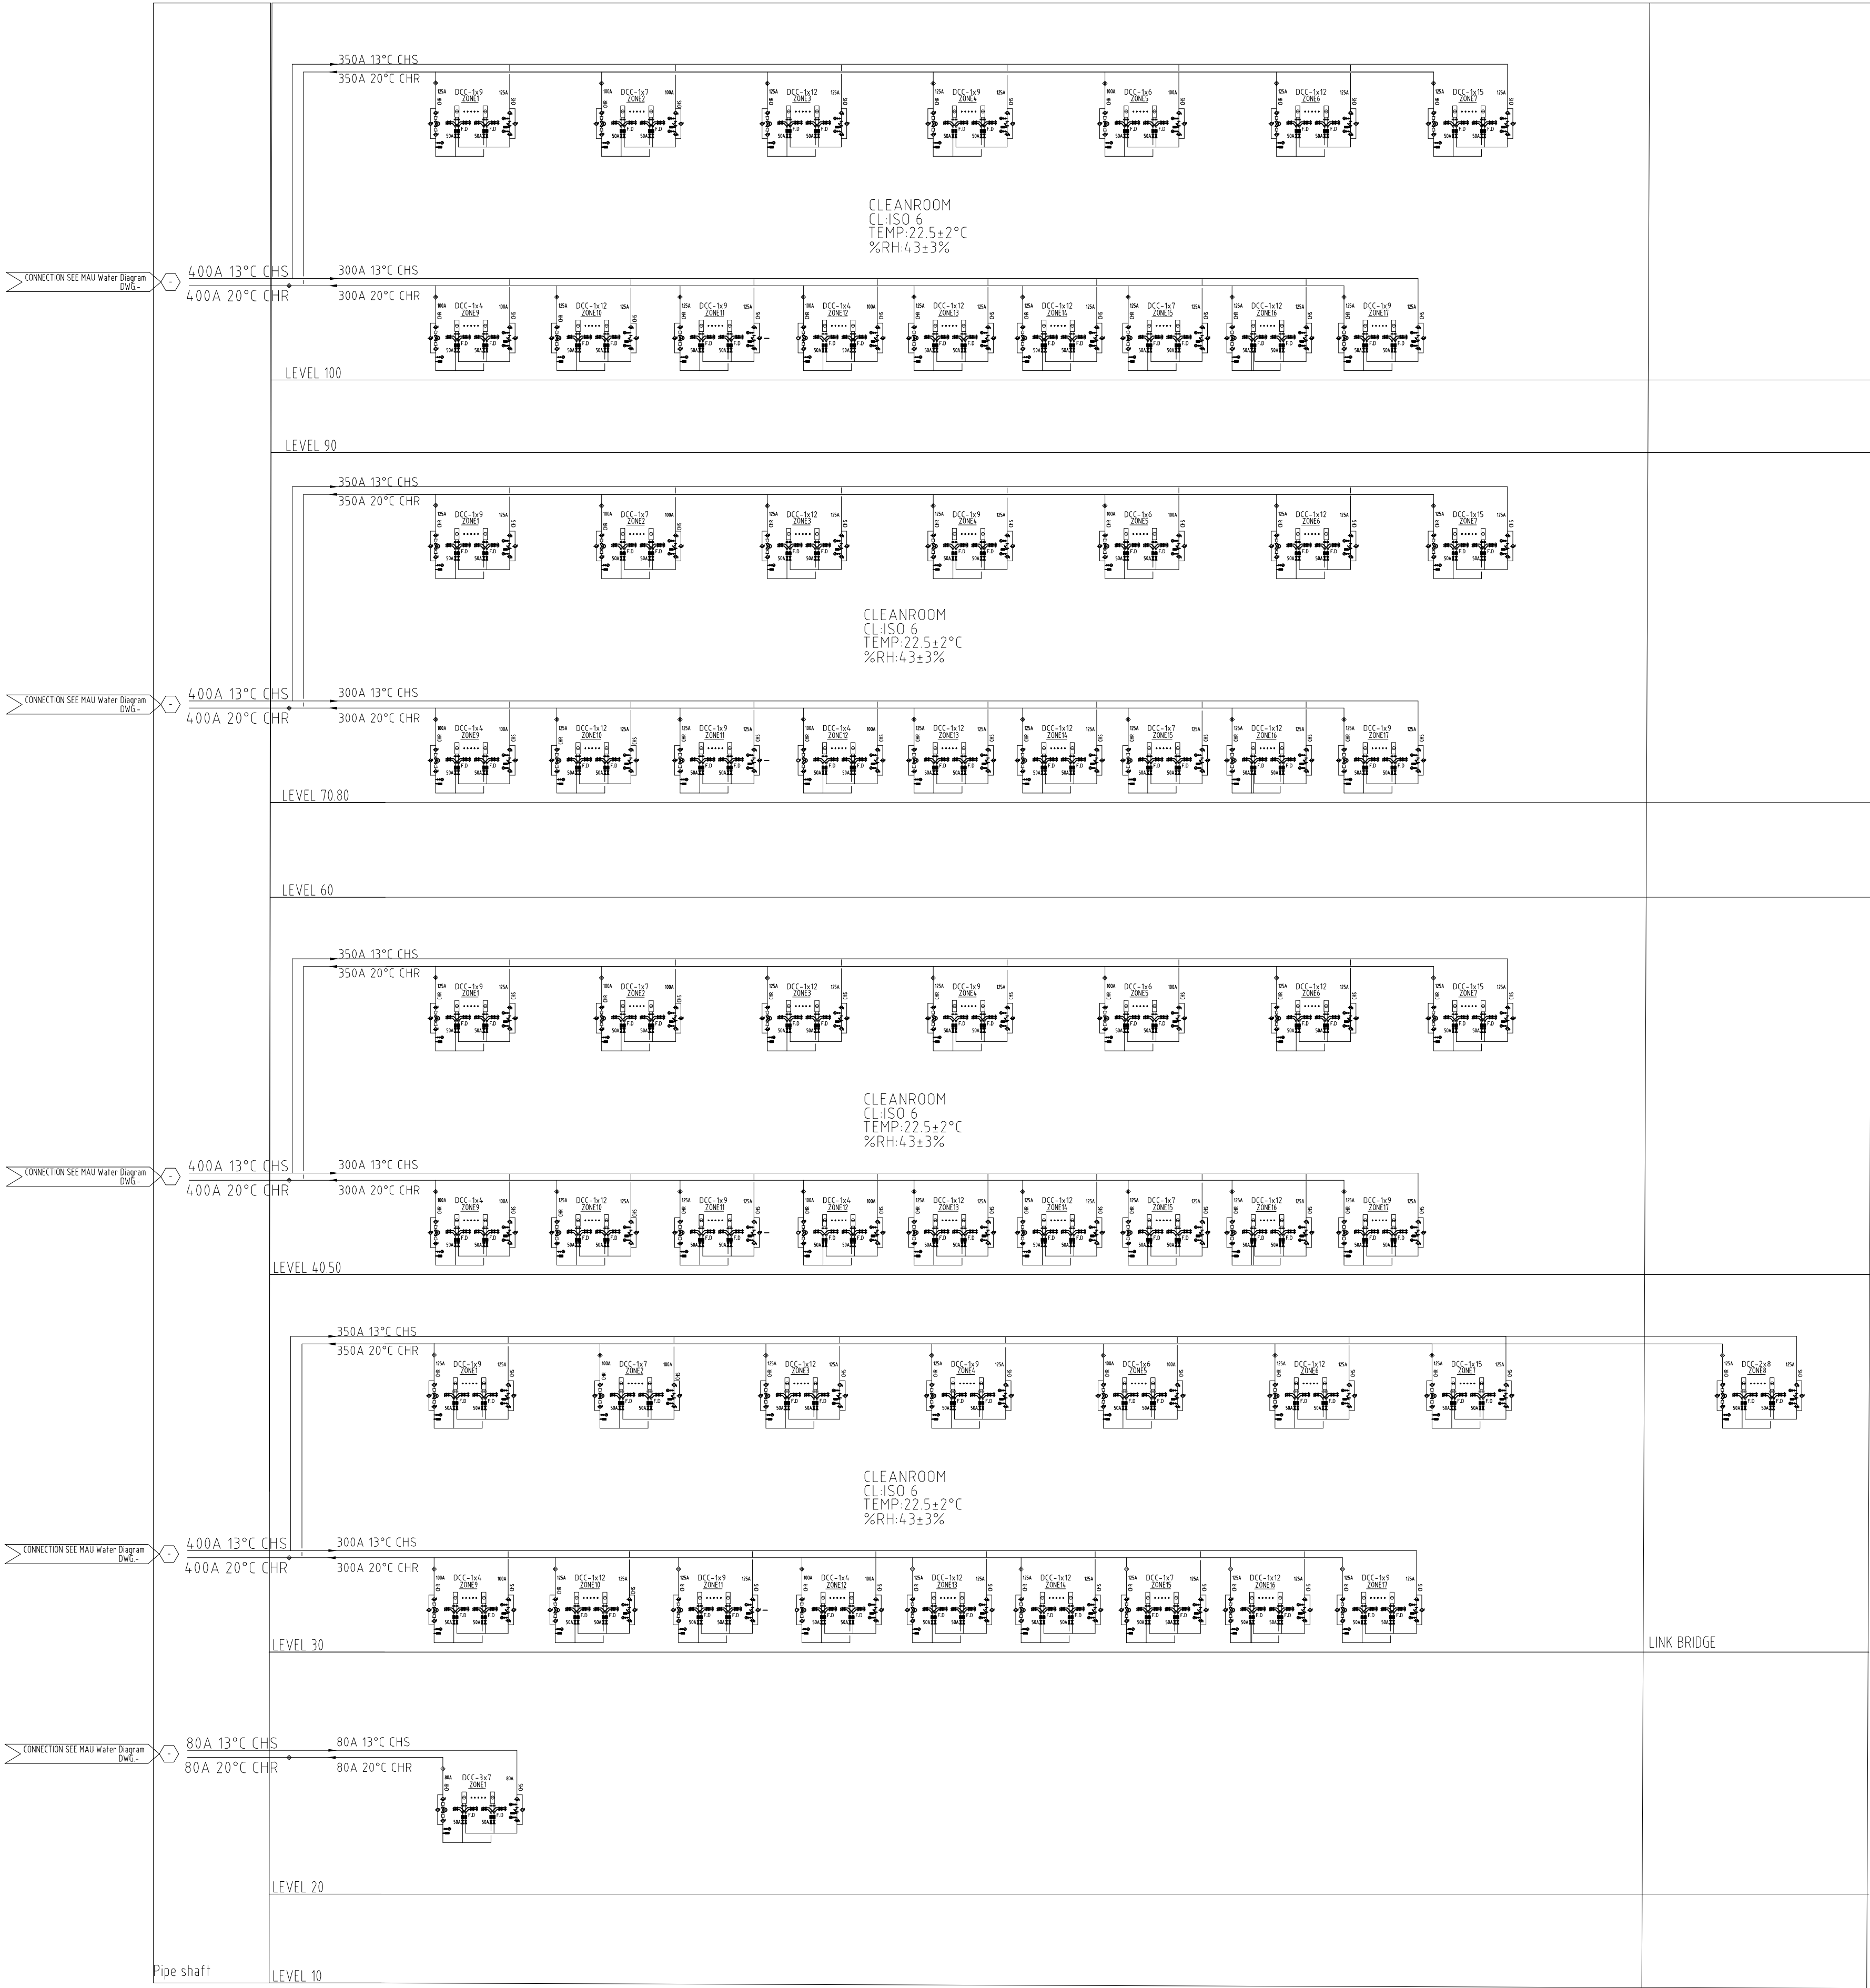

ARCHITECTURAL CONSULTANT


CIVIL & STRUCTURAL CONSULTANT

MECHANICAL & ELECTRICAL CONSULTANT

DESIGN MANAGER



PROJECT ADDRESS
North Coast Drive, Singapore

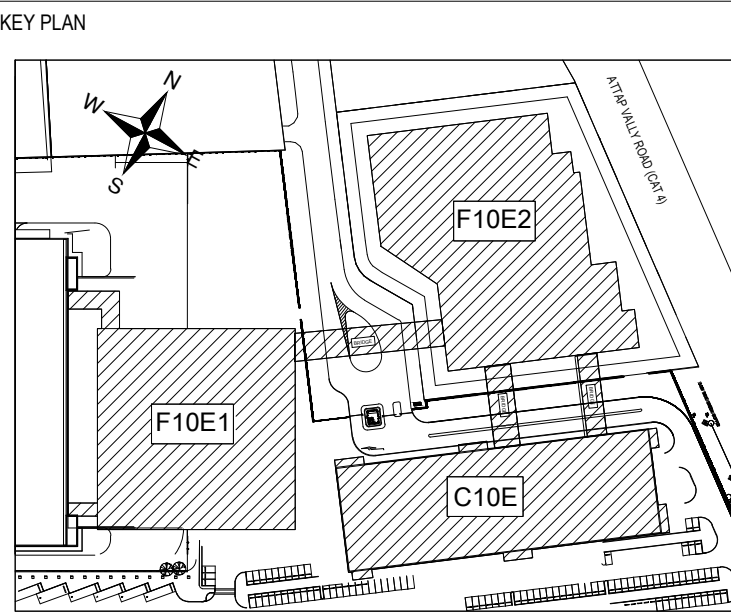

Secret
R3
Level

FOR REVIEW

REV	DATE	DESCRIPTION Revisions	ISSUED BY

PROJECT TITLE
Micron F10E Probe Project

PROJECT PHASE
A&E

DRAWING TITLE
**Flow Diagram_
DCC PIPING System F10E2**

DESIGNED : 設計者		DRAWN : 作者		CHECKED : 審圖員	
DATE : 01/14/26		JOB NO. :		SCALE :	
Micron DRAWING NO. F01-F10E-PFD-F10E2-00-K-103		REV B			
CTCI DRAWING NO.					
Reference Model					
A0~A999 or Vendor				SHEET: 1 OF 1	
				SIZE A1	