
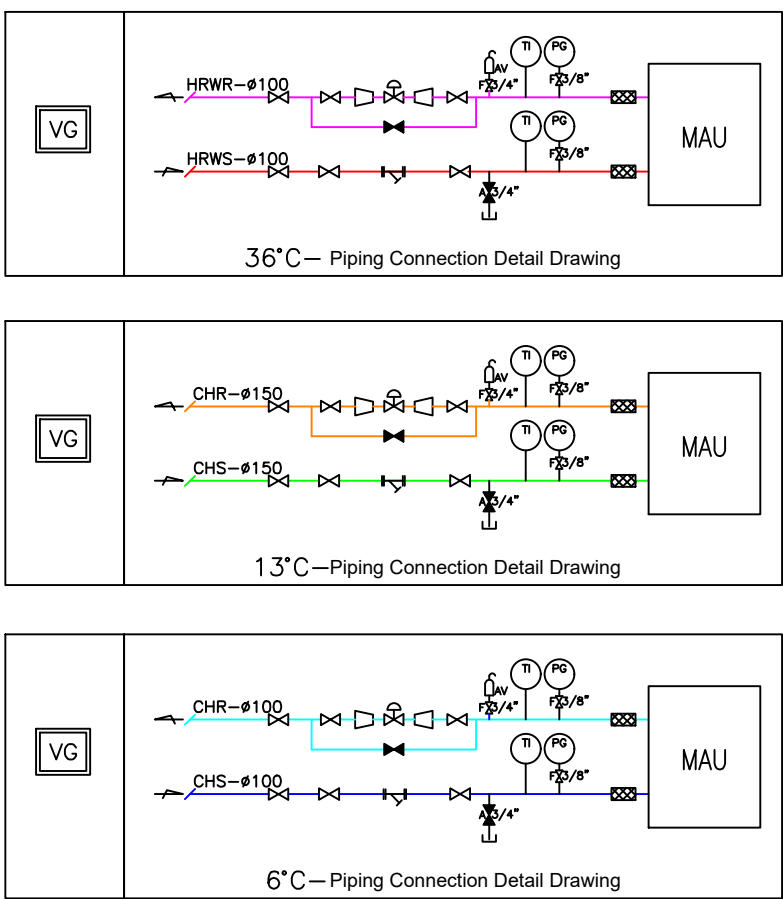


INTELLECTUAL NOTICE: THE CONTENTS OF THIS DOCUMENT IS SUBJECT TO MICRON'S PROPRIETARY RIGHTS AND ARE NOT TO BE REPRODUCED OR TRANSMITTED IN ANY FORM OR BY ANY MEANS, ELECTRONIC OR MECHANICAL, INCLUDING PHOTOCOPYING, RECORDING, OR BY ANY INFORMATION STORAGE AND RETRIEVAL SYSTEM, WITHOUT THE WRITTEN PERMISSION OF MICRON. ANY UNAUTHORIZED REPRODUCTION OR TRANSMISSION OF THIS DOCUMENT IS STRICTLY PROHIBITED. MICRON ASSUMES NO LIABILITY FOR ANY ERRORS OR OMISSIONS IN THIS DOCUMENT. THE USER OF THIS DOCUMENT SHALL BE RESPONSIBLE FOR OBTAINING NECESSARY INFORMATION FROM THE APPROPRIATE SOURCES AND FOR OBTAINING NECESSARY INFORMATION FROM THE APPROPRIATE SOURCES. MICRON ASSUMES NO LIABILITY FOR ANY ERRORS OR OMISSIONS IN THIS DOCUMENT. THE USER OF THIS DOCUMENT SHALL BE RESPONSIBLE FOR OBTAINING NECESSARY INFORMATION FROM THE APPROPRIATE SOURCES AND FOR OBTAINING NECESSARY INFORMATION FROM THE APPROPRIATE SOURCES.

MAU PIPING SYSTEM DIAGRAM

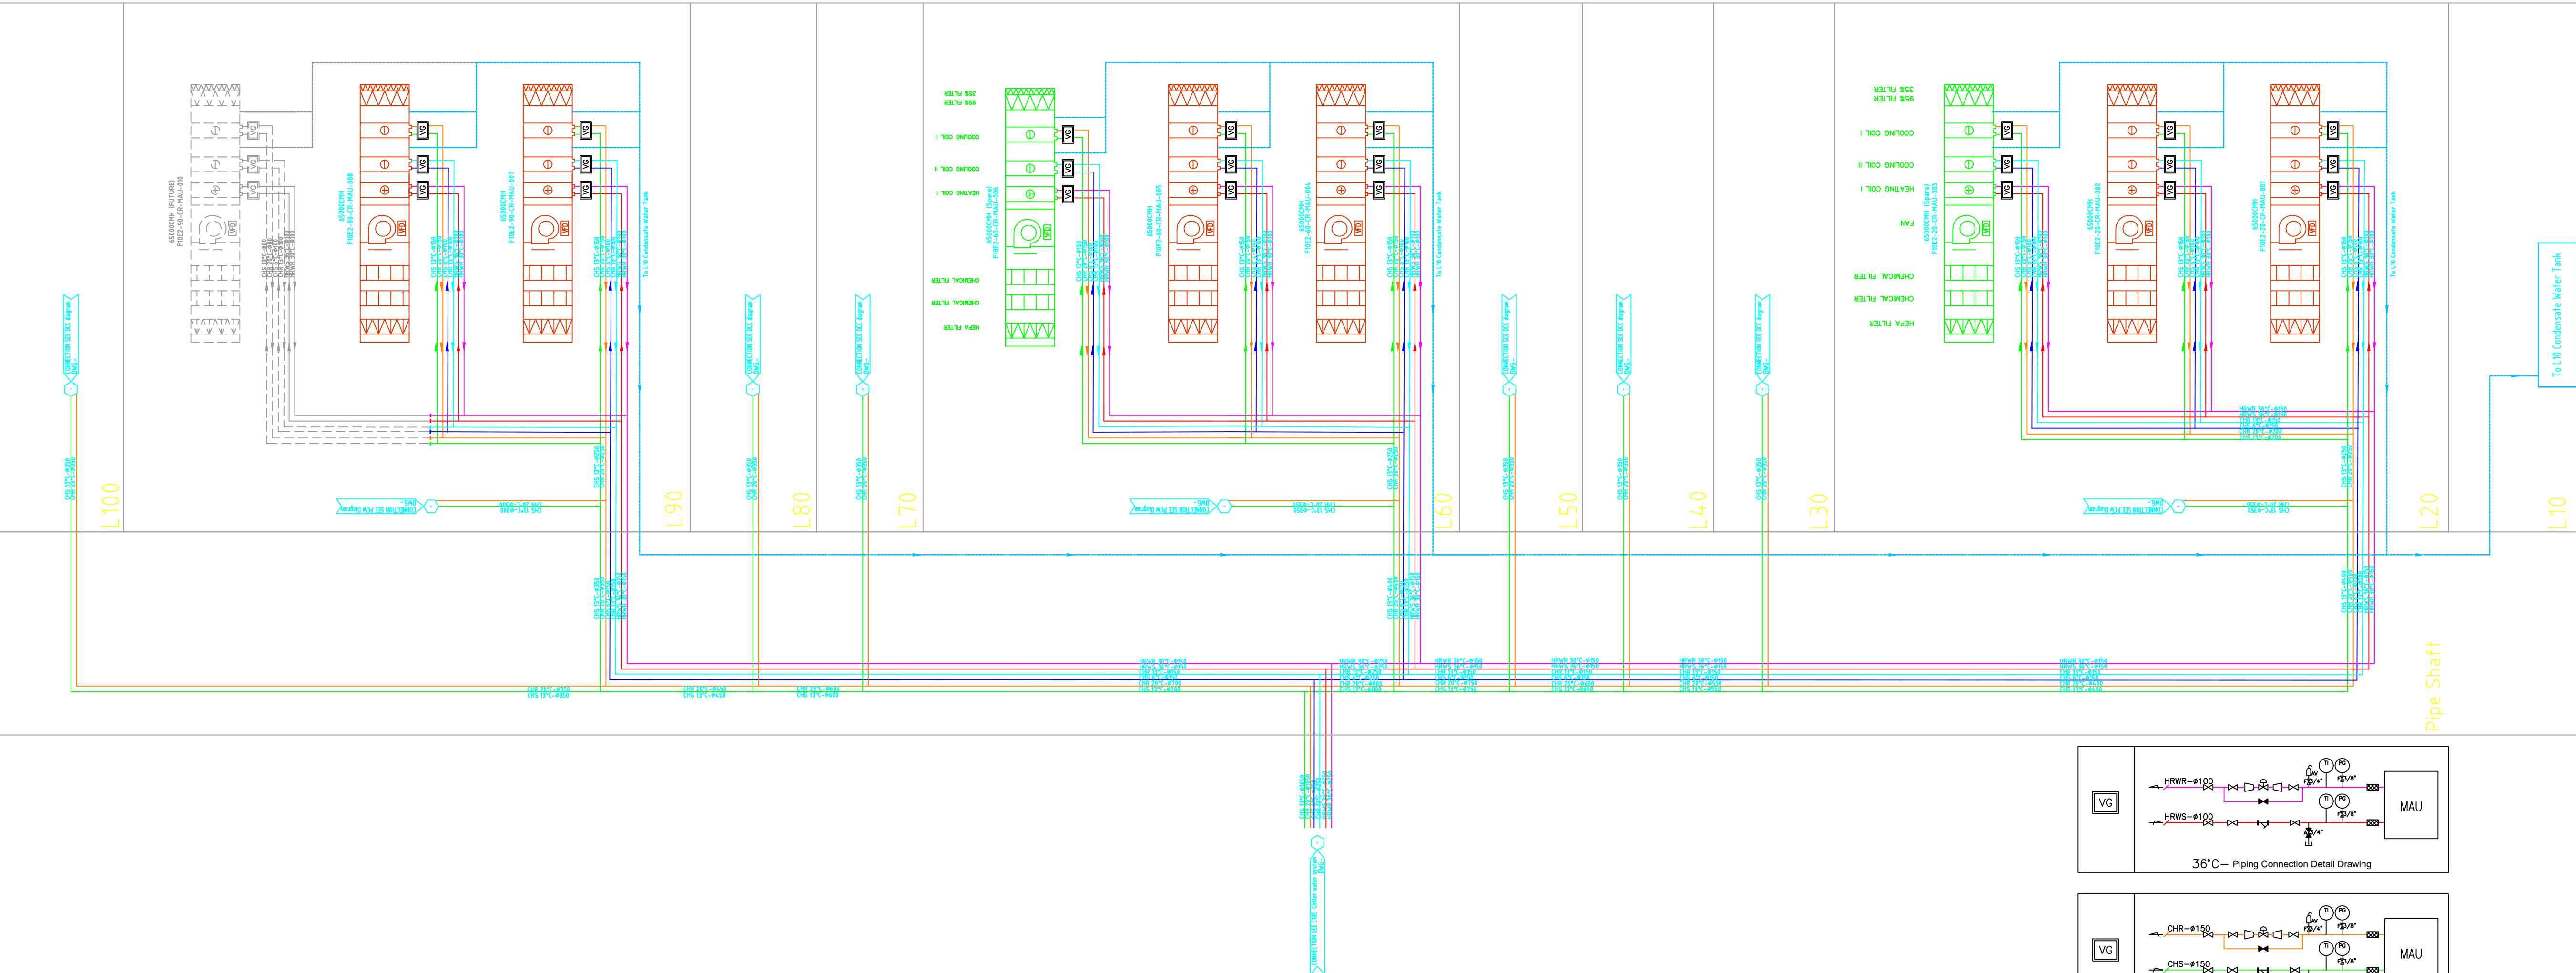

ARCHITECTURAL CONSULTANT

CIVIL & STRUCTURAL CONSULTANT


MECHANICAL & ELECTRICAL CONSULTANT

DESIGN MANAGER



PROJECT ADDRESS
North Coast Drive, Singapore

KEY PLAN

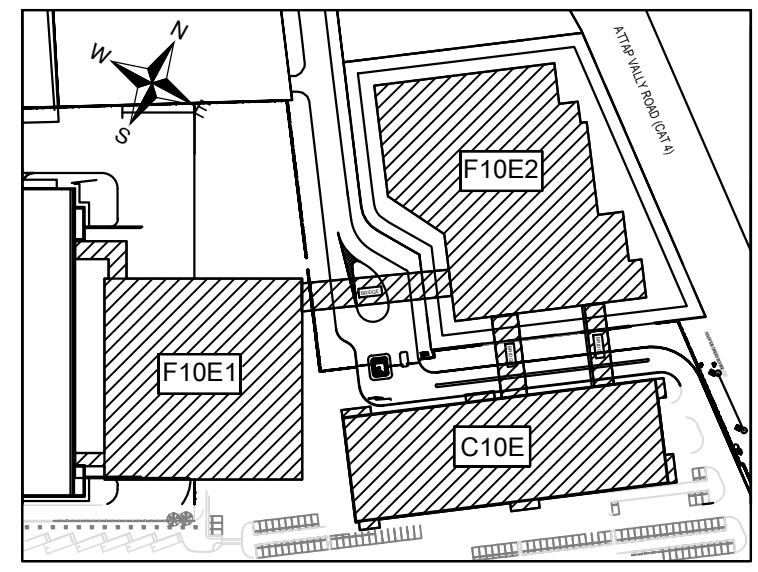

Secret
R3
Level

FOR REVIEW

REV	DATE	DESCRIPTION	ISSUED BY

PROJECT TITLE
Micron F10E Probe Project

PROJECT PHASE
A&E

DRAWING TITLE
FLOW DIAGRAM-
MAU PIPING SYSTEM F10E2

DESIGNED : 設計者	DRAWN : 作者	CHECKED : 審圖員
DATE : 01/26/26	JOB NO. :	SCALE :
Micron DRAWING NO. : F01-F10E-PFD-F10E2-00-K-101	REV	
CTCI DRAWING NO. :	0A	
Reference Model		
CTCI	SHEET: 1 OF 1	SIZE A1