


DISCLAIMER NOTICE: THE CONTENT OF THIS DOCUMENT IS SUBJECT TO THE TERMS AND CONDITIONS OF THE MICRON CORPORATION AND IS NOT TO BE REPRODUCED OR TRANSMITTED IN ANY FORM OR BY ANY MEANS, ELECTRONIC OR MECHANICAL, INCLUDING PHOTOCOPYING, RECORDING, OR BY ANY INFORMATION STORAGE AND RETRIEVAL SYSTEM, WITHOUT THE WRITTEN PERMISSION OF MICRON CORPORATION. ANY REPRODUCTION OR TRANSMISSION OF THIS DOCUMENT WITHOUT THE WRITTEN PERMISSION OF MICRON CORPORATION IS STRICTLY PROHIBITED. THE CONTENT OF THIS DOCUMENT IS SUBJECT TO THE TERMS AND CONDITIONS OF THE MICRON CORPORATION AND IS NOT TO BE REPRODUCED OR TRANSMITTED IN ANY FORM OR BY ANY MEANS, ELECTRONIC OR MECHANICAL, INCLUDING PHOTOCOPYING, RECORDING, OR BY ANY INFORMATION STORAGE AND RETRIEVAL SYSTEM, WITHOUT THE WRITTEN PERMISSION OF MICRON CORPORATION. ANY REPRODUCTION OR TRANSMISSION OF THIS DOCUMENT WITHOUT THE WRITTEN PERMISSION OF MICRON CORPORATION IS STRICTLY PROHIBITED.

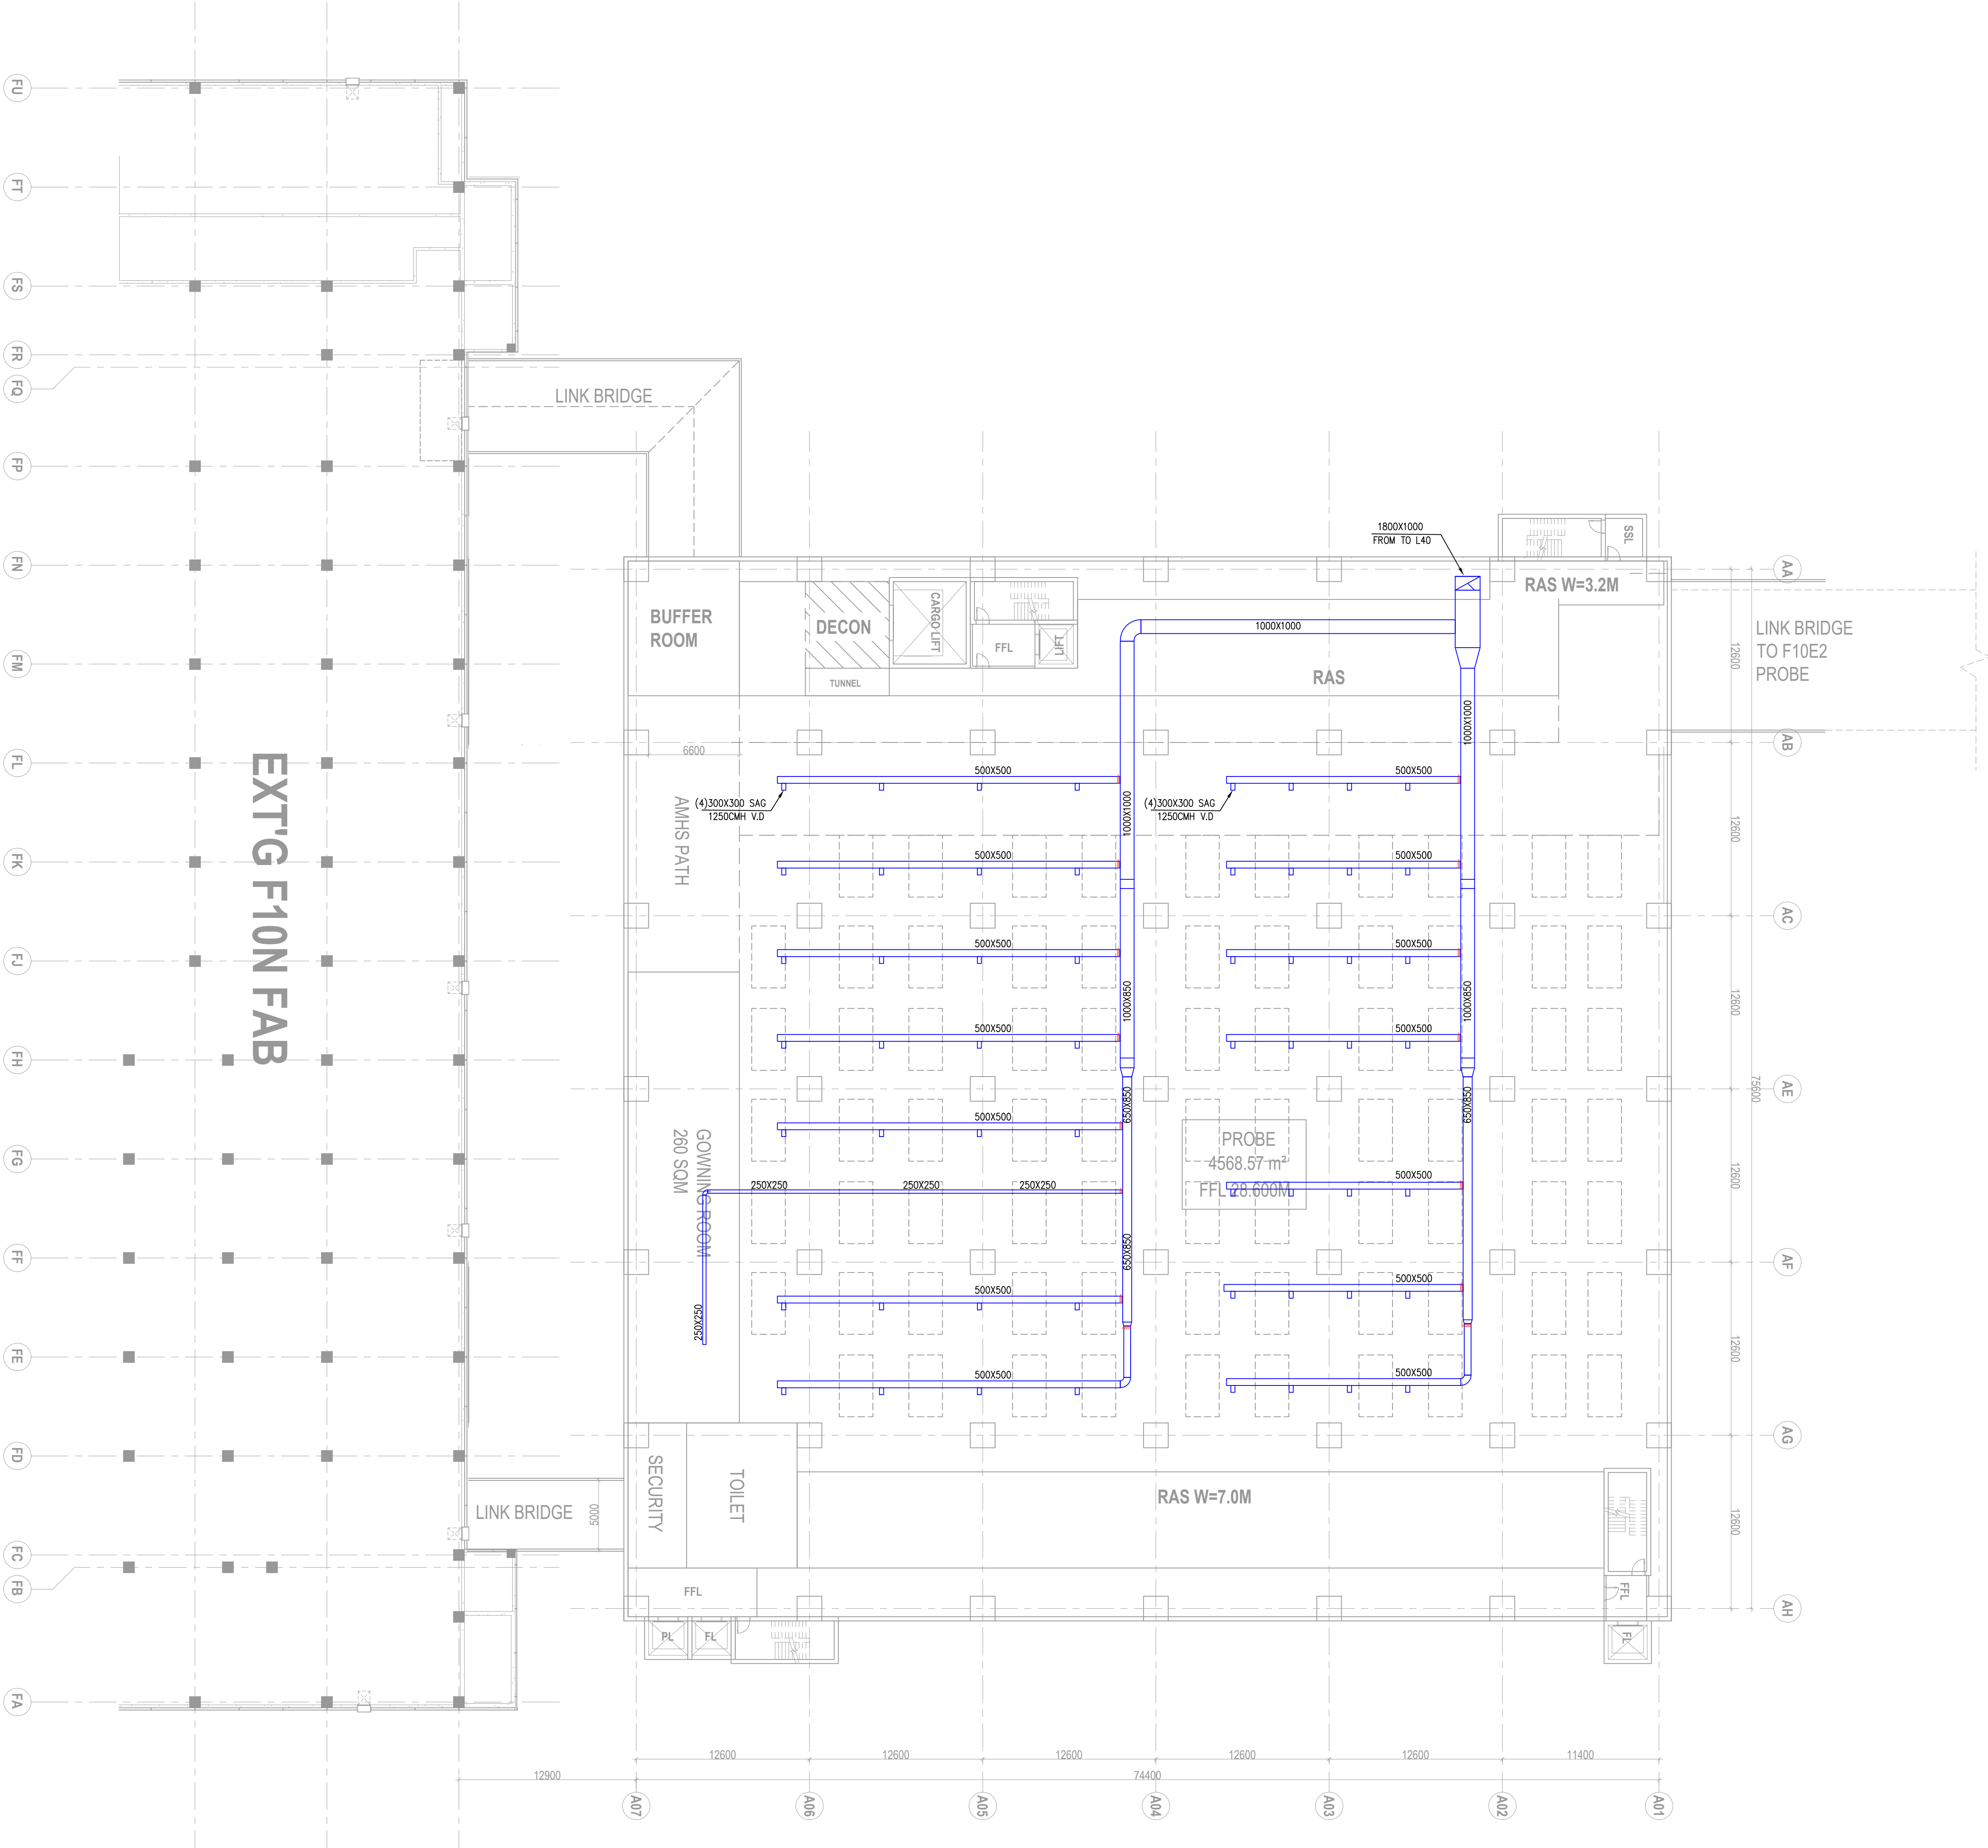

OWNER / DEVELOPER

ARCHITECTURAL CONSULTANT

CIVIL & STRUCTURAL CONSULTANT

MECHANICAL & ELECTRICAL CONSULTANT

DESIGN MANAGER

CTCI Singapore Pte. Ltd.

PROJECT ADDRESS
North Coast Drive, Singapore

KEY PLAN

Secret

R3

Level

FOR REVIEW

REV	DATE	DESCRIPTION	ISSUED BY
		Revisions	

PROJECT TITLE
Micron F10E Probe Project

PROJECT PHASE
A&E

DRAWING TITLE
Floor Plan
MAU DUCTS LAYOUT F10E1 L30

DESIGNED :	設計者	DRAWN :	作者	CHECKED :	審圖員
DATE :	02/12/26	JOB NO. :		SCALE :	
Micron DRAWING NO.	F01-F10E-LAY-F10E1-03-K-134				REV
CTCI DRAWING NO.					B
Reference Model					
CTCI	SHEET: 1 OF 1				SIZE A1