


DISCLAIMER NOTICE: THE CONTENT OF THIS DOCUMENT IS SUBJECT TO THE ASSUMPTIONS, INFORMATION AND OWNERSHIP OF MICRON CORPORATION AND IS NOT TO BE USED FOR ANY OTHER PURPOSES WITHOUT MICRON'S WRITTEN PERMISSION. MICRON CORPORATION AND ITS SUBSIDIARIES ARE NOT RESPONSIBLE FOR ANY DAMAGE, LOSS OR INJURY TO ANY PERSON OR PROPERTY, OR FOR ANY OTHER LOSS OR INJURY, ARISING FROM THE USE OF THIS DOCUMENT. MICRON CORPORATION AND ITS SUBSIDIARIES ARE NOT RESPONSIBLE FOR ANY DAMAGE, LOSS OR INJURY TO ANY PERSON OR PROPERTY, OR FOR ANY OTHER LOSS OR INJURY, ARISING FROM THE USE OF THIS DOCUMENT.

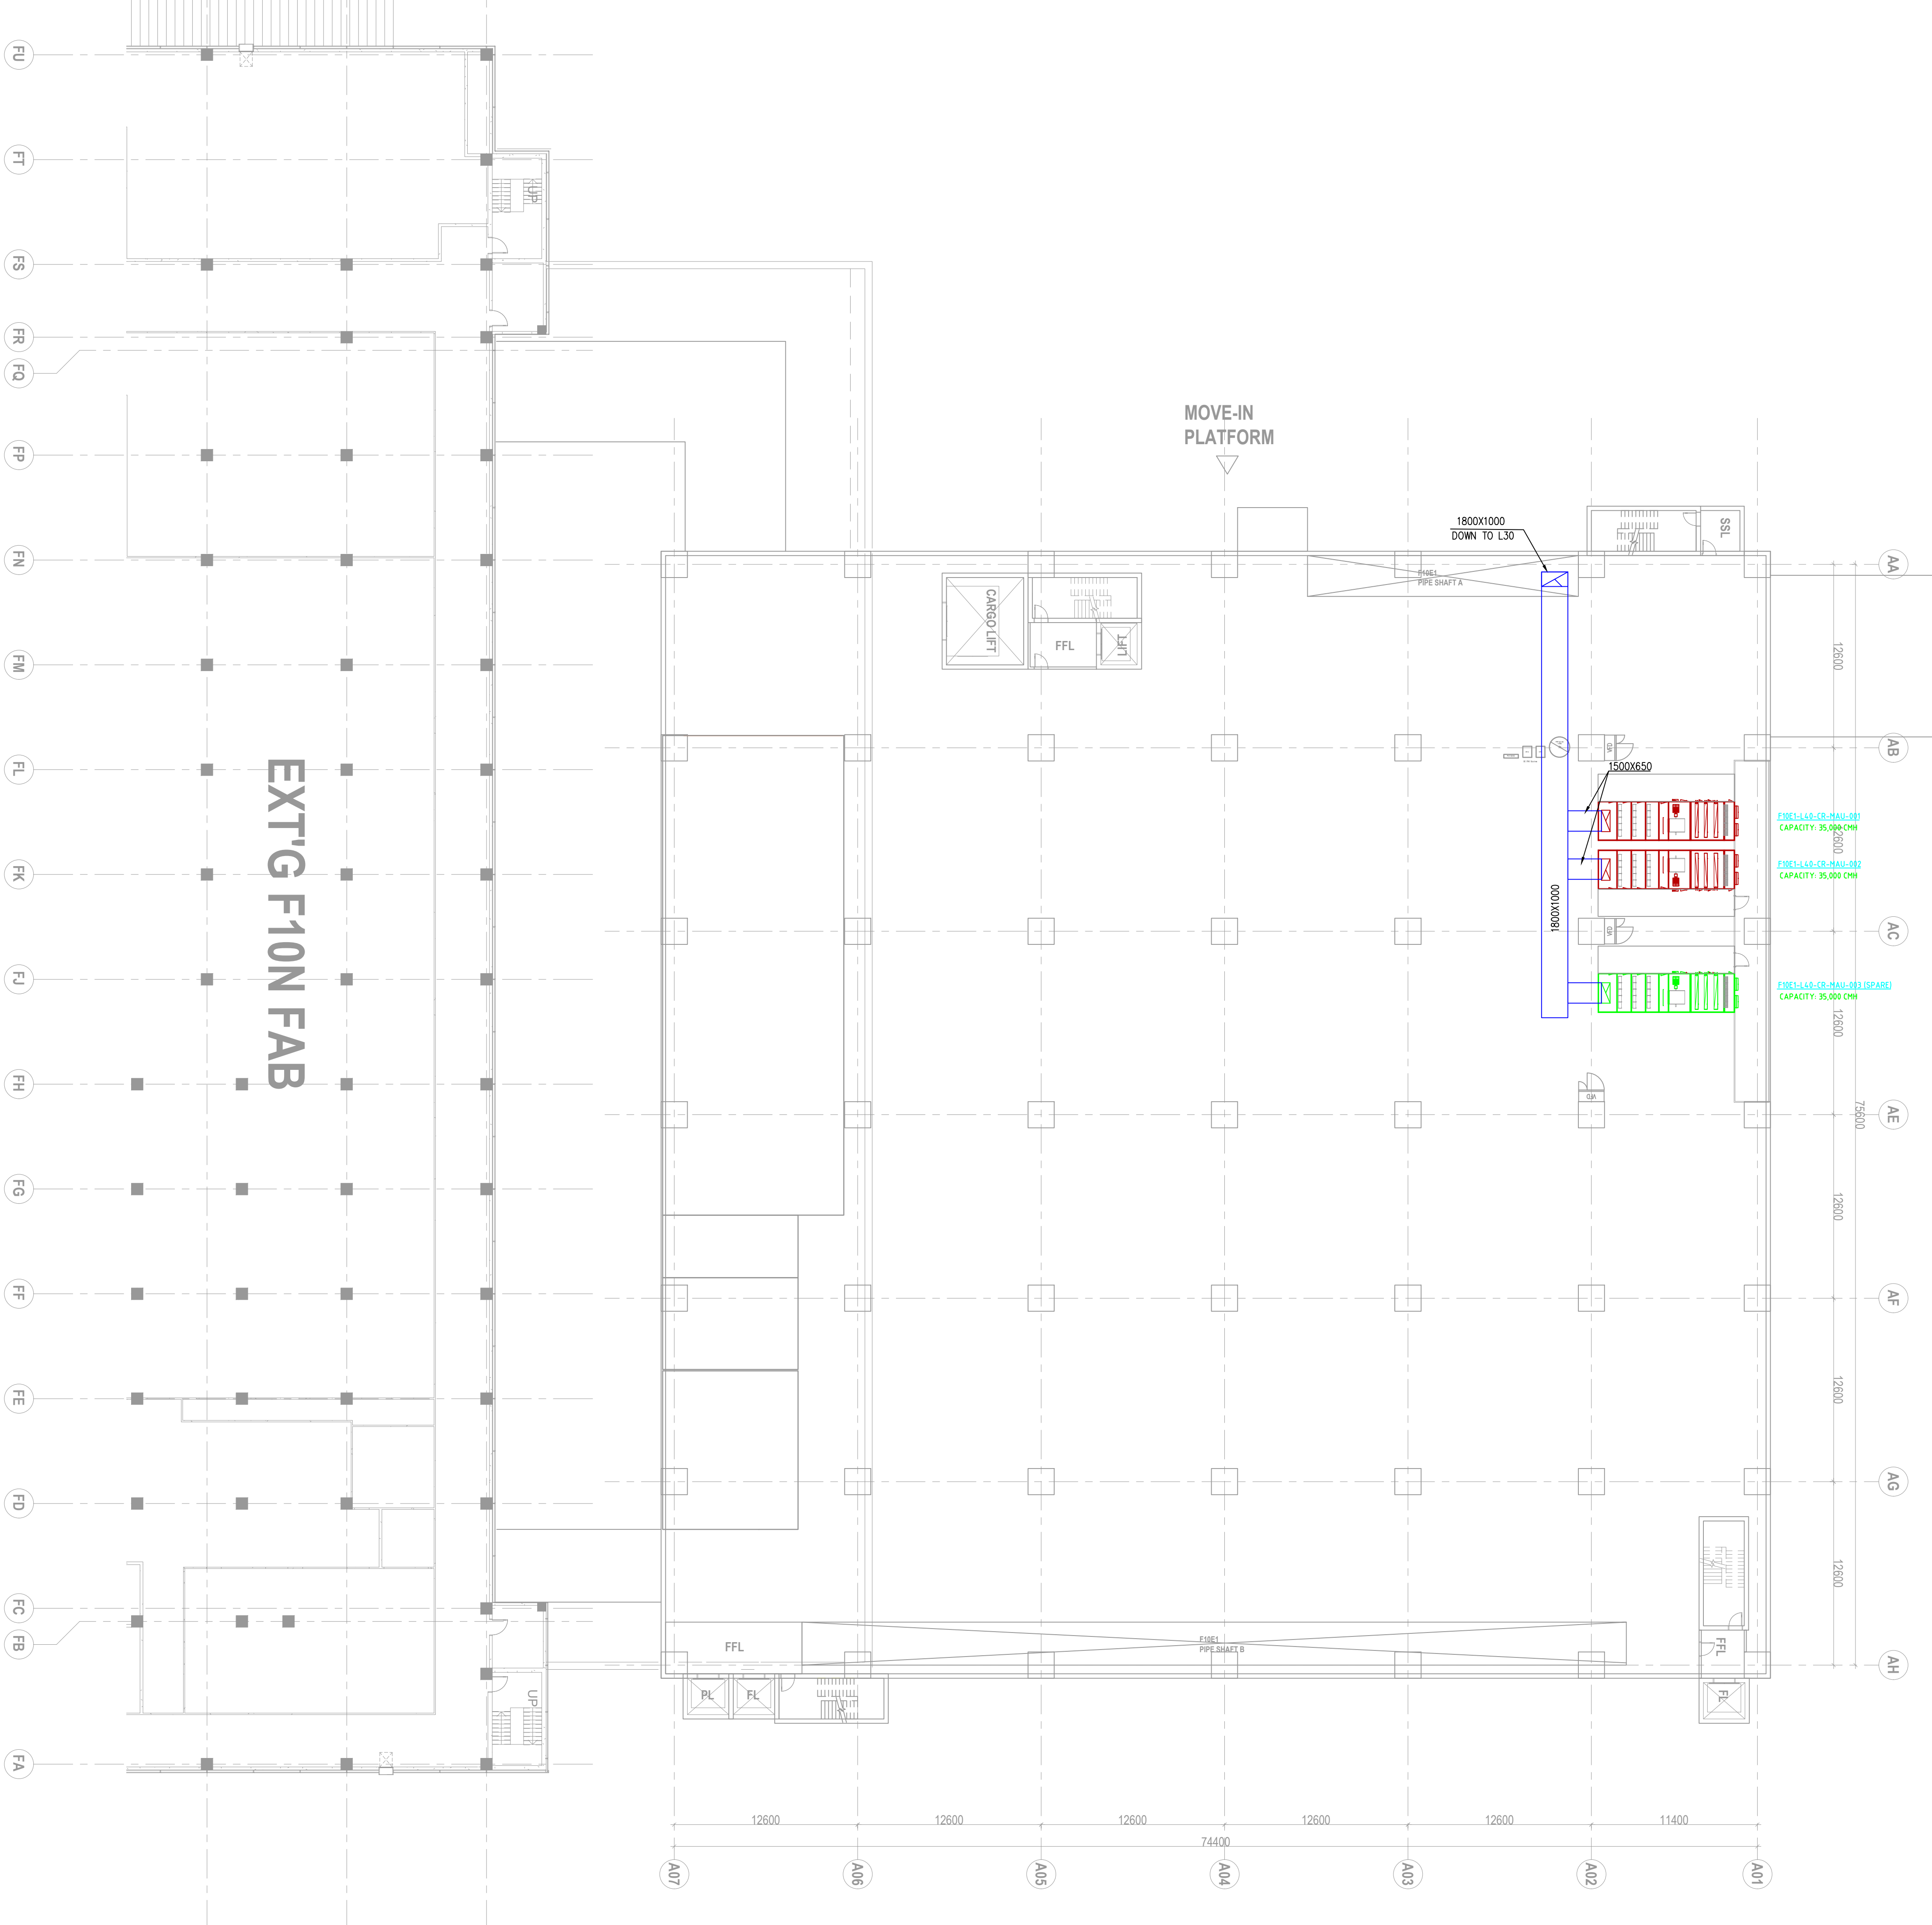

OWNER / DEVELOPER

ARCHITECTURAL CONSULTANT

CIVIL & STRUCTURAL CONSULTANT

MECHANICAL & ELECTRICAL CONSULTANT

DESIGN MANAGER

CTCI Singapore Pte. Ltd.

PROJECT ADDRESS
North Coast Drive, Singapore

KEY PLAN

Secret
R3
Level

FOR REVIEW

REV	DATE	DESCRIPTION	ISSUED BY
		Revisions	

PROJECT TITLE

Micron F10E Probe Project

PROJECT PHASE

A&E

DRAWING TITLE

Floor Plan
MAU DUCTS LAYOUT F10E1 L40

DESIGNED : 設計者	DRAWN : 作者	CHECKED : 審圖員
DATE : 02/12/26	JOB NO. :	SCALE :
Micron DRAWING NO. : F01-F10E-LAY-F10E1-04-K-134	REV	
CTCI DRAWING NO. :	0A	
Reference Model		
CTCI	SHEET: 1 OF 1	SIZE A1