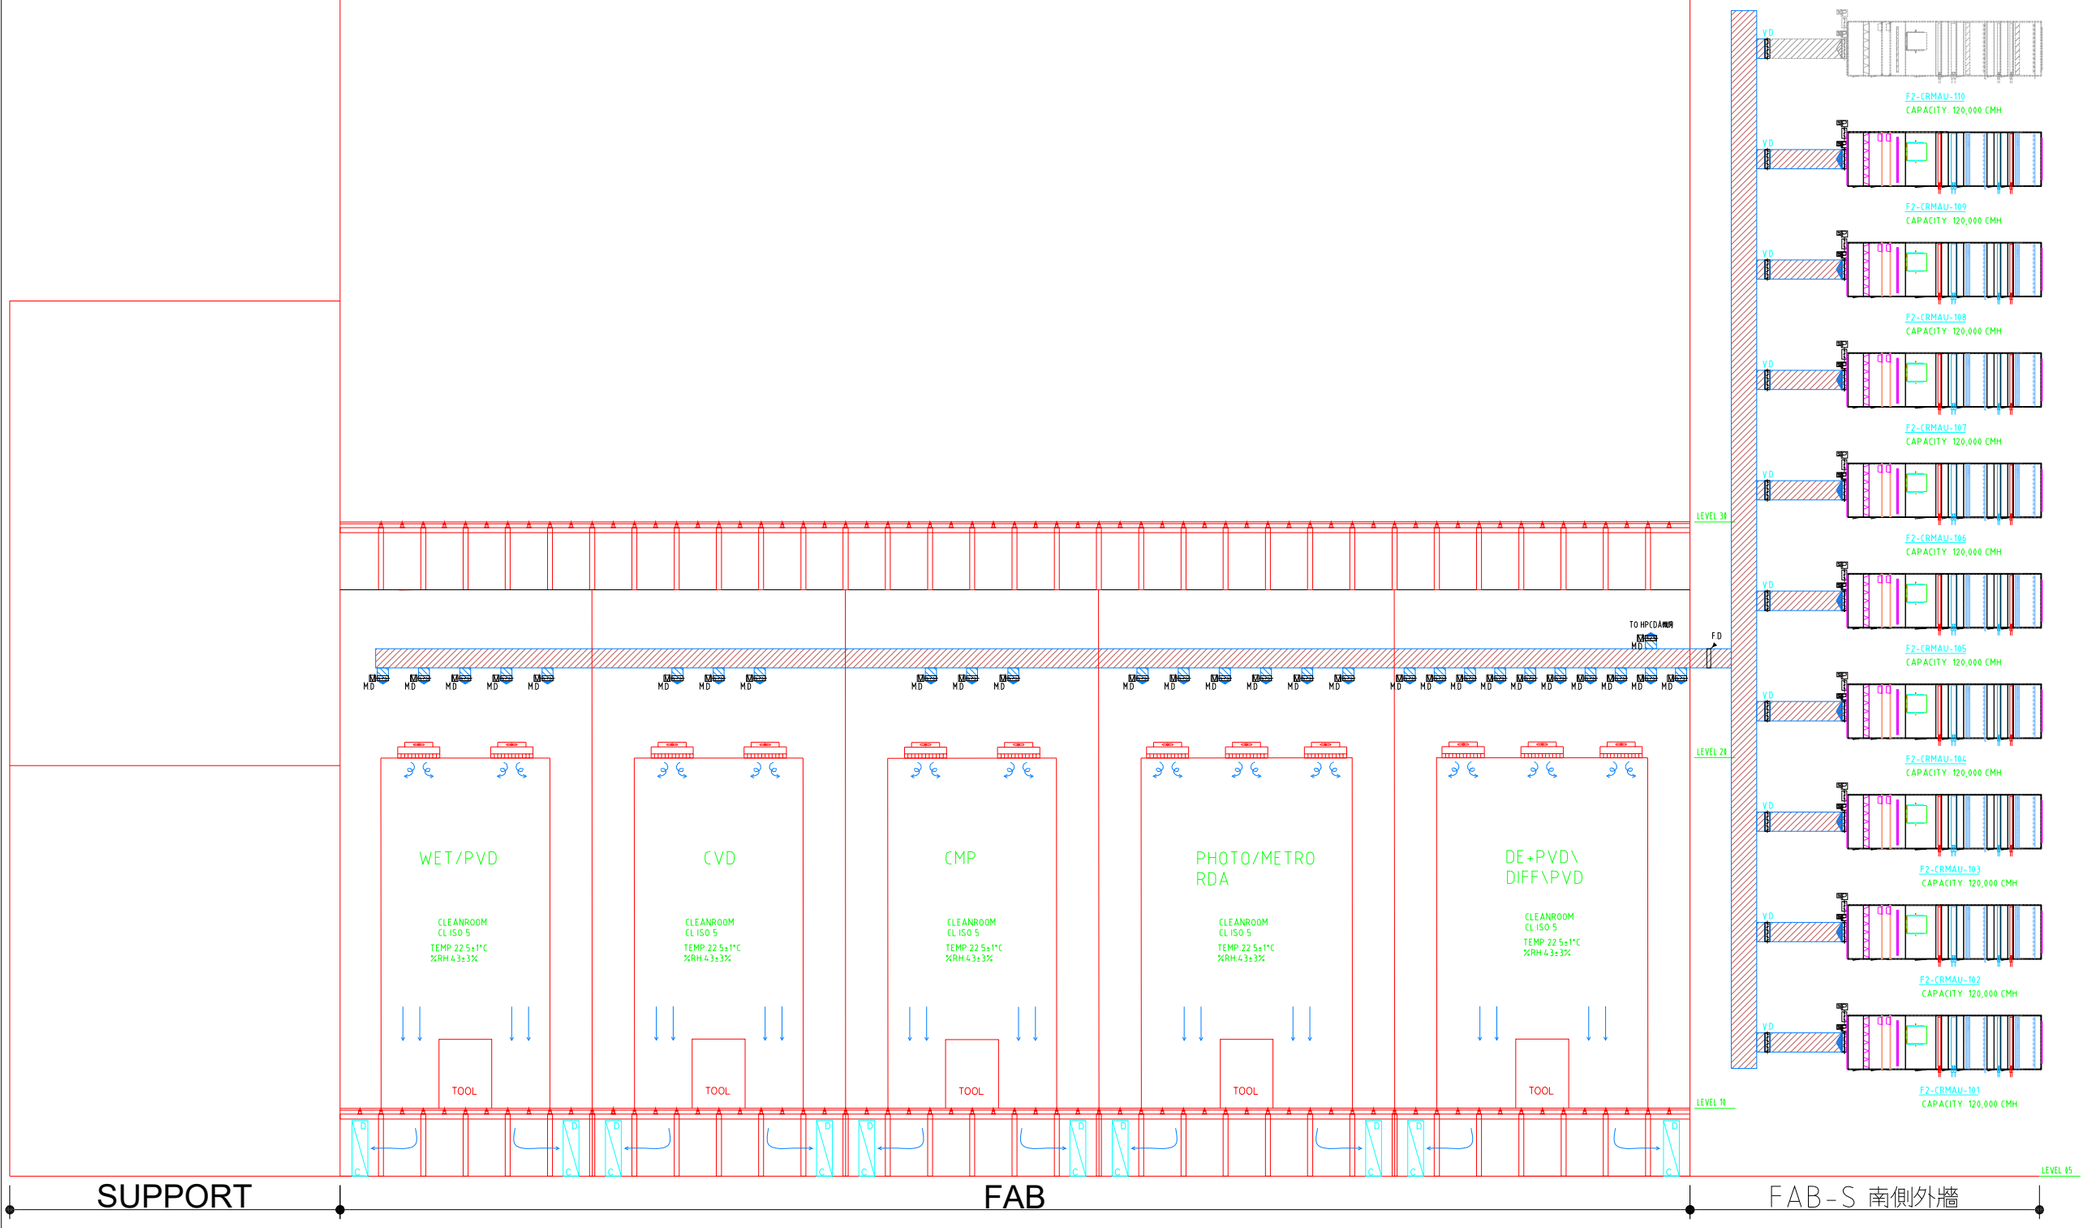

OWNER / DEVELOPER

micron™

ARCHITECTURAL CONSULTANT

QUO 陳昆豐建築師事務所

CIVIL & STRUCTURAL CONSULTANT

禾森工程顧問有限公司

MECHANICAL & ELECTRICAL CONSULTANT & CONTRACTOR

YKE 洋基工程股份有限公司
YANKEY Engineering Co.,Ltd

SUB-CONTRACTOR

PROJECT ADDRESS

KEY PLAN

REV	DATE	DESCRIPTION	ISSUED BY

Revisions

PROJECT TITLE

美光台南廠188K增建工程

MECH

PROJECT PHASE

Concept Design

DRAWING TITLE

DE_MMTN_F2_B002_M_DUCT_1001
CR MAU風管系統流程圖
FLOW DIAGRAM-MAU DUCT SYSTEM

DESIGNED :	DRAWN :	CHECKED :
DATE : 2025/08/25	JOB NO. :	SCALE :

DRAWING NO. **DE_MMTN_F2_B002_M_DUCT_1001** REV **A**

[SHEET PURPOSE]

SHEET: SIZE