


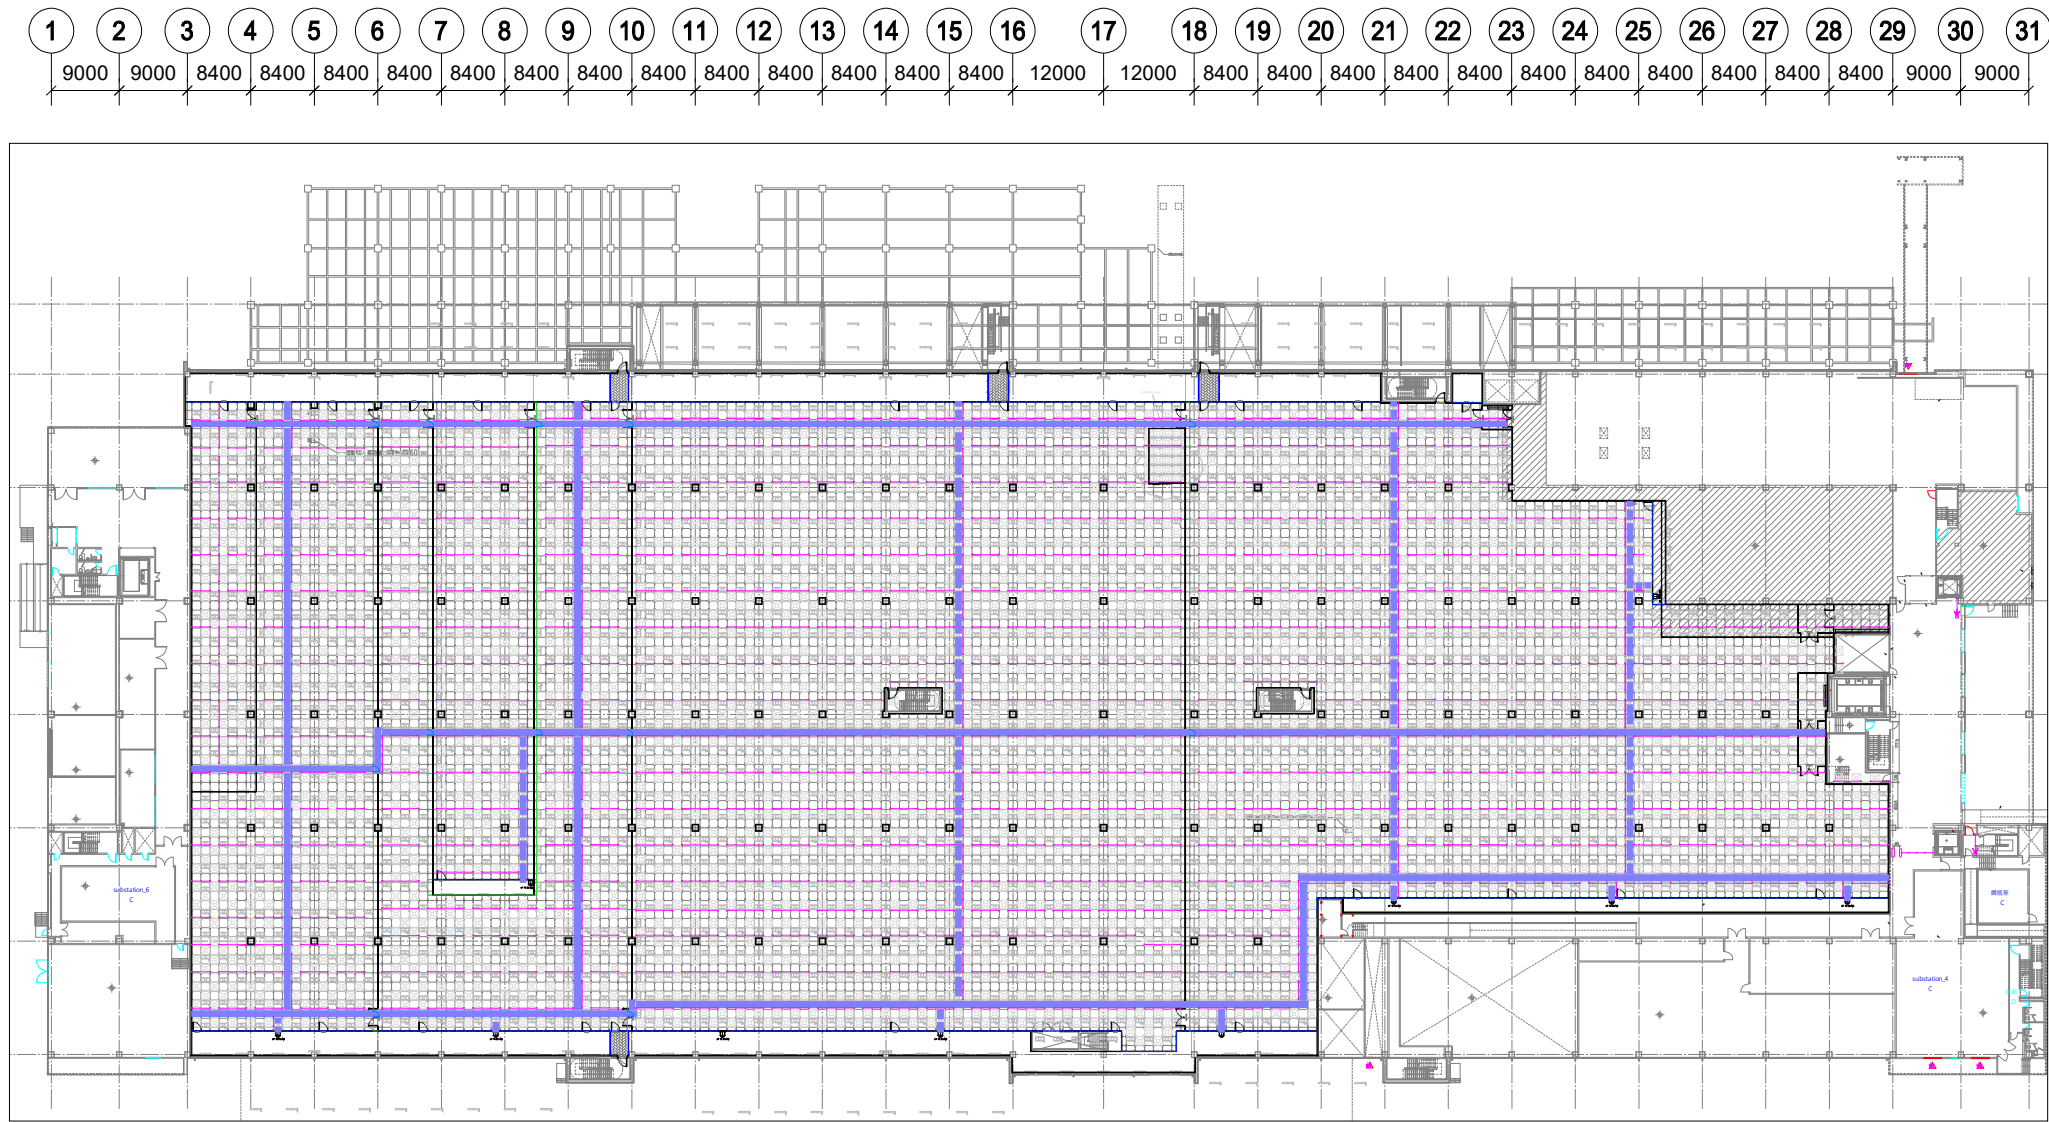

SYMBOL	DESCRIPTION	REMARK
	欄杆扶手 H=1100mm(SUS 304)	
	欄杆鍊條 H=1100mm	
	安全母索施作離天花板 H=1000mm	
	貓道板 749mm(W)×1196.5mm(L)×43mm(D)	主走道
	貓道板 749mm(W)×596.5mm(L)×43mm(D)	主走道V S 燈具旁
	鍍鋅鐵皮封板(高架地板下 (H=550mm) 鍍鋅鐵皮封板(天花板上方)	
	單開銅板門 800W x 1500H 安裝於天花板上(鐵皮上開門, 須氣密)	

※實際尺寸依現場實際可施作為準。

OWNER / DEVELOPER

ARCHITECTURAL CONSULTANT

QUO 陳昆豐建築師事務所

CIVIL & STRUCTURAL CONSULTANT

禾森工程顧問有限公司

MECHANICAL & ELECTRICAL CONSULTANT & CONTRACTOR

洋基工程股份有限公司
YANKEY Engineering Co.,Ltd

SUB-CONTRACTOR

PROJECT ADDRESS

KEY PLAN

PROJECT TITLE

美光台南廠188K增建工程

PROJECT PHASE

MECH
Concept Design

DRAWING TITLE

DE_MMTN_F2_B002_B_CATW_2L15
F2 L15 貓道平面配置圖
F2 L15 CATWALK LAYOUT

DESIGNED :

DRAWN :

CHECKED :

DATE :

2025/08/17

JOB NO. :

SCALE :

A3:1/1000

DRAWING NO.

DE_MMTN_F2_B002_B_CATW_2L15

REV

A

[SHEET PURPOSE]

SHEET:

SIZE